


Quarto adaptável e fechamento da claraboia

A cortina fecha a sala de estar como quarto de hóspede; a claraboia ganha fechamento elétrico em 2027/28, com a infraestrutura feita agora.

cama de casal com 0,60 m de circulação nos três lados

8,78 m² dentro da cortina · claraboia não furável

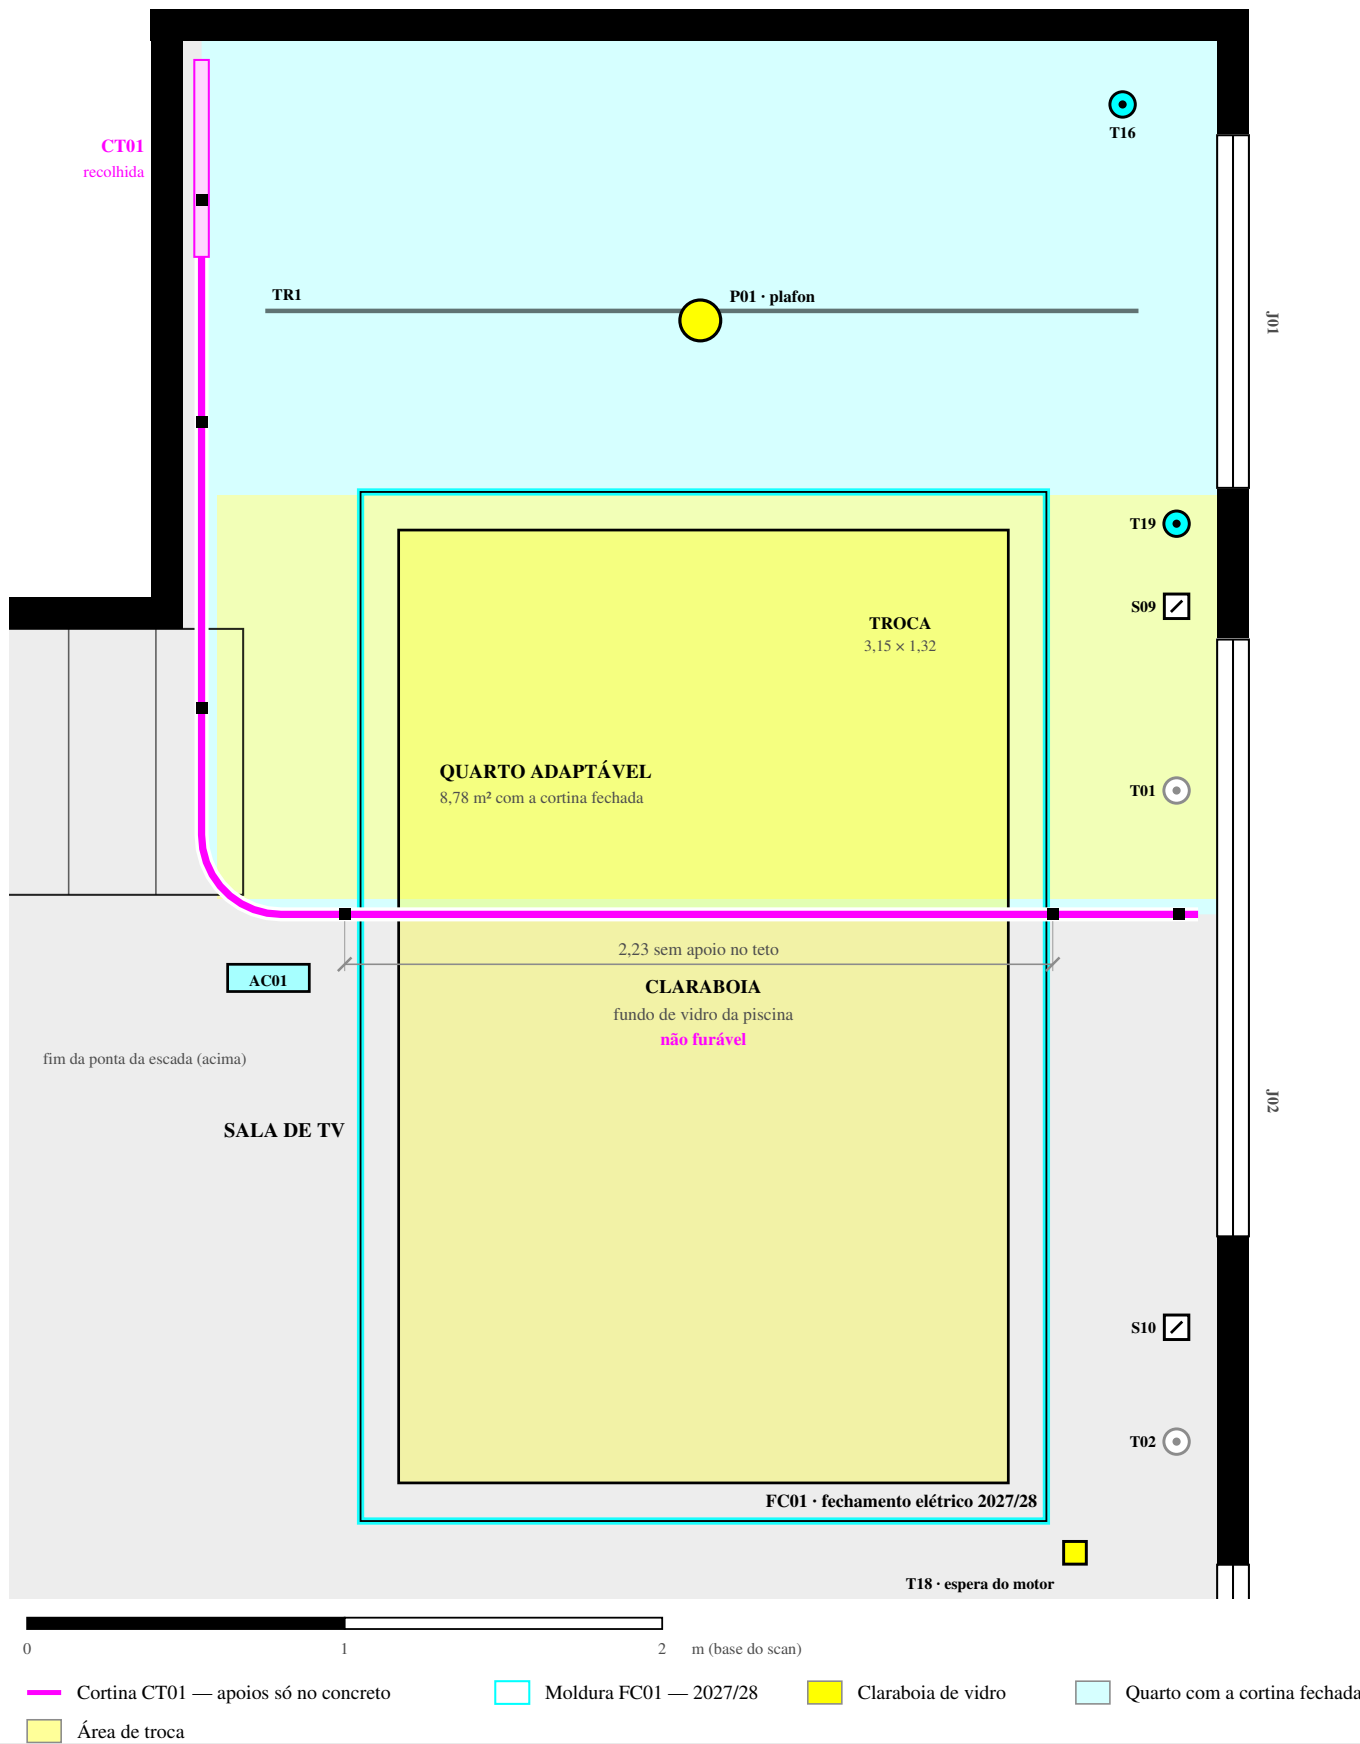

Circulação mínima adotada de 0,60 m em volta da cama; cortina com ~5 cm de tecido de cada lado do eixo do trilho. Medidas sobre o scan de 02.09.2026.

O vidro da claraboia não recebe fixação. Apoios do trilho e da moldura só no concreto em volta, com posição confirmada em estrutura antes de furar.

ESTUDO PRELIMINAR — NÃO LIBERADO PARA EXECUÇÃO | CADERNO ALTERNATIVO A | 01/10/2026

QUARTO ADAPTÁVEL — NÚMEROS

Grandeza	Valor	Leitura
Área dentro da cortina	8,78 m²	sala de estar 5,90 m² + faixa da sala de TV até a ponta da escada
Largura × profundidade	3,20 × 2,75 m	da cortina à fachada · da parede norte à cortina
Linha da cortina	2,85 m	da parede norte — 0,06 m além da ponta da escada
Trilho CT01	5,72 m	eixo, do canto da sala de estar à fachada leste
Cortina recolhida	~0,62 m de trilho	pacote no canto noroeste, junto à parede
Vão sem apoio no teto	2,23 m	sob a claraboia: perfil autoportante

CAMA x CIRCULAÇÃO — LESTE-OESTE, JUNTO À PAREDE NORTE

Cama	Medida m	Pé oeste	Cabeceira	Lado sul	Atende 0,60
Casal padrão	1,38 × 1,88	0,65	0,62	1,32	sim
Viúva	1,28 × 1,88	0,65	0,62	1,42	sim
Queen — referência	1,58 × 1,98	0,60	0,57	1,12	no limite

ESCOPO — O QUE ENTRA AGORA E O QUE FICA PARA 2027/28

ID	Item	Fase
CT01	Trilho da cortina + perfil autoportante no trecho da claraboia	agora
CT02	Cortina de tecido, pé-direito inteiro — blackout a definir	agora
IN4	Eletroduto aparente e caixa de espera T18 junto à moldura	agora
IN5	Comando S10 com cabo guia até a espera	agora
MR1	Faixa de 0,12 m em volta do vidro reservada à moldura	agora
FC01	Fechamento elétrico da claraboia: moldura, motor e painel	2027/28
FC02	Ligação na espera T18 e programação do comando S10	2027/28

O trilho é reto e vira exatamente no fim da ponta da escada.

Recollida, a cortina fica o canto noroeste da sala de estar. Estendida, desce em linha reta rente à parede, sem desvio — passa por cima do degrau da ponta da escada —, faz a curva no fim da ponta e corre reta a 2,85 m da parede norte até a fachada. Ali a fachada é vidro (J02): a cortina encosta no caixilho; se a J02 tiver montante central, o trilho termina nele.

A cama fica no sentido leste-oeste, encostada na parede norte.

A lateral longa encosta na parede norte, que é cega (divisa); a cabeceira fica a leste. Sobram 0,65 m no pé, até a cortina, 0,62 m atrás da cabeceira (criado e acesso à J01) e 1,32 m do lado sul: os 0,60 m mínimos estão atendidos. A faixa sul inteira, de $3,15 \times 1,32$ m, é a área de troca de roupa. Viúva sobra mais; queen passa no limite.

Sob a claraboia o trilho não tem apoio no teto.

Entre 5,00 e 7,23 m são 2,23 m sem fixação — trilho comum pede apoio a cada ~1,0 m. Entra perfil autoportante (tubo metálico) fixado no concreto antes e depois da moldura, com o trilho preso nele; alternativa, cabo de aço tensionado. Confirmar com o fornecedor.

Fechamento elétrico: o equipamento é de 2027/28, a espera é de agora.

Com o teto aberto, eletroduto, caixa T18 e comando S10 com cabo guia custam pouco; depois da pintura custam abrir laje aparente e repintar. A moldura fixa na faixa de 0,12 m em volta do vidro — confirmar em estrutura se há viga de borda da piscina ali.

O que a cortina muda no resto do teto.

P01 passa a plafon, sobre a cama. AC01 sai da linha da cortina para 4,76 / 3,05 m: com a cortina fechada o quarto fica sem evaporadora própria. T16 e T19 são as tomadas das duas cabeceiras; S09 é paralelo da luz da sala de estar, no pilar entre J01 e J02.