


Opção A — cumaru-ferro com a cozinha em monolítico

Piso pronto em réguas nas áreas de estar e dormir; monolítico na cozinha de trabalho. Cores e desenho de régua ilustrativos.

norte 126° · Prancha 03 de 07

a ponta do monolítico nasce na quina do degrau, em curva

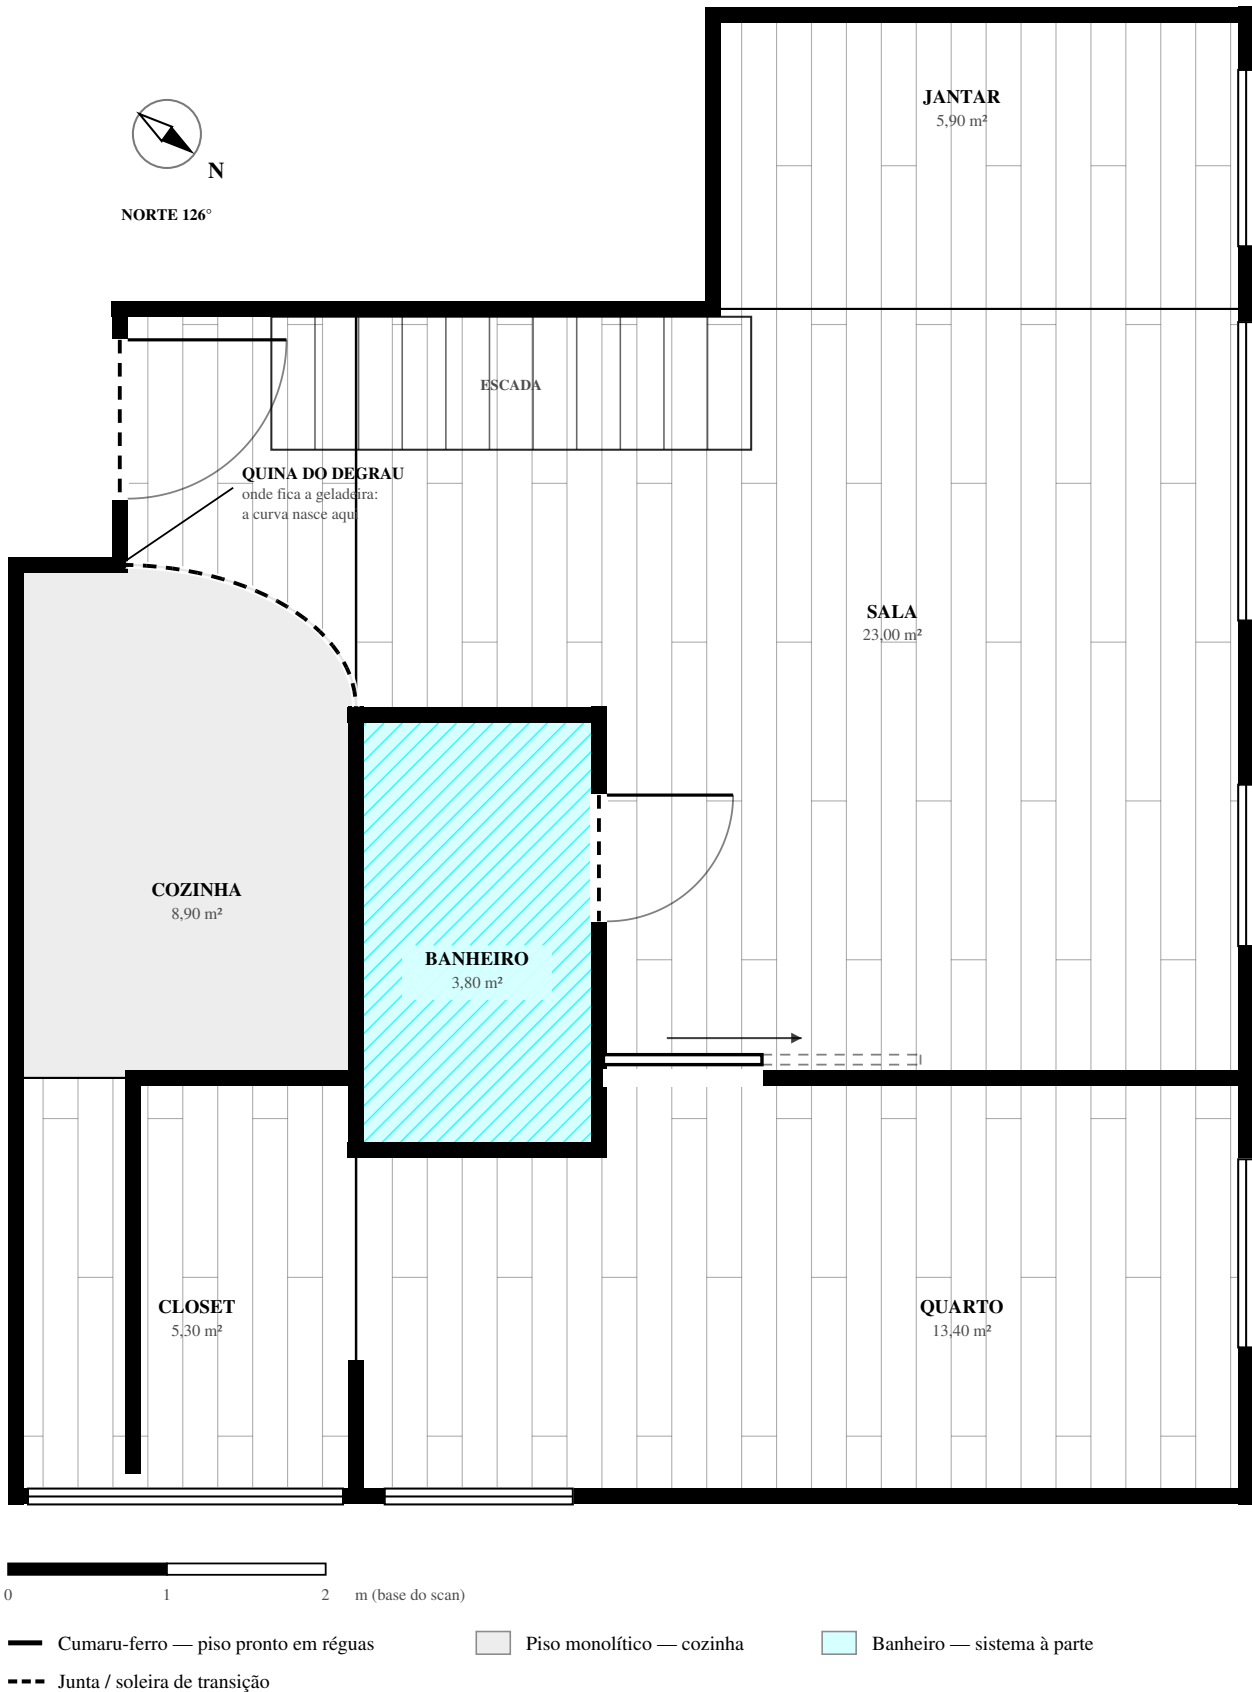

QUADRO DE ÁREAS

Sistema	Onde	Área
Cumaru-ferro	sala 23,00 + quarto 13,40 + jantar 5,90 + closet 5,30 + corredor 2,56	50,16 m²
+ reserva de 10%	cortes, perdas e reposição futura	55,18 m²
Monolítico	cozinha — 6,34 dos 8,90 m² do ambiente	6,34 m²
Banheiro	sistema à parte, área molhada, na mesma cota	3,80 m²
MainFloor	total do pavimento	60,30 m²

Dois materiais, e é a curva que resolve o encontro.

A ponta do monolítico nasce na quina do degrau da parede — logo abaixo da porta de entrada, onde fica a geladeira — e gira em arco de 1,49 × 0,89 m até a parede do banheiro. O corredor da entrada e a escada ficam em cumaru; a cozinha de trabalho fica em monolítico.

A junta curva é o detalhe mais caro desta opção.

Perfil de transição curvo, sob medida, com junta de movimentação. E as duas espessuras têm de ser niveladas no contrapiso para se encontrarem rentes: régua pronta com manta e monolítico somam alturas diferentes, e é no contrapiso que se acerta a diferença, não na soleira.

Cumaru-ferro é madeira densa — o que é virtude e é risco.

Dureza e resistência altas, e por isso mesmo muito sensível a umidade e a base torta. Exige contrapiso seco, plano e nivelado (P06), aclimação das régua no ambiente antes de assentar e folga de dilatação em todo o perímetro, escondida no rodapé. Piso pronto reduz obra, mas não dispensa nenhuma dessas três condições.

O desenho das régua é hipótese, não especificação.

Régua de 0,22 m correndo norte-sul, paralelas ao lado maior do pavimento, com topos a cada 3,00 m defasados de um terço. Largura, comprimento e sentido de assentamento são decisão de projeto: o sentido muda a leitura do espaço e a percepção do desnível do contrapiso.

O closet entrou em cumaru nesta opção.

Na proposta anterior ele ia em monolítico junto com a cozinha; como o pedido fala só da cozinha, o closet voltou para a madeira. Se preferir mantê-lo monolítico, o quadro muda para cumaru 44,86 m² e monolítico 11,64 m² — é uma linha de ajuste.

O banheiro fica fora dos dois sistemas, mas na mesma cota.

Sistema próprio, com impermeabilização, caimento e acabamento antiderrapante, nivelado com o piso seco (P05): a soleira é junta de material, não degrau. Sem degrau, ralo linear e fecho de vidro assumem a contenção de água.