


Elétrica

Força, comando e quadro. Iluminação na FO4 e ar-condicionado na FO5: aqui entram só as caixas de alimentação.

FO3 — ELÉTRICA

extraído do Caderno Alternativo A — REV. O

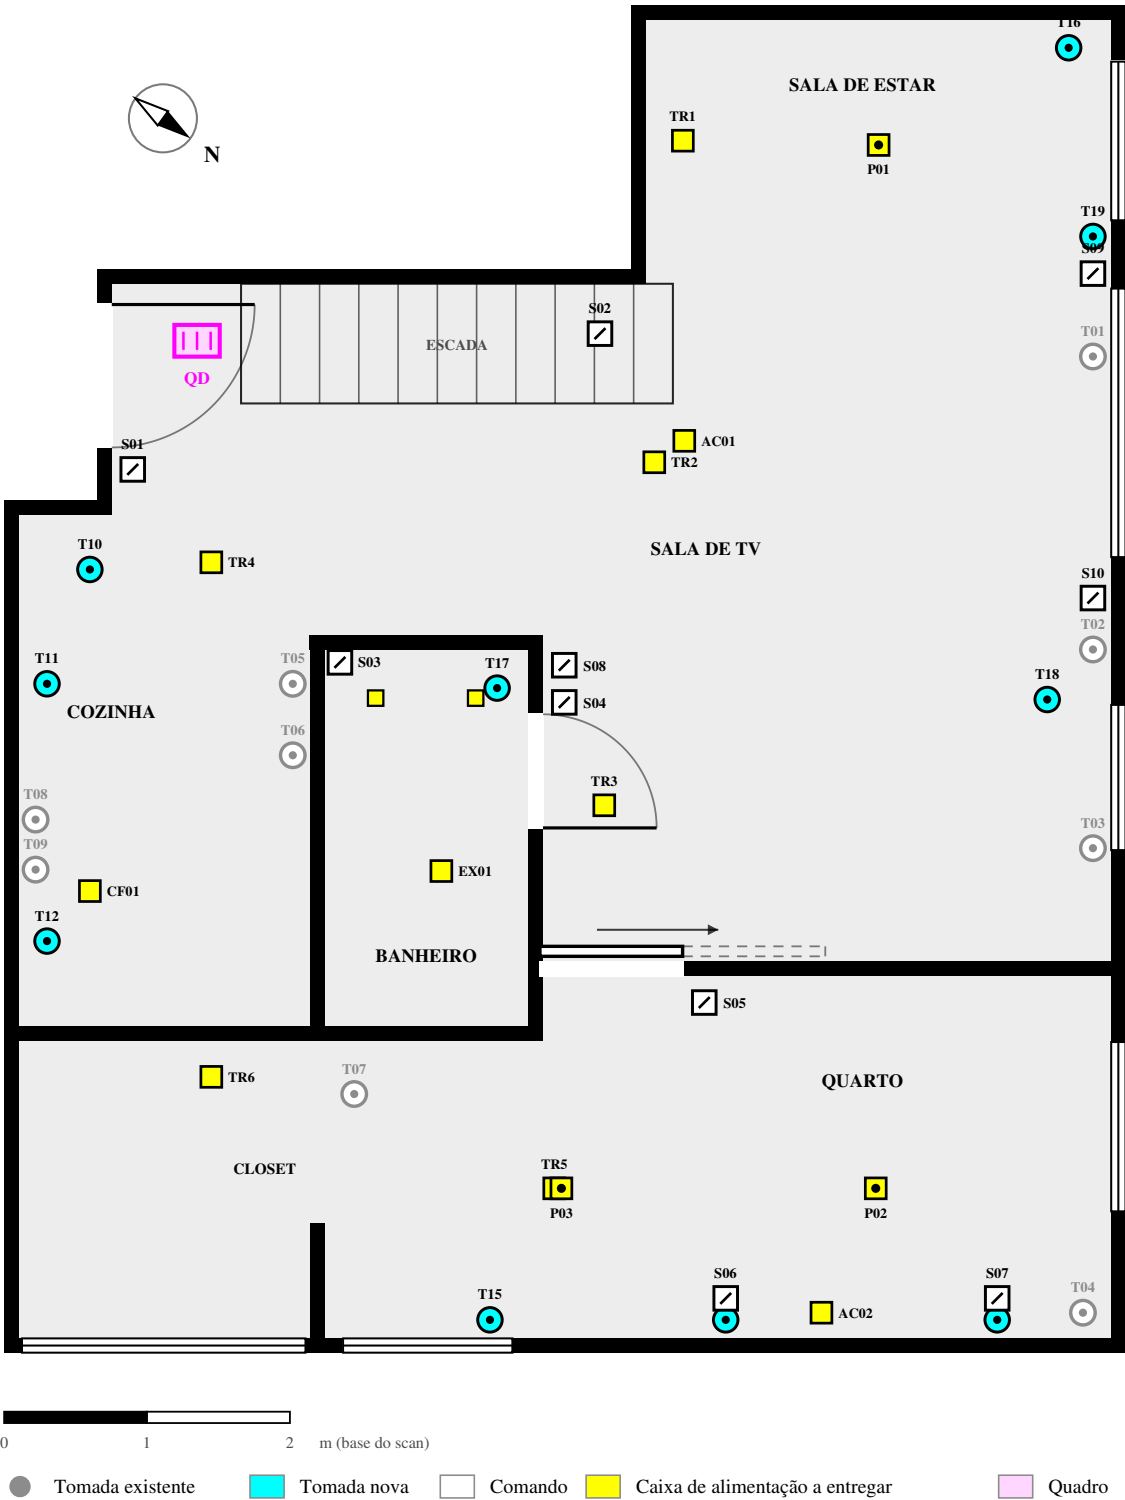

SEQUÊNCIA GERAL DA OBRA

|                      |             |                          |                  |                 |        |           |                           |
|----------------------|-------------|--------------------------|------------------|-----------------|--------|-----------|---------------------------|
| 1 Ensaios e proteção | 2 Demolição | 3 Preparo de superfícies | 4 Infraestrutura | 5 Reconstruções | 6 Piso | 7 Pintura | 8 Marcenaria e luminárias |
|----------------------|-------------|--------------------------|------------------|-----------------|--------|-----------|---------------------------|

ESCOPO — TAREFA E QUANTIDADE

| ID      | Tarefa                                                                       | Quantidade  |
|---------|------------------------------------------------------------------------------|-------------|
| QD      | Quadro de distribuição: avaliar, dimensionar e substituir                    | 1 conjunto  |
| T01–T09 | Tomadas existentes: conferir caixa, altura e circuito                        | 9 pontos    |
| T10–T19 | Tomadas novas, T18 é espera no teto                                          | 10 pontos   |
| S01–S10 | Comandos / interruptores, com paralelos na cabeceira                         | 10 pontos   |
| IN1     | Infraestrutura embutida em parede — antes de fechar a drywall R01            | 4,08 m      |
| IN2     | Infraestrutura aparente no teto: perfilado ou eletrocalha pintada            | a medir     |
| IN3     | Circuitos dedicados: geladeira, forno, cooktop, lava-louças, coifa           | 5 circuitos |
| AL1     | Alimentação de trilho no teto — entregar caixa (ver FO4)                     | 6 pontos    |
| AL2     | Alimentação de destaque — P02 e P03 no eixo do TR5 (ver FO4)                 | 3 pontos    |
| AL3     | Alimentação de embutido no forro do banheiro (ver FO4)                       | 2 pontos    |
| AL4     | Alimentação de evaporadora — entregar caixa (ver FO5)                        | 2 pontos    |
| AL5     | Alimentação de exaustor e de coifa (ver FO5)                                 | 2 pontos    |
| AL6     | Espera do motor da claraboia: caixa T18, eletroduto e guia até S10 (ver FO6) | 1 ponto     |
| PR      | Proteção: disjuntores, DR e DPS conforme projeto elétrico                    | 1 conjunto  |
| AT      | Aterramento e equipotencialização                                            | 1 conjunto  |
| EN      | Ensaio: continuidade, isolamento, DR e aterramento                           | 1 conjunto  |

ORDEM DE EXECUÇÃO

- 1 Levantamento e ensaio — E02.  
Identificar quadro, prumadas e circuitos existentes. Medir isolamento.
- 2 Estudo de demanda e projeto executivo.  
Diagrama unifilar, seções, proteção e quadro dimensionado antes de comprar material. Considerar 2 a 3 evaporadoras, forno, cooktop e lava-louças.
- 3 Marcação de pontos em obra.  
Conferir com marcenaria e mobiliário antes de abrir caixa. Faixa de 1,00 m a leste do vão da porta de correr é reservada: nada de caixa ali.
- 4 Infraestrutura embutida — IN1.  
Concluir antes de fechar a drywall R01.
- 5 Infraestrutura aparente no teto — IN2.  
Somente após o preparo da laje (P03), alinhada aos trilhos da FO4.
- 6 Descidas, caixas e passagem de cabos.  
Concluir antes do piso.
- 7 Entrega das alimentações — AL1 a AL6.  
Caixa no ponto, cabo passado e circuito identificado, para a iluminação (FO4), o ar (FO5) e a claraboia (FO6, 2027/28) instalarem sem abrir laje.
- 8 Quadro, proteção e aterramento — QD, PR e AT.
- 9 Ensaio — EN.  
Continuidade, isolamento, DR e aterramento, com laudo por escrito.
- 10 Ligação final e acabamento de placas.  
Somente após a pintura concluída.