


Demolição e desmontagem

Diagrama de escopo sobre o modelo de trabalho. Conferir os alvos presencialmente antes de mobilizar a demolidora.

sem forro: laje de concreto aparente

fundo do box é pano de vidro chão-teto

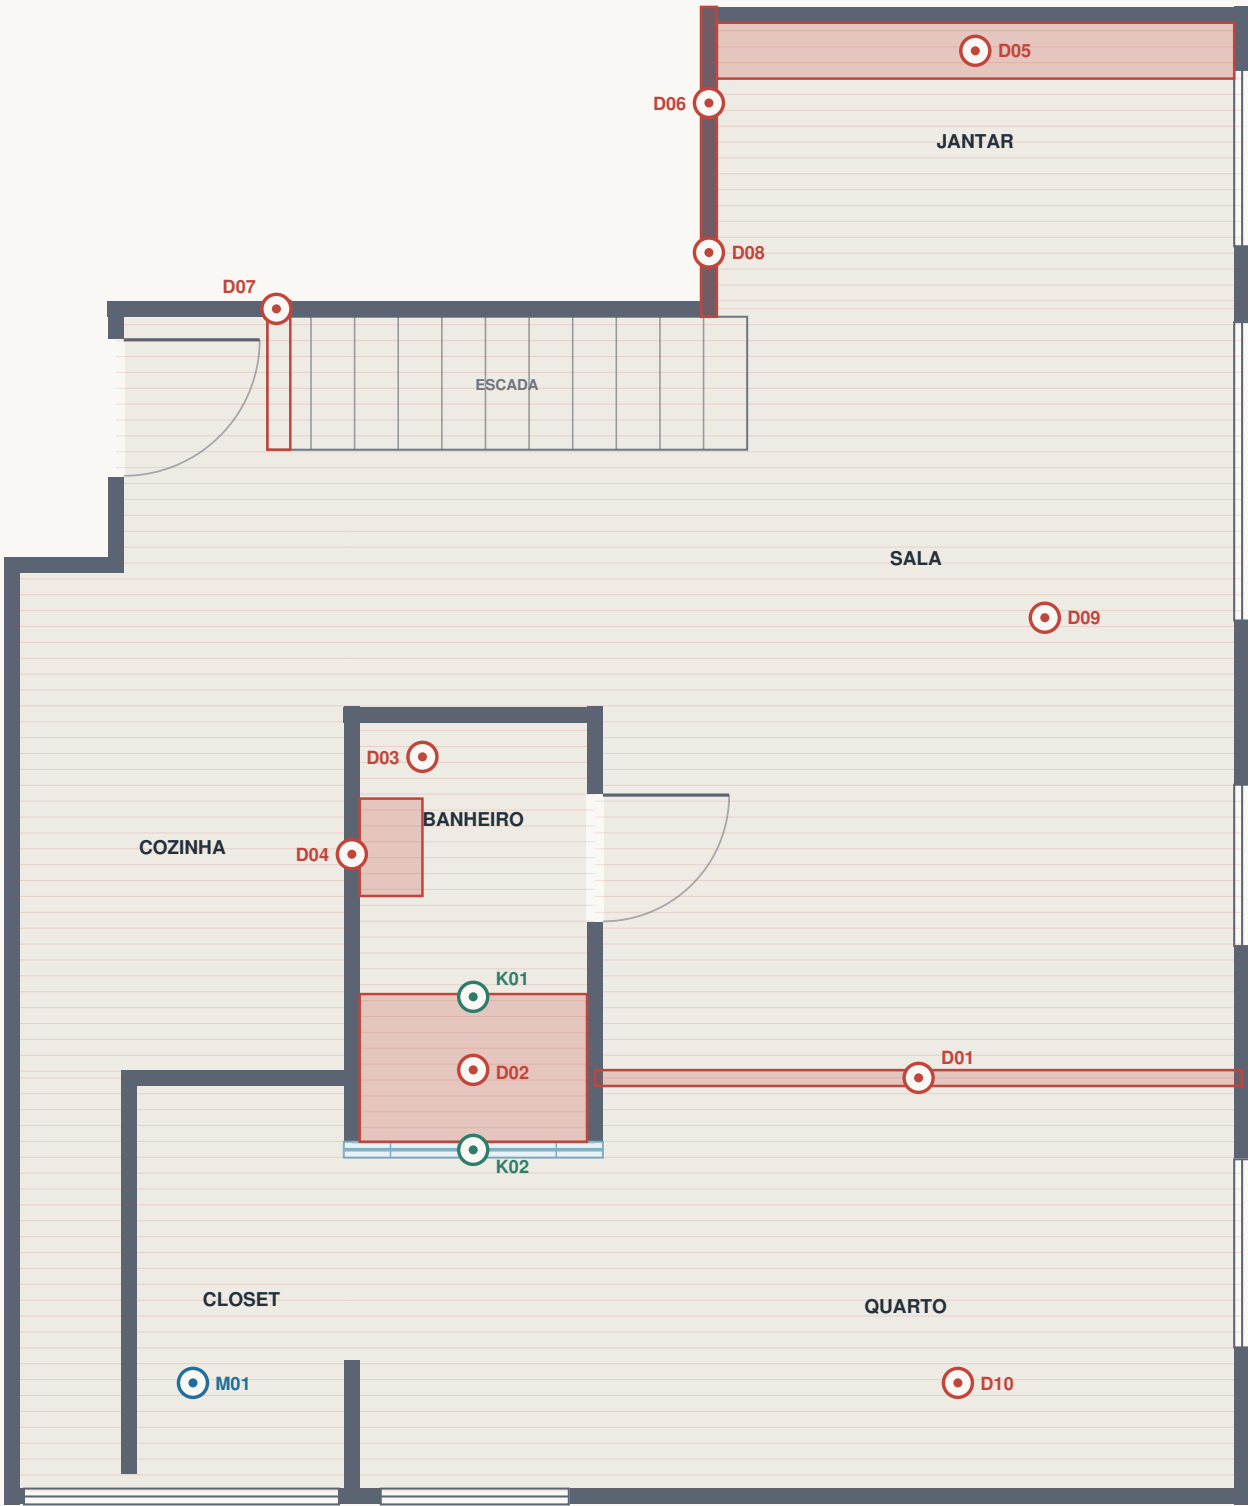

ESCOPO DE DEMOLIÇÃO E DESMONTAGEM

ID	Serviço	Quantidade preliminar
D01	Drywall entre sala e quarto	1 trecho — 4,08 m
D02	Box do banheiro: fechamento e base	1 conjunto — vidro preservado
D03	Piso do banheiro	3,80 m²
D04	Parede atrás do espelho e da bancada	1 trecho — 2,64 m a conferir
D05	Canto alemão do jantar	1 conjunto — inventário por módulo
D06	Espelho de parede do jantar	1 peça — não confundir com a fachada
D07	Parede da escada	trecho a confirmar em obra
D08	Parede entre a escada e o jantar	1 trecho — 1,95 m
D09	Forro: retirar 100%	60,30 m² menos a área marcada de 5,76 m²
D10	Retirar pisos do MainFloor	60,30 m² úteis, sem dupla contagem
M01	Desmontar e remontar closet	1 conjunto — inventário por módulo
K01	Vidro do box — MANTER	1 peça
K02	Pano de vidro chão-teto do box — MANTER	1,63 m, ponta a ponta

Sem forro. O teto do MainFloor passa a ser a laje de concreto aparente:
a retirada do forro é total, não parcial. Só o banheiro admite forro, para abrigar a exaustão e a luminária embutida. Toda a iluminação e o ar-condicionado dos demais ambientes serão aplicados na laje — ver Prancha 04.

O fundo do box não é parede: é um pano de vidro chão-teto, ponta a ponta.
O scan leu esse pano como vão. A correção vale para todas as pranchas do caderno. O vidro permanece; o que sai é o fechamento do box, o revestimento e o piso.

Drywall: não somar as duas faces como área de parede demolida.
Aberturas, montantes, instalações internas e encontros exigem conferência. O desenho marca apenas o trecho entre sala e quarto.

Closet: etiquetar módulos e ferragens, fotografar, acondicionar e proteger.
A área de 5,30 m² é do ambiente, não é área de marcenaria.

Escada: dois alvos distintos.
A parede entre a escada e o jantar (D08) está identificada no scan. A parede da escada (D07) precisa ser apontada presencialmente antes de entrar em orçamento.

Quantidades preliminares sobre o modelo do scan (02.09.2026): servem para orientar visita e proposta, não para fechar medição. Nenhum alvo foi verificado em campo. Instalações embutidas, estrutura e vedações devem ser identificadas antes do início dos serviços.

Cumaru ou monolítico

Comparação gráfica em planta. Cores ilustrativas; nenhum produto ou espessura está especificado.


ponta da cozinha em curva na quina da porta

fundo do box em vidro chão-teto · drywall sala/quarto retirada

- Cumaru em réguas
- Piso monolítico
- Banheiro — sistema à parte (área molhada)
- Junta / soleira de transição
- Drywall retirada

A / Cumaru nas áreas secas

cozinha e closet em monolítico

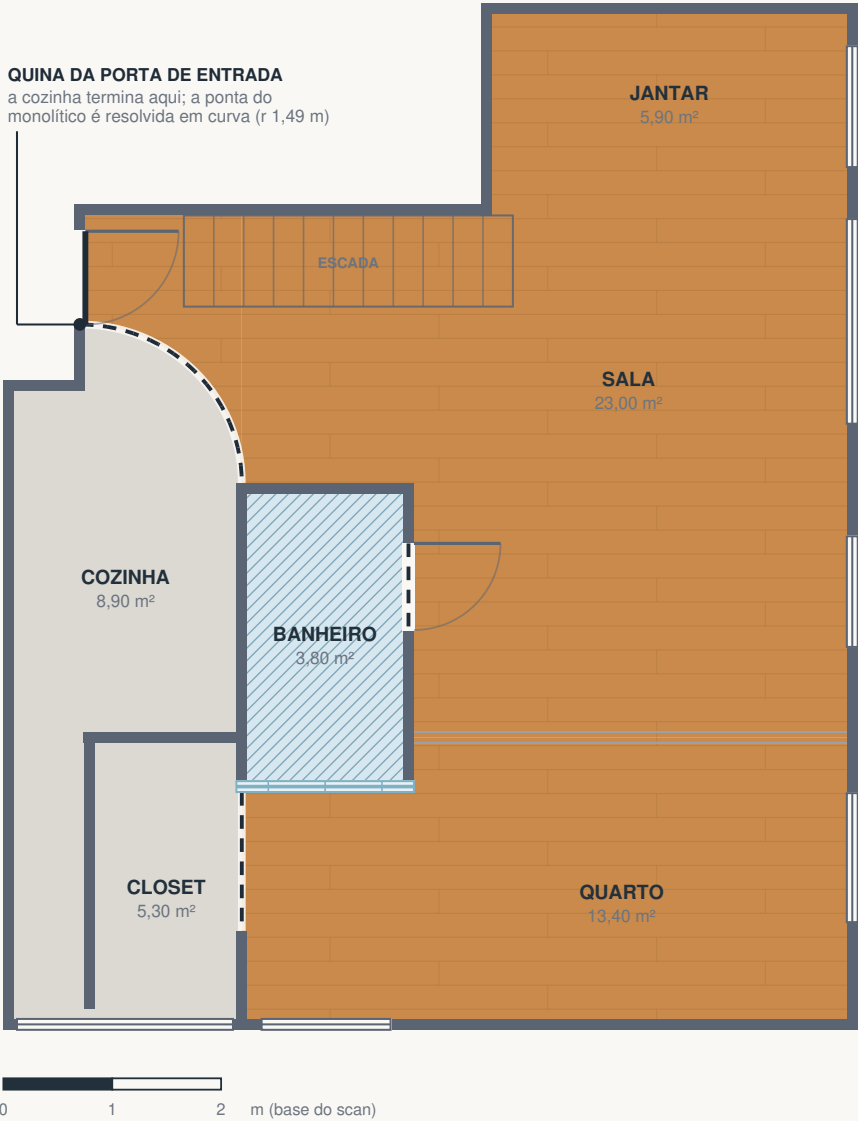


QUADRO DE ÁREAS (m²)		
Cumaru	sala 23,00 + quarto 13,40 + jantar 5,90 + hall 1,94	44,24
+ reserva 10%	cortes, perdas e reposição futura	48,66
Monolítico	cozinha 6,96 (de 8,90) + closet 5,30	12,26
Banheiro	sistema à parte (área molhada)	3,80
TOTAL DO PAVIMENTO		60,30

A cozinha sobe pela extensão e para na quina da porta de entrada: a ponta do monolítico gira em curva (raio 1,49 m) até a parede do banheiro. O hall da entrada e a escada — 1,94 m² que o scan conta como cozinha — ficam em cumaru, por isso a cozinha entra no quadro com 6,96 m². Cumaru: 44,24 m² líquidos; 48,66 m² com reserva de 10%.

B / Monolítico no MainFloor

banheiro em sistema à parte

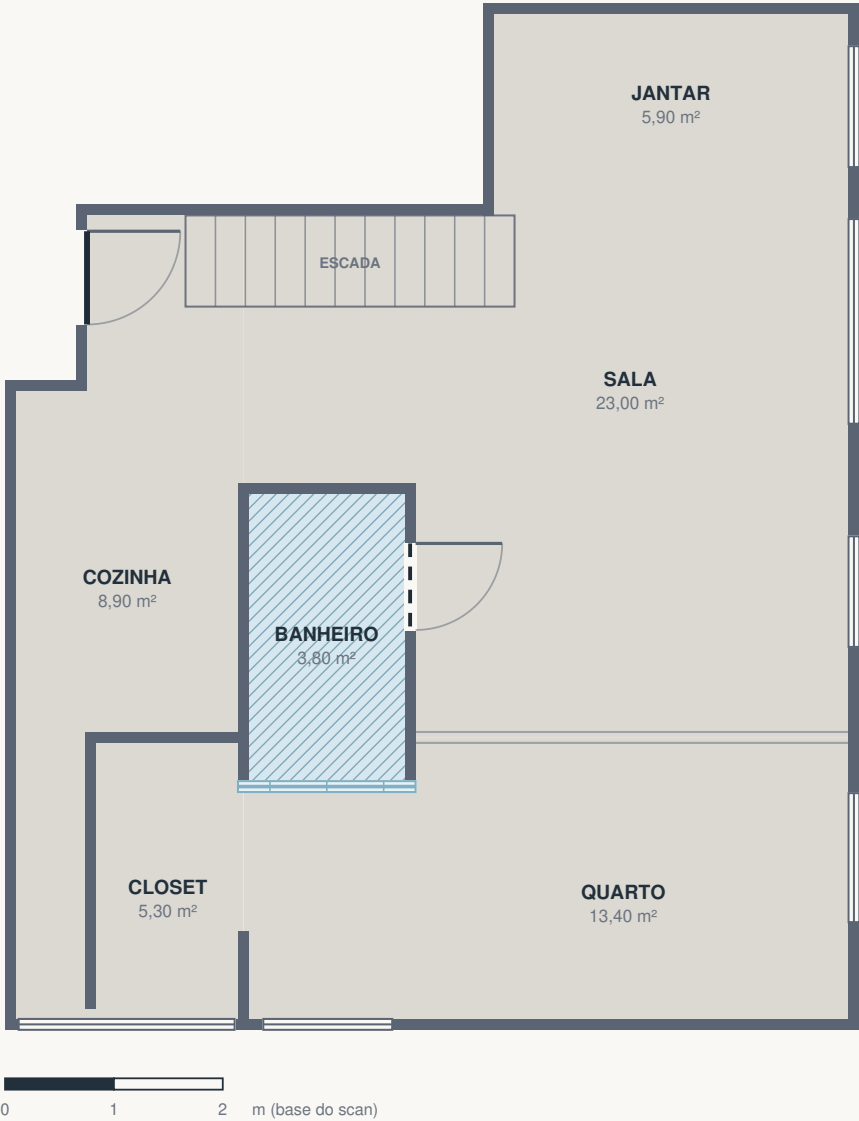

QUADRO DE ÁREAS (m²)		
Monolítico	sala, jantar, quarto, cozinha e closet	56,50
Banheiro	sistema à parte (área molhada)	3,80
Sem reserva	aplicação moldada in loco, sem perda de corte	—
TOTAL DO PAVIMENTO		60,30

Monolítico contínuo em 56,50 m² de base horizontal (60,30 m² do pavimento menos os 3,80 m² do banheiro) — sem junta de material entre os ambientes secos. Degraus excluídos; o piso acessível sob a escada permanece. Juntas de dilatação a definir no executivo. No banheiro, especificar sistema com impermeabilização e acabamento antiderrapante.


Revestimento contínuo: toda a área de piso é revestida, inclusive sob móveis e equipamentos — nenhum recorte de mobiliário foi descontado. O fundo do box é um pano de vidro chão-teto, ponta a ponta. Drywall entre sala e quarto retirada (indicada em fantasma): some ~0,40 m² de piso na faixa da parede, a conferir em obra. Áreas conforme o scan de 02.09.2026.

Teto: laje aparente, iluminação e ar-condicionado

Distribuição conceitual sobre a laje de concreto. Reservas de posição, não quantidade final de luminárias nem de equipamentos.

sem forro — tudo aplicado na laje

exceção: banheiro mantém forro

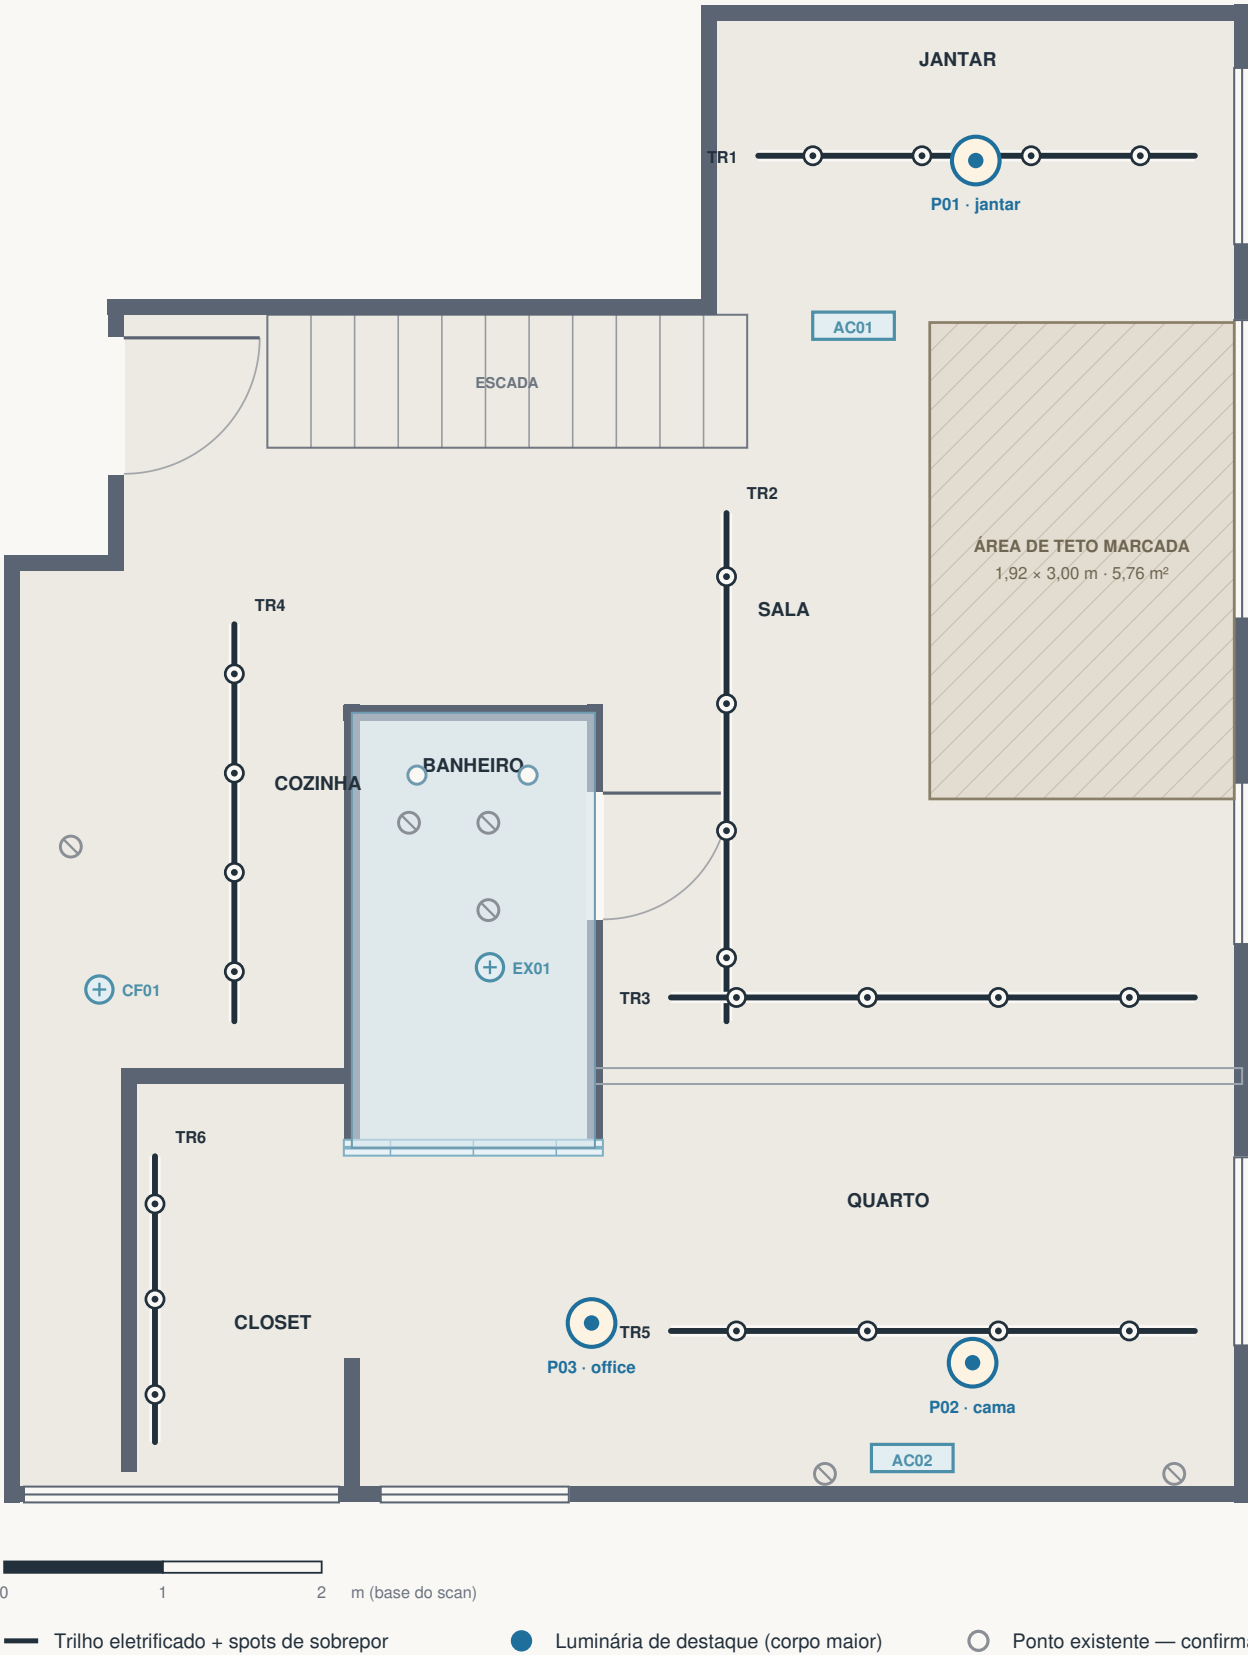

ILUMINAÇÃO POR AMBIENTE

Ambiente	Alvo geral	Fluxo inicial	Temperatura de cor
Sala	150 lux	7.188 lm	2.700 K
Quarto	150 lux	4.188 lm	2.700 K
Cozinha	300 lux	5.563 lm	3.000 K
Jantar	150 lux	1.844 lm	2.700 K
Closet	200 lux	2.208 lm	3.000 K
Banheiro	200 lux	1.583 lm	3.000 K

AR-CONDICIONADO — REGRA SIMPLIFICADA 600/800 BTU/h POR m²

Zona	Área	Base sombra	Base sol
Social + cozinha	37,80 m²	22.680 BTU/h	30.240 BTU/h
Quarto + closet	18,70 m²	11.220 BTU/h	14.960 BTU/h
Total sem banheiro	56,50 m²	33.900 BTU/h	45.200 BTU/h

Não há forro: a laje de concreto é o teto acabado.

Toda a iluminação passa a ser aplicada — trilhos eletrificados, spots de sobrepor e pendentes. Nada de embutido fora do banheiro, único ambiente que mantém forro para abrigar a exaustão e a luminária do box.

Fiação e infraestrutura ficam à vista.

Prever perfilados, eletrocalhas ou canaletas pintadas, alinhados às vigas e aos trilhos. O caminho da fiação vira projeto de desenho, não sobra de obra: definir antes de furar a laje.

P01, P02 e P03 são as três luminárias de destaque pedidas pelo cliente

— jantar, cama e office. Corpo e diâmetro maiores que os spots dos trilhos, em pendente ou plafon de sobrepor. As demais posições são reserva de estudo, não quantidade final.

Ar-condicionado sem forro: não há plenum para dutar.

Trabalhar com evaporadoras hi-wall ou cassete aparente. Tubulação frigorígena, dreno e interligação elétrica correm aparentes, em calha, com caimento contínuo do dreno. Somente Electrolux; marca igual não garante compatibilidade entre unidades.

A área de teto marcada (1,92 x 3,00 m = 5,76 m²) condiciona a modulação.

Nem luminária, nem trilho, nem evaporadora ou tubulação podem invadi-la. Os trilhos foram posicionados fora dela: TR1 ao norte, TR2 a oeste e TR3 ao sul.

A reserva AC01 do estudo anterior caía dentro da área marcada.

Foi deslocada para oeste, mantendo a insuflação para sala e jantar. A posição definitiva depende de confirmar apoio acima do limite sala/jantar e o modelo da condensadora existente: não assumir que ela admite duas evaporadoras.

Comandos: cenas geral / tarefa / noturna, com acionamento no acesso de cada ambiente.

Trilho permite remanejar spots depois — o comando é que precisa estar certo desde já. Priorizar boa reprodução de cores no espelho e no closet.

Vazões de referência, a validar com perda de carga do duto:

banheiro 3,8 x 2,62 x 10 = 99,56 m³/h; coifa 8,9 x 2,62 x 12 = 279,82 m³/h — este último valeria só se a cozinha fosse isolada. Cozinha integrada exige seleção por captura no fogão. Coifa e exaustão do banheiro precisam de rotas e descargas próprias; não interligar.


Fluxo = área x lux ÷ (0,60 x 0,80). Fatores de utilização e manutenção são hipóteses; a laje aparente escura reduz o fator de utilização e deve ser reavaliada. Carga térmica não é carga final: claraboia, insolação, escada aberta e ocupação mudam o resultado. Estudar 2 ou 3 evaporadoras; não há número fechado de aparelhos.

Tomadas, comandos e quadro

Reservas de localização, sem circuitos executivos. Posições existentes conforme marcação do cliente sobre o estudo anterior.

quadro junto à porta de entrada

trajetos aparentes: não há forro

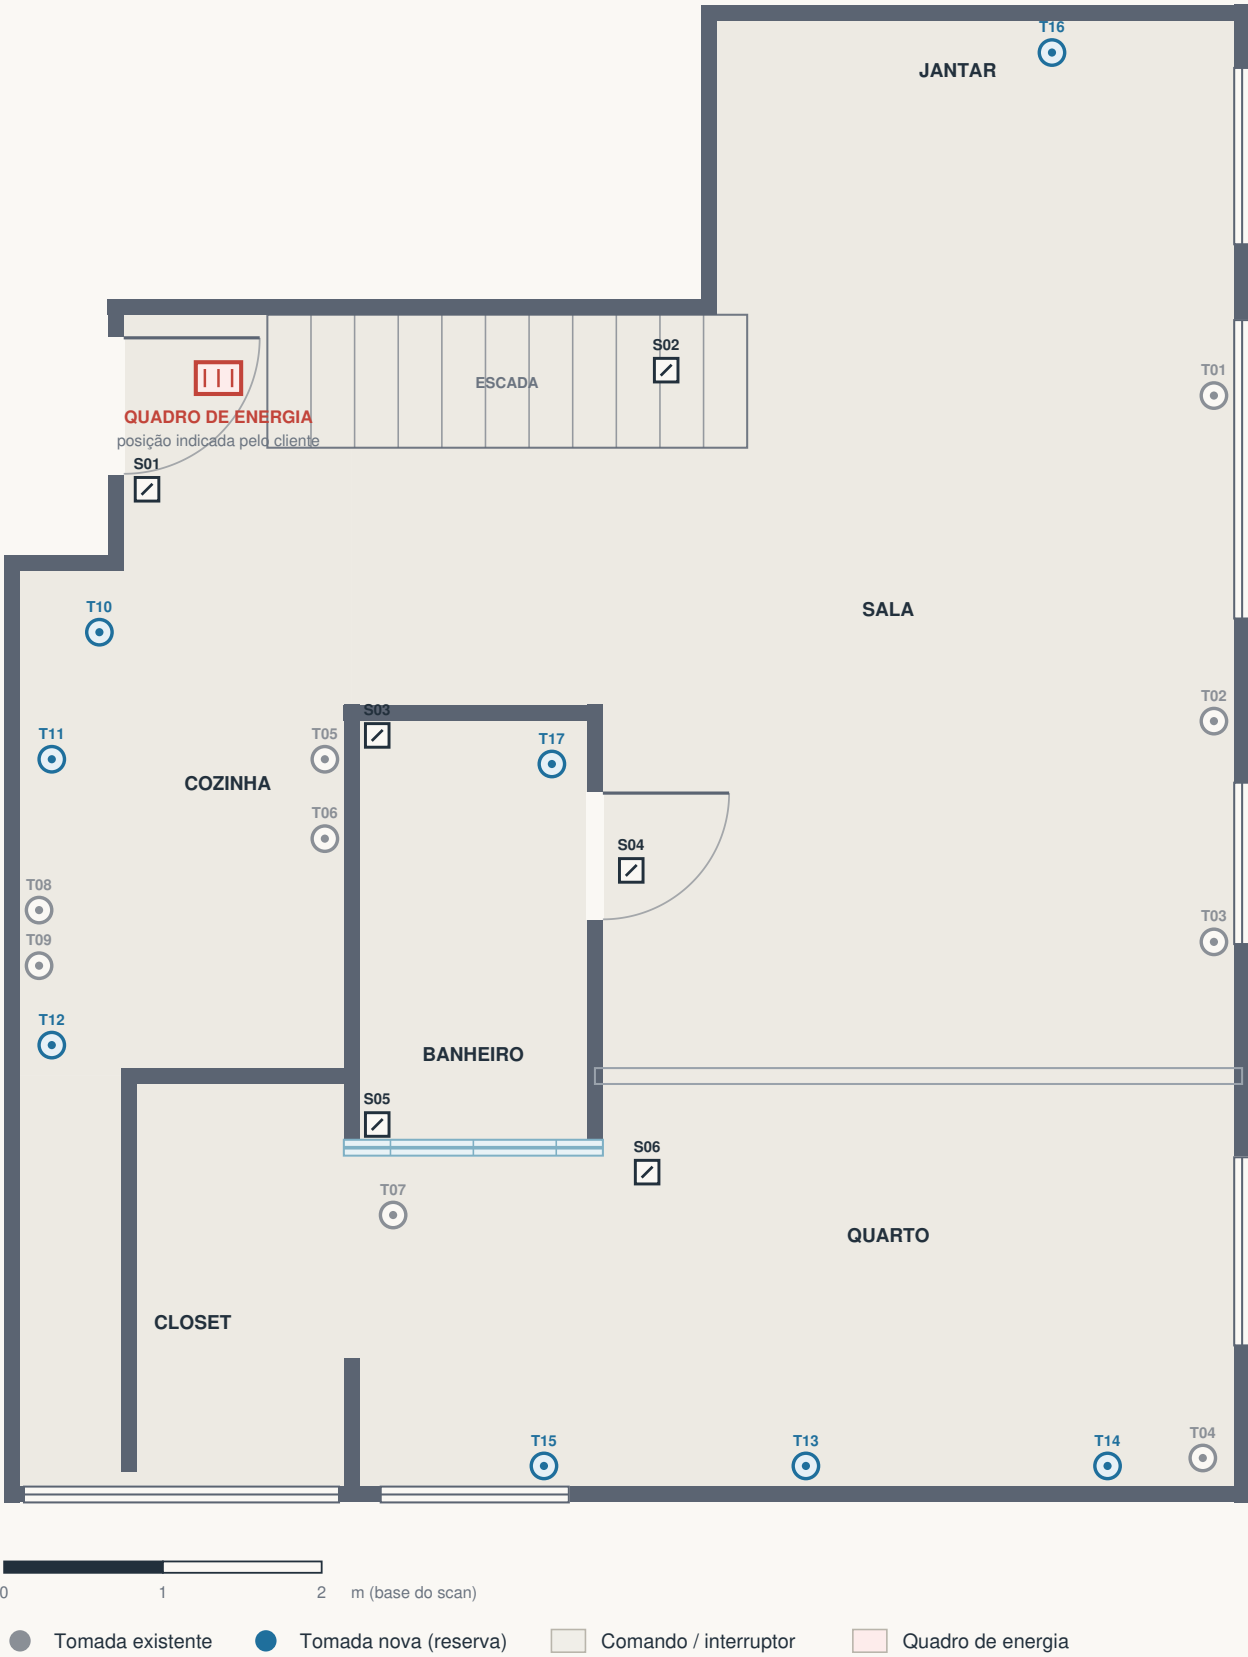

RESERVAS DE INFRAESTRUTURA ELÉTRICA

Grupo	Reservas	Revisão necessária
Quadro elétrico	junto à porta de entrada, na extensão da cozinha	tensão, fases, demanda, proteção e espaços
Tomadas existentes	9 posições levantadas pelo cliente	confirmar altura, caixa e circuito
Tomadas novas	8 reservas — T10 a T17	não é número normativo nem total final
Comandos	6 posições de acesso — S01 a S06	lado da porta, marcenaria e cenas
Cozinha	geladeira, forno, lava-louças, coifa e bancada	pontos dedicados, circuito exclusivo
Ar-condicionado	alimentação conforme manual da unidade	quem alimenta varia com o sistema
Banheiro	ponto junto ao lavatório a validar	volumes de proteção, DR e cargas

O quadro de energia foi localizado pelo cliente: fica junto à porta de entrada, no início da extensão da cozinha. Confirmar espaço livre, altura e a circulação da porta antes de fixar. Todo o resto do traçado sai dele.

Sem forro, os trajetos ficam aparentes. A distribuição no teto passa a ser perfilado ou eletrocalha pintada, acompanhando os trilhos de luz da Prancha 04; as descidas para tomadas e comandos correm embutidas na parede. Isso vira desenho: definir caminhos e separações antes de medir eletrodutos e cabos.

Alturas de intenção, sempre conferidas com mobiliário e acabamento: tomadas gerais 0,30 m; comandos 1,10 m; pontos de bancada em torno de 1,15 m. As marcações não autorizam instalação em parede sem localizar estrutura e tubulações.

Os pontos T01 a T09 são os existentes que você marcou em planta. Estão desenhados na posição aproximada do levantamento: servem para decidir o que se aproveita e o que se remaneja, não para medir. T10 a T17 são reservas novas do estudo.

Circuitos, seções, disjuntores, aterramento, DR, demanda e proteção contra surtos ficam a cargo do projeto elétrico após o levantamento. Não usar estas reservas como projeto para o eletricista executar.