


Teto: laje aparente, iluminação e ar-condicionado

Distribuição conceitual sobre a laje de concreto. Reservas de posição, não quantidade final de luminárias nem de equipamentos.

sem forro — tudo aplicado na laje

exceção: banheiro mantém forro

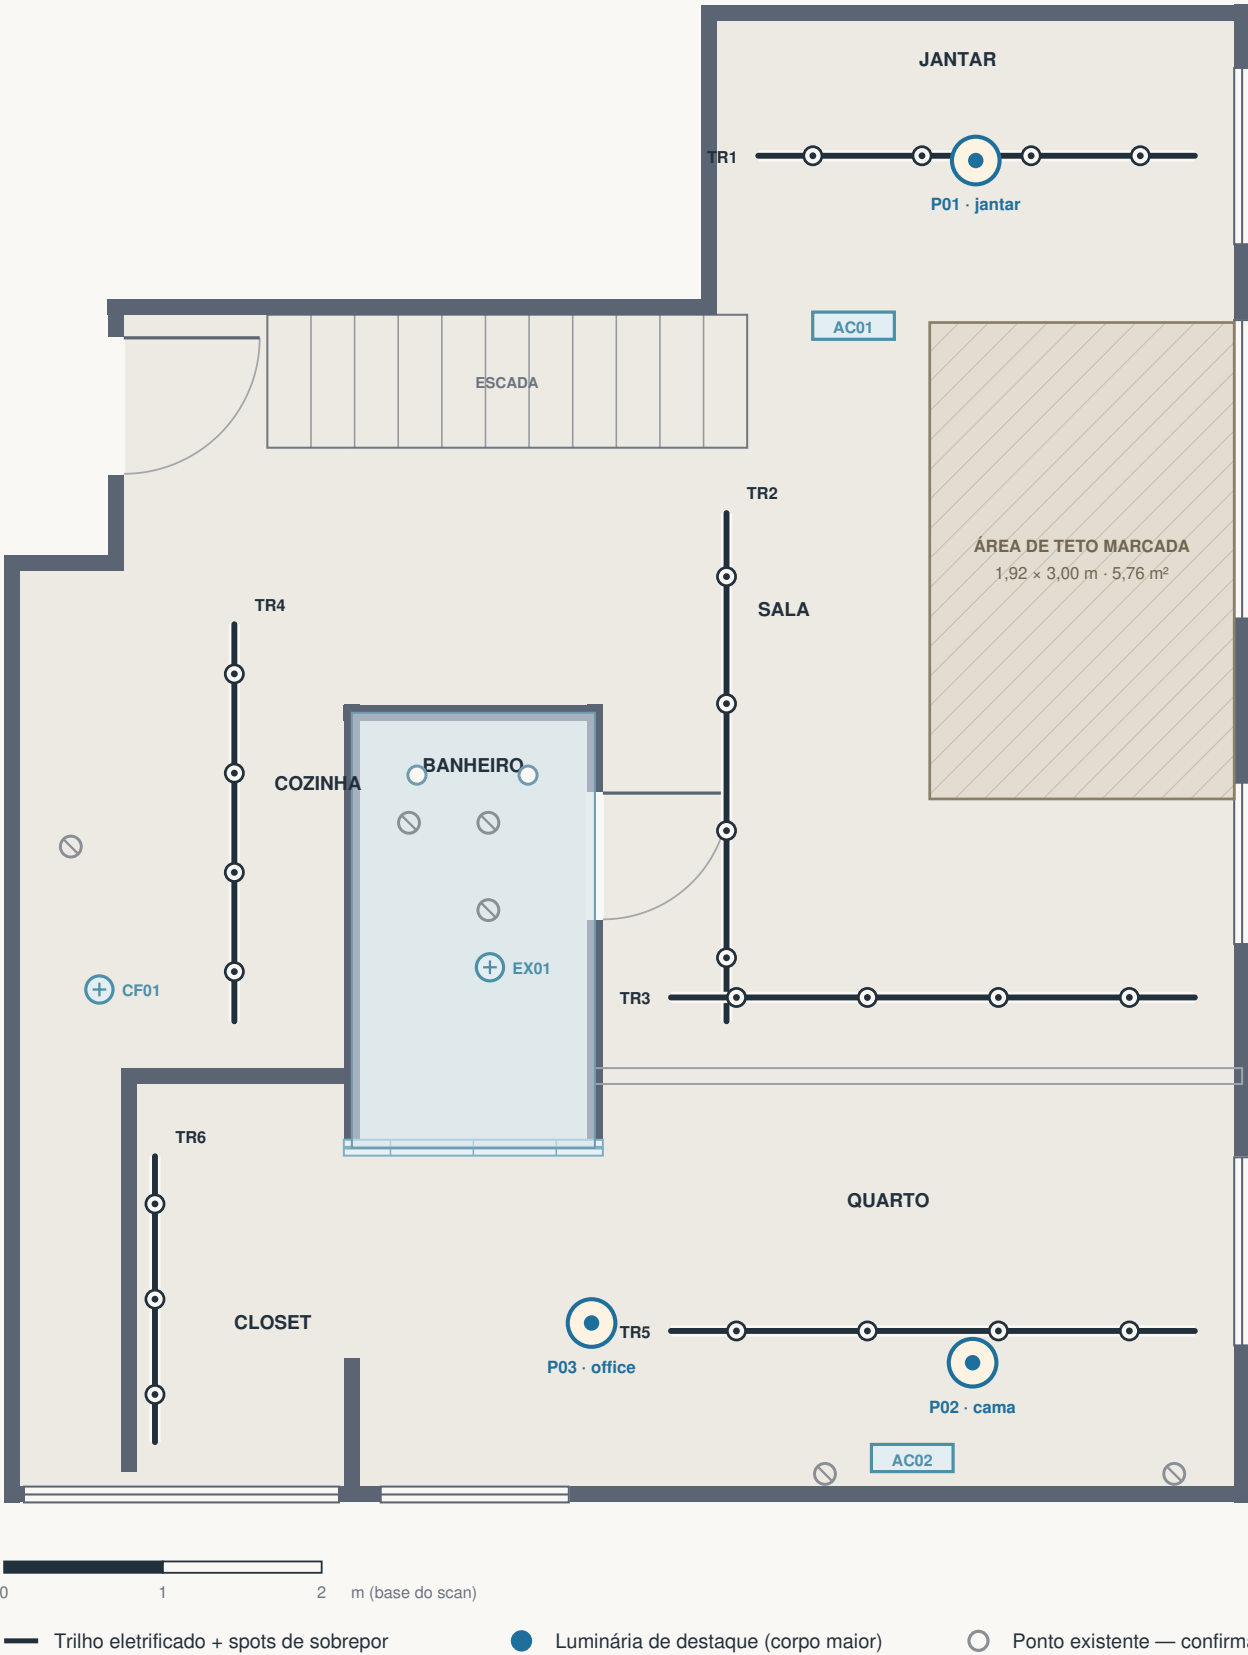

ILUMINAÇÃO POR AMBIENTE

Ambiente	Alvo geral	Fluxo inicial	Temperatura de cor
Sala	150 lux	7.188 lm	2.700 K
Quarto	150 lux	4.188 lm	2.700 K
Cozinha	300 lux	5.563 lm	3.000 K
Jantar	150 lux	1.844 lm	2.700 K
Closet	200 lux	2.208 lm	3.000 K
Banheiro	200 lux	1.583 lm	3.000 K

AR-CONDICIONADO — REGRA SIMPLIFICADA 600/800 BTU/h POR m²

Zona	Área	Base sombra	Base sol
Social + cozinha	37,80 m²	22.680 BTU/h	30.240 BTU/h
Quarto + closet	18,70 m²	11.220 BTU/h	14.960 BTU/h
Total sem banheiro	56,50 m²	33.900 BTU/h	45.200 BTU/h

Não há forro: a laje de concreto é o teto acabado.

Toda a iluminação passa a ser aplicada — trilhos eletrificados, spots de sobrepor e pendentes. Nada de embutido fora do banheiro, único ambiente que mantém forro para abrigar a exaustão e a luminária do box.

Fiação e infraestrutura ficam à vista.

Prever perfilados, eletrocalhas ou canaletas pintadas, alinhados às vigas e aos trilhos. O caminho da fiação vira projeto de desenho, não sobra de obra: definir antes de furar a laje.

P01, P02 e P03 são as três luminárias de destaque pedidas pelo cliente

— jantar, cama e office. Corpo e diâmetro maiores que os spots dos trilhos, em pendente ou plafon de sobrepor. As demais posições são reserva de estudo, não quantidade final.

Ar-condicionado sem forro: não há plenum para dutar.

Trabalhar com evaporadoras hi-wall ou cassete aparente. Tubulação frigorígena, dreno e interligação elétrica correm aparentes, em calha, com caimento contínuo do dreno. Somente Electrolux; marca igual não garante compatibilidade entre unidades.

A área de teto marcada (1,92 × 3,00 m = 5,76 m²) condiciona a modulação.

Nem luminária, nem trilho, nem evaporadora ou tubulação podem invadi-la. Os trilhos foram posicionados fora dela: TR1 ao norte, TR2 a oeste e TR3 ao sul.

A reserva AC01 do estudo anterior caía dentro da área marcada.

Foi deslocada para oeste, mantendo a insuflação para sala e jantar. A posição definitiva depende de confirmar apoio acima do limite sala/jantar e o modelo da condensadora existente: não assumir que ela admite duas evaporadoras.

Comandos: cenas geral / tarefa / noturna, com acionamento no acesso de cada ambiente.

Trilho permite remanejar spots depois — o comando é que precisa estar certo desde já. Priorizar boa reprodução de cores no espelho e no closet.

Vazões de referência, a validar com perda de carga do duto:

banheiro 3,8 × 2,62 × 10 = 99,56 m³/h; coifa 8,9 × 2,62 × 12 = 279,82 m³/h — este último valeria só se a cozinha fosse isolada. Cozinha integrada exige seleção por captura no fogão. Coifa e exaustão do banheiro precisam de rotas e descargas próprias; não interligar.