


Planta proposta cotada

MainFloor completo, com a parede cozinha/closet na posição nova. Demais ambientes sem alteração.

cozinha 9,82 m² · closet 4,38 m²

mesma base do scan — REV. M

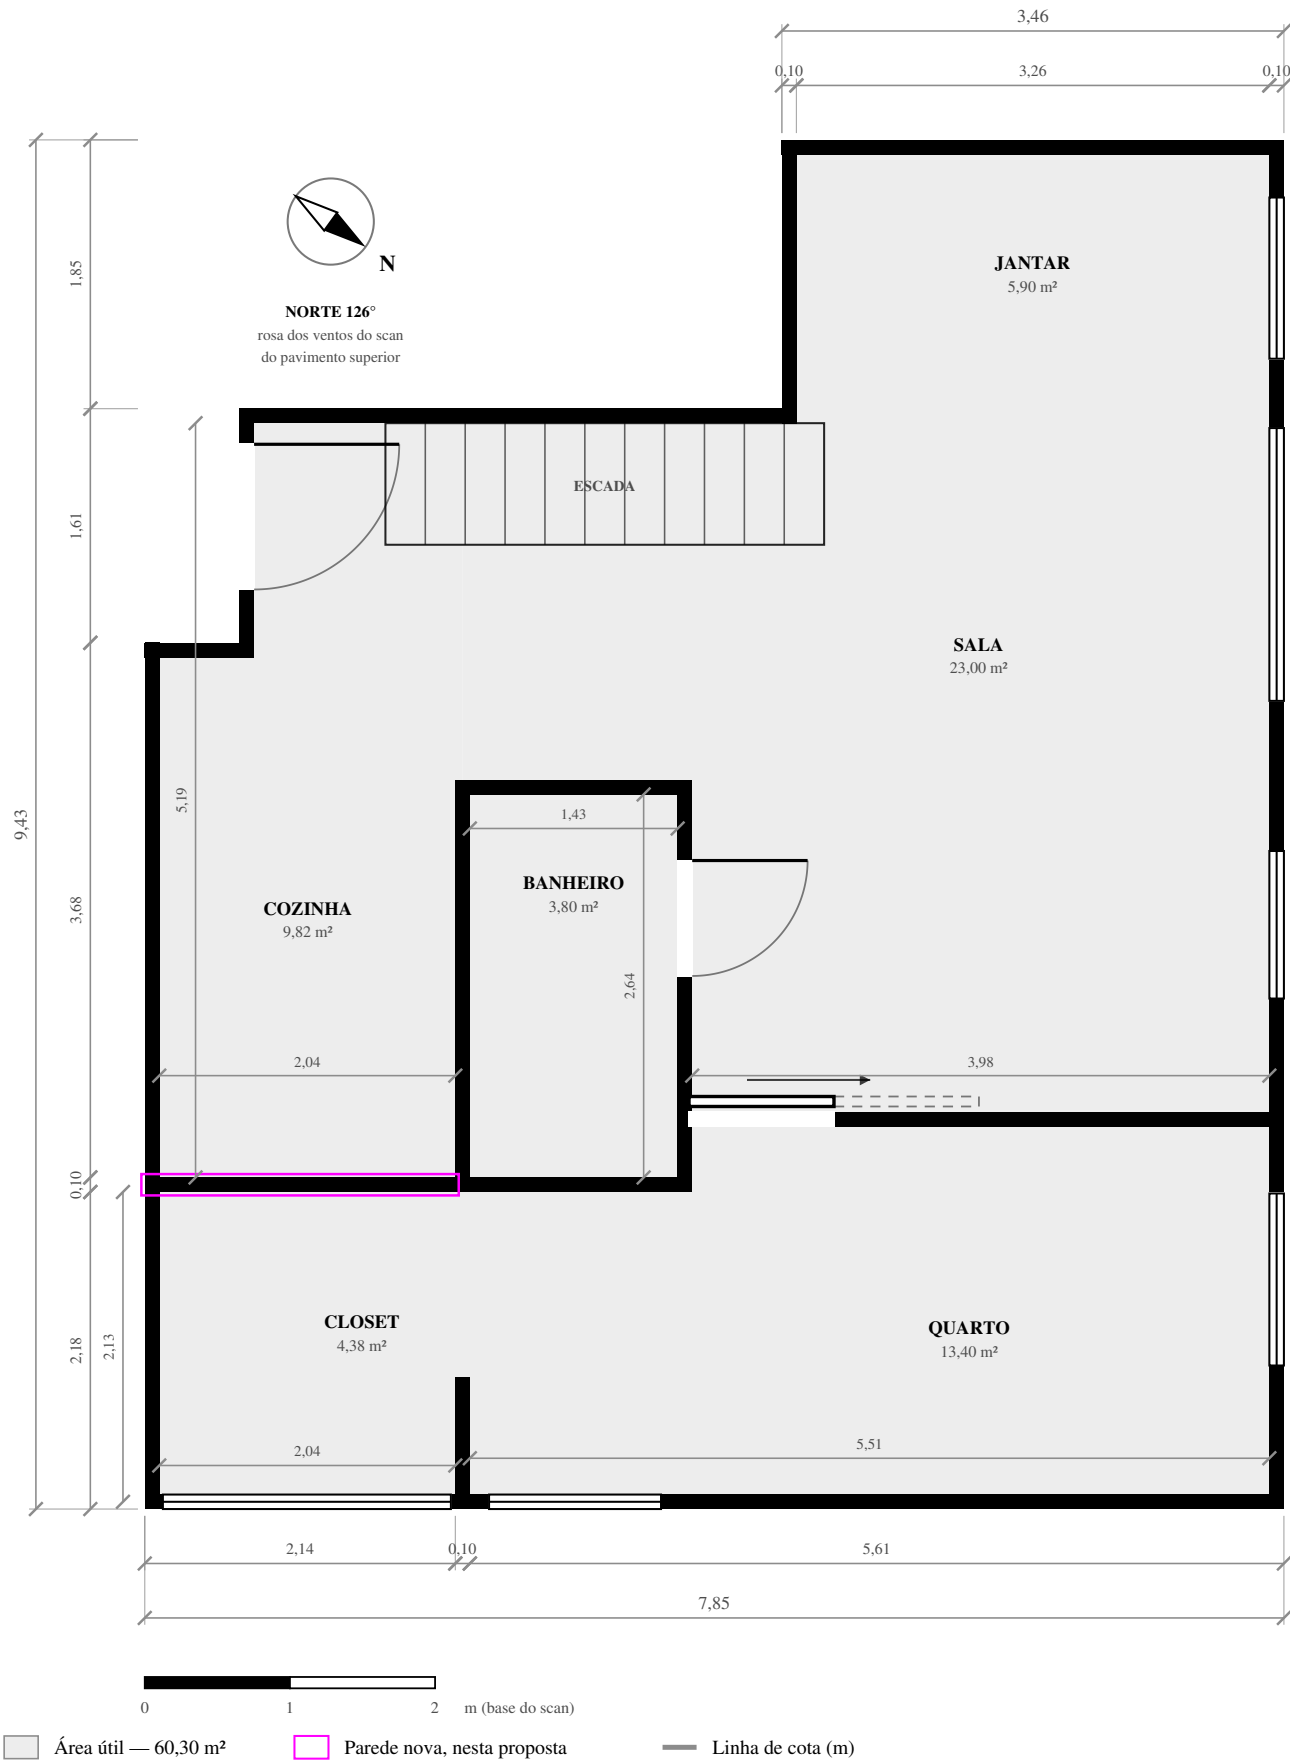

COMPARATIVO DE ÁREAS

Ambiente	Área atual	Área nesta proposta	Diferença
Cozinha	8,90 m²	9,82 m²	+0,92 m²
Closet	5,30 m²	4,38 m²	−0,92 m²
Soma das duas	14,20 m²	14,20 m²	sem variação
MainFloor — total	60,30 m²	60,30 m²	sem variação

Só duas salas mudam de área.

Sala, quarto, jantar e banheiro seguem exatamente como na REV. M — mesmas cotas, mesmas esquadrias, mesma numeração de portas e janelas.

A largura interna comum não muda.

Cozinha e closet continuam com 2,04 m de largura livre — a mesma parede externa oeste e a mesma parede do banheiro/quarto os limitam dos dois lados. Só a parede que os separa entre si é que se move.

J06, a janela do closet, não é afetada.

Fica na parede sul (fachada), que esta alteração não toca. A profundidade do closet diminui pelo lado norte — o vão da janela permanece o mesmo.

Cotas extraídas do modelo do scan e arredondadas ao centímetro, com a parede cozinha/closet na posição desta proposta. Planta de estudo. Substituí a Prancha 01 apenas nesta proposta alternativa — a REV. M segue como está.