Opção B — porcelanato acetinado no banheiro, cozinha e closet

norte 126° · Prancha 04 de 14

Porcelanato acetinado no banheiro e box e na zona cozinha + closet; monolítico nas áreas de estar e dormir. Cores e paginação ilustrativas.

ponta arredondada: canto reto com filete de 0,70 m

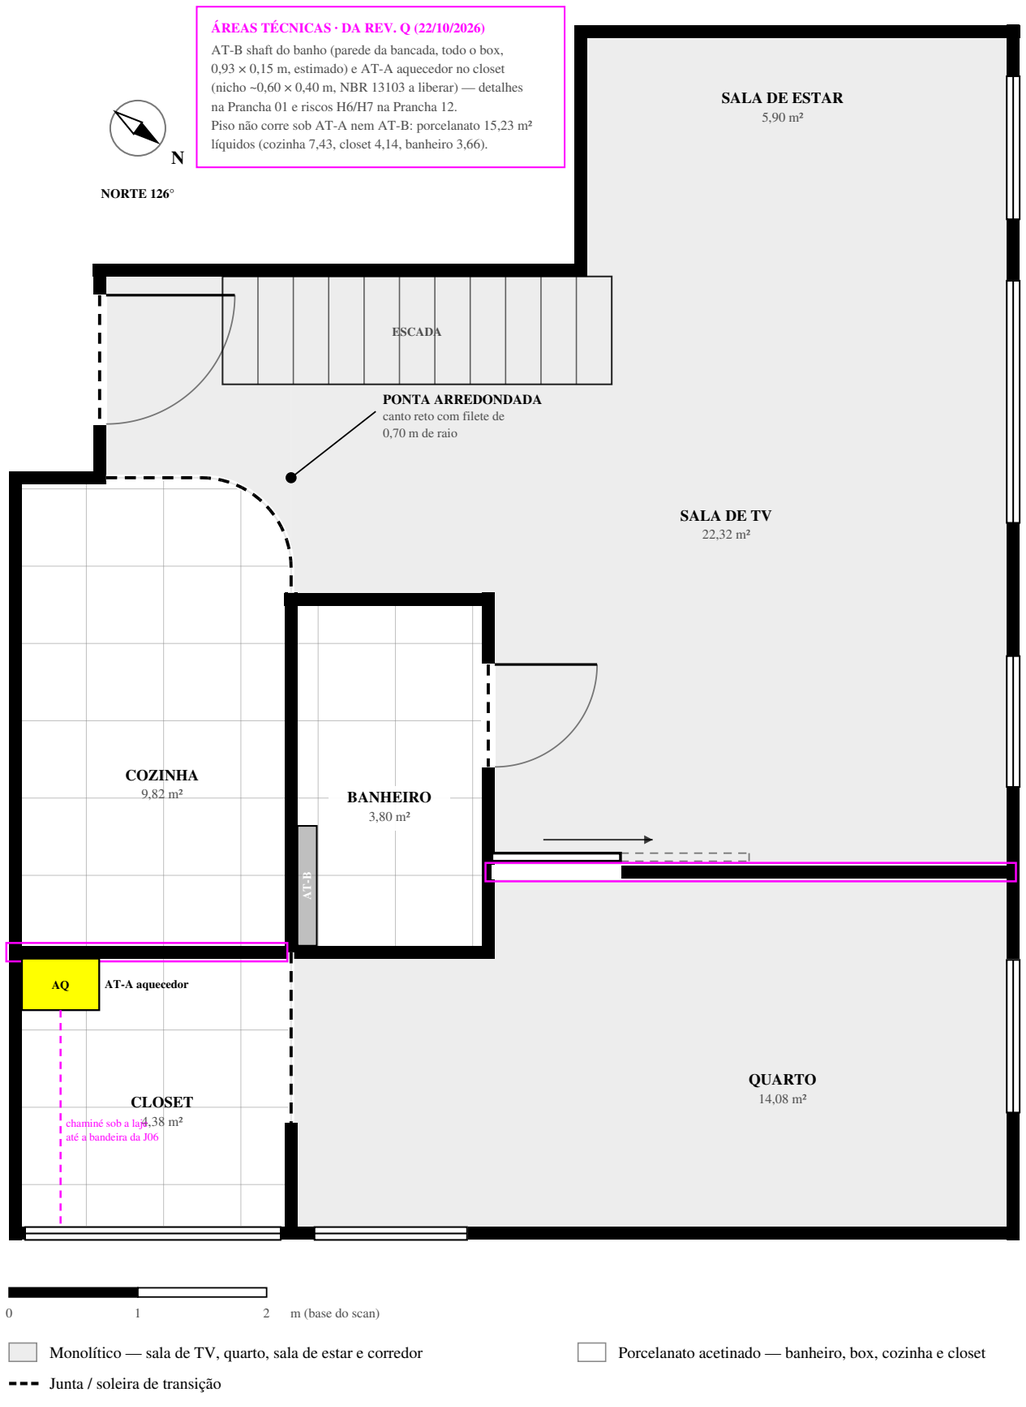

QUADRO DE ÁREAS

Sistema	Onde	Área
Monolítico	sala de TV 22,32 + quarto 14,08 + sala de estar 5,90 + corredor 2,39	44,69 m²
Porcelanato	acetinado: cozinha 7,43 + closet 4,14 + banheiro e box 3,66 (líquidos)	15,23 m²
+ reserva de 10%	cortes, perdas e reposição futura do porcelanato	16,75 m²
MainFloor	total revestido, líquido das áreas técnicas	59,92 m²

Opção B: porcelanato acetinado onde há água e gordura, monolítico no resto.
Porcelanato no banheiro e no box e na zona contínua cozinha + closet; monolítico na sala de TV, no quarto, na sala de estar e no corredor. O contorno da zona e a ponta arredondada não mudam.

Acetinado no box: conferir o coeficiente de atrito molhado.
Acabamento acetinado varia muito de fabricante para fabricante. No banheiro e no box, exigir na ficha técnica atrito dinâmico adequado a área molhada (mín. 0,4) — ou usar no box a versão antiderrapante da mesma linha. Formato, cor e rejunte a definir; a grade de 0,60 m é ilustrativa.

O monolítico agora é o pano grande: 44,69 m² pedem projeto de juntas.
Cimentício trabalha em painéis de 3 a 6 m de lado; microcimento reduz as juntas às do substrato e ao perímetro. Lugares naturais: as soleiras da entrada e do banheiro, a linha da porta de correr P03 e o encontro com o porcelanato. Pedir a paginação de juntas junto com a proposta.

Na ponta arredondada o monolítico acompanha e o porcelanato é cortado.
Filete de 0,70 m de raio, canto reto nos demais trechos. O monolítico, moldado in loco, segue a curva sem esforço; do lado do porcelanato as peças são cortadas em curva (jato d'água ou serra) e o perfil de transição curvo fica no encontro.

As duas espessuras se acertam no contrapiso, não na soleira.
Porcelanato com argamassa colante e monolítico somam alturas diferentes: o acerto é no contrapiso (P06), para os dois se encontrarem rentes, sem degrau.

Sequência sugerida: porcelanato e perfil, depois o monolítico.
O monolítico é aplicado contra o perfil de transição já fixado e cura antes da marcenaria: o closet (M01) só volta com o piso curado.

Revestimento contínuo: toda a área de piso é revestida, inclusive sob móveis e equipamentos — nenhum recorte de mobiliário foi descontado. Áreas conforme o scan de 02.09.2026.
Estudo preliminar de superfície: não substitui especificação de sistema, projeto de juntas nem memorial de aplicação do fornecedor.