

Planta baixa cotada — estado proposto

Folha de referência dimensional. Cotas em metros, sobre o levantamento por scan de 02.09.2026; conferir em campo antes de qualquer medição.

norte 126° — medido pela rosa do pavimento superior

pé-direito 2,62 m na laje · 2,42 m com o forro atual

QUADRO DE AMBIENTES — LEVANTAMENTO (m, m²)

Ambiente	Área	Perímetro	Bounding box	Inscrita
Sala	23,00 m²	20,7 m	5,6 × 4,8	4,8 × 4,0
Quarto	13,40 m²	16,2 m	5,6 × 2,5	5,6 × 2,1
Cozinha	8,90 m²	13,7 m	4,7 × 2,1	4,7 × 1,4
Jantar	5,90 m²	10,1 m	3,3 × 1,8	—
Closet	5,30 m²	9,3 m	2,5 × 2,1	—
Banheiro	3,80 m²	8,1 m	2,6 × 1,4	—
MainFloor	60,30 m²	78,1 m	7,85 × 9,43	—

Como esta planta foi levantada.

Scan 3D Polycam, captura de 02.09.2026, relatório exportado em 07.09.2026. Paredes, vãos e polígonos de ambiente foram lidos do vetor do arquivo em pontos PDF e convertidos pela escala 45,66 pt/m, conferida duas vezes contra as cotas gerais: 358,33 pt / 7,85 m e 430,56 pt / 9,43 m. O próprio relatório avisa que são estimativas — nenhuma cota aqui substitui medição em campo.

Pé-direito: 2,42 m com o forro atual, 2,62 m na laje.

Alturas informadas pelo cliente; o relatório do scan mede 2,40 m com forro, o que confere. Com a retirada total do forro (D07) ganham-se os 0,20 m de plenum. É essa folga que acomoda a porta de correr de 2,29 m: sob o forro de hoje sobriariam 0,13 m, e sobre a laje sobram 0,33 m — espaço para o trilho aparente. Volume passa de 144,51 m³ para cerca de 158 m³ com a laje aparente.

Espessuras e níveis: uma cota única para o pavimento.

Todas as paredes lidas no scan têm 0,10 m. A nova drywall (R01) repete a espessura, salvo se o trilho da porta de correr for embutido em cassete — aí a parede engrossa. O banheiro passa a nascer na mesma cota do piso seco (P05), sem degrau de soleira, e todo o contrapiso é lixado e nivelado (P06): ±0,00 é o piso acabado atual, e o nível final precisa ser amarrado ao hall.

Diferença entre as áreas do relatório.

Área externa 64,70 m² (inclui paredes), área útil 60,20 m² pelo relatório e 60,30 m² pela soma dos seis ambientes — a diferença é arredondamento. O caderno usa 60,30 m². Área de parede 130,40 m², área de janela 12,70 m², perímetro somado dos ambientes 78,10 m.

Bounding box não é o ambiente.


As dimensões do relatório vêm em duas leituras: o menor retângulo que contém o ambiente (B) e o maior retângulo inscrito (I). Em planta irregular — sala e cozinha — as duas divergem bastante: usar a inscrita para conferir mobiliário e a cotada em planta para obra.

O norte foi medido, não arbitrado: 126° do topo da folha.

O relatório do pavimento superior — mesma captura — traz rosa dos ventos e GPS; o do MainFloor não traz nenhum dos dois. As duas plantas estão desenhadas com 180° de diferença, confirmado por dois elementos que os pavimentos compartilham: a caixa da escada e a área da piscina, que só cai no terraço de cima com essa rotação. A pétala N do Upfloor marca −53,97°; somados 180°, dá 126°.

As duas fachadas envidraçadas dão para NOROESTE e NORDESTE.

Noroeste: jantar (J01), sala (J02 e J03) e uma janela do quarto (J04) — é a face que toma o sol de tarde, o mais quente. Nordeste: a outra janela do quarto (J05) e o closet (J06), sol de manhã. As outras duas faces são divisa, a sudeste e a sudoeste. Coordenadas do levantamento: 23°36'46,8"S 46°44'15,8"O, altitude 822 m.

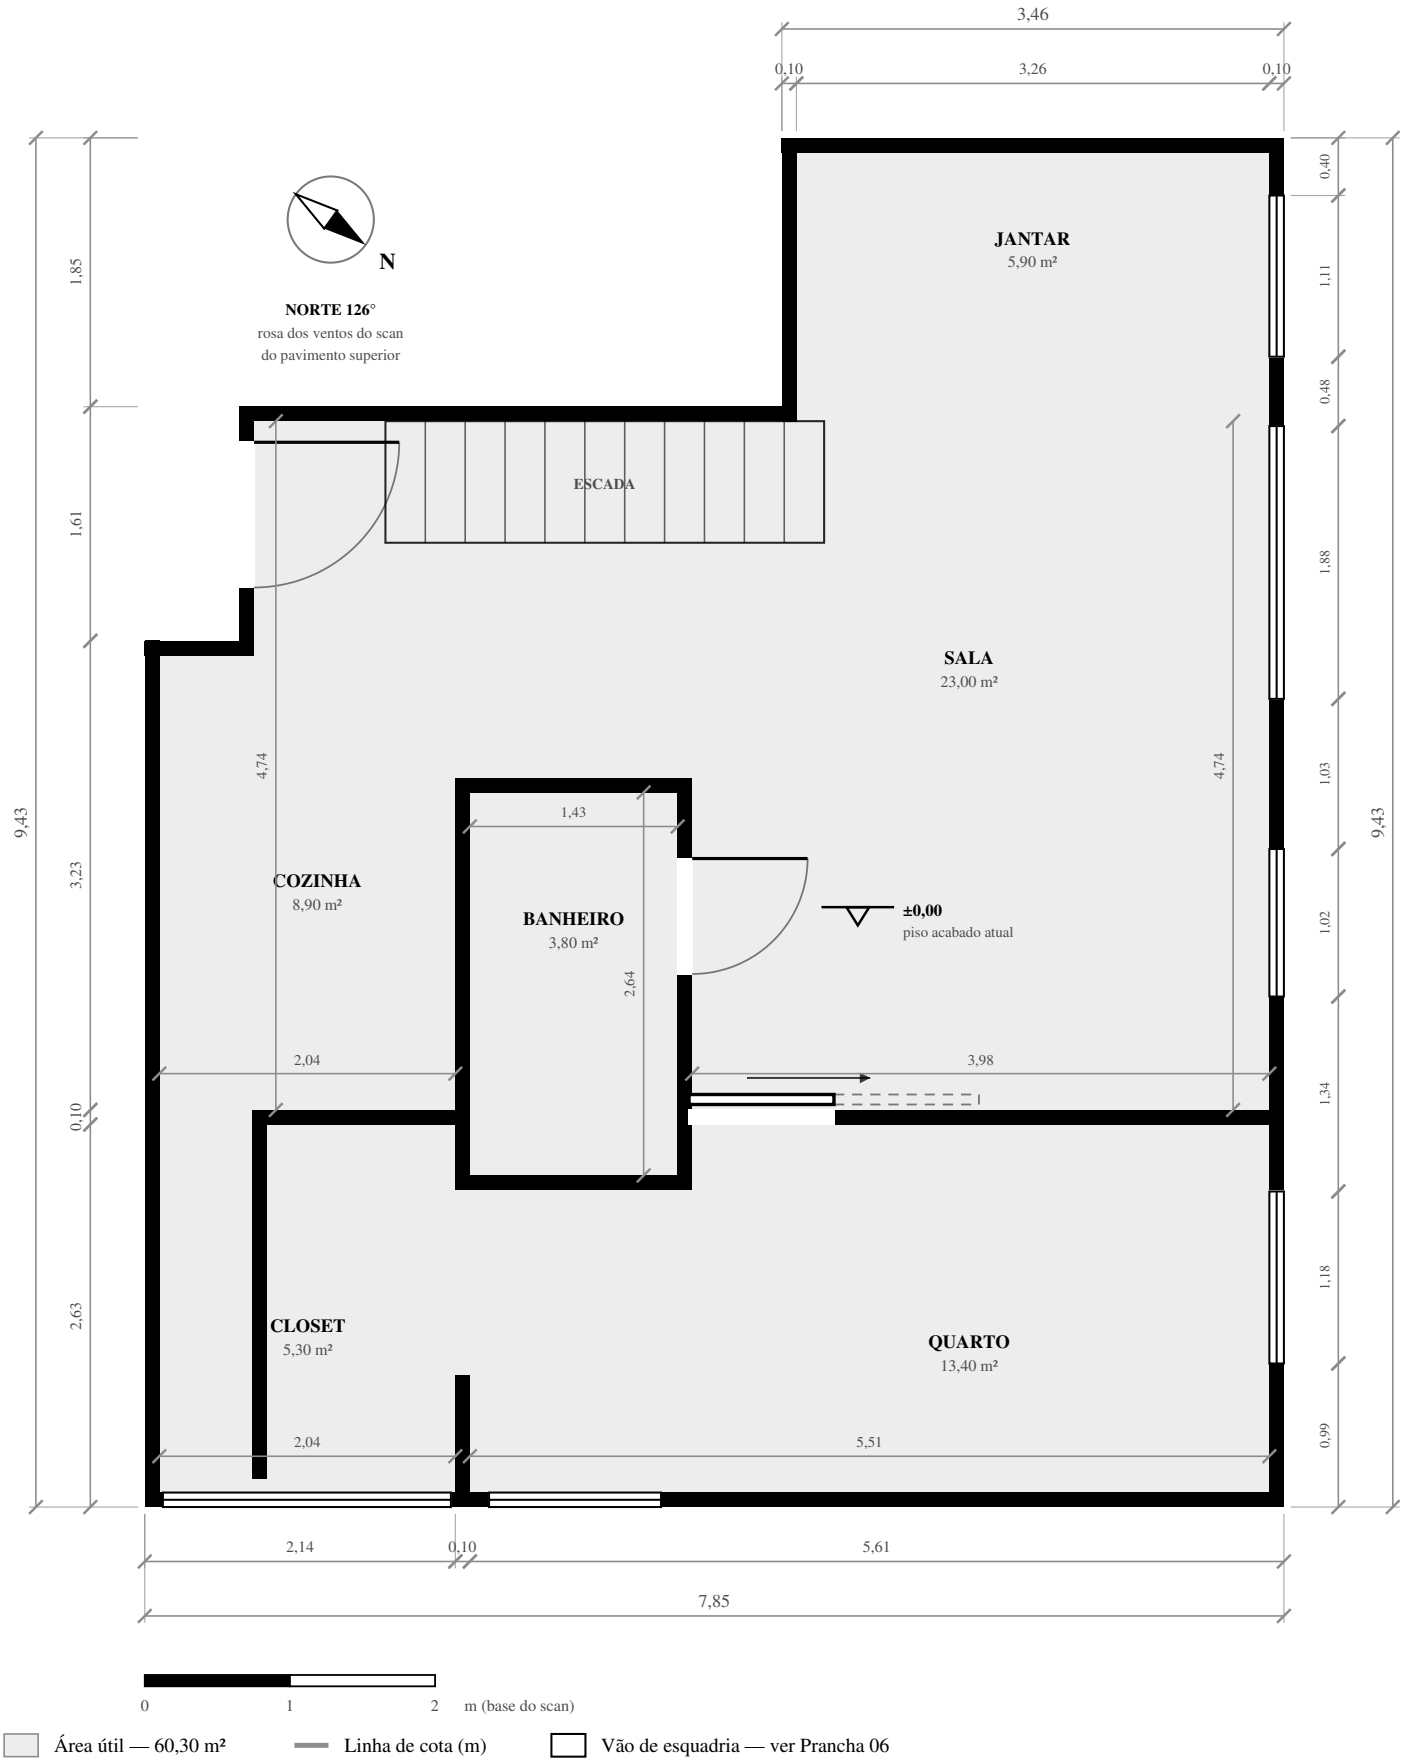



Cotas extraídas do modelo do scan e arredondadas ao centímetro. O relatório do levantamento declara que os valores são estimativas: conferir em campo antes de fabricar esquadria, marcenaria ou bancada. Planta de estudo preliminar. Não é planta executiva liberada: faltam projeto estrutural, hidráulica, elétrico executivo e aprovação do condomínio.

Demolição e desmontagem

Diagrama de escopo sobre o modelo de trabalho. Conferir os alvos presencialmente antes de mobilizar a demolidora.

estado existente: o que sai, o que se prepara

demolir e reconstruir são serviços separados

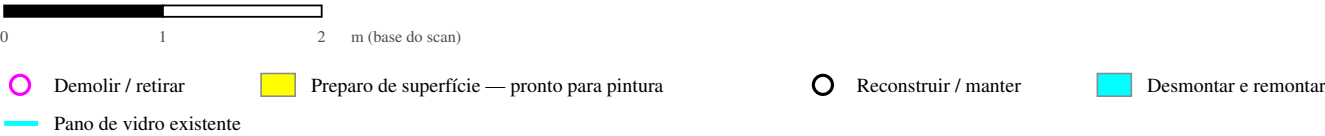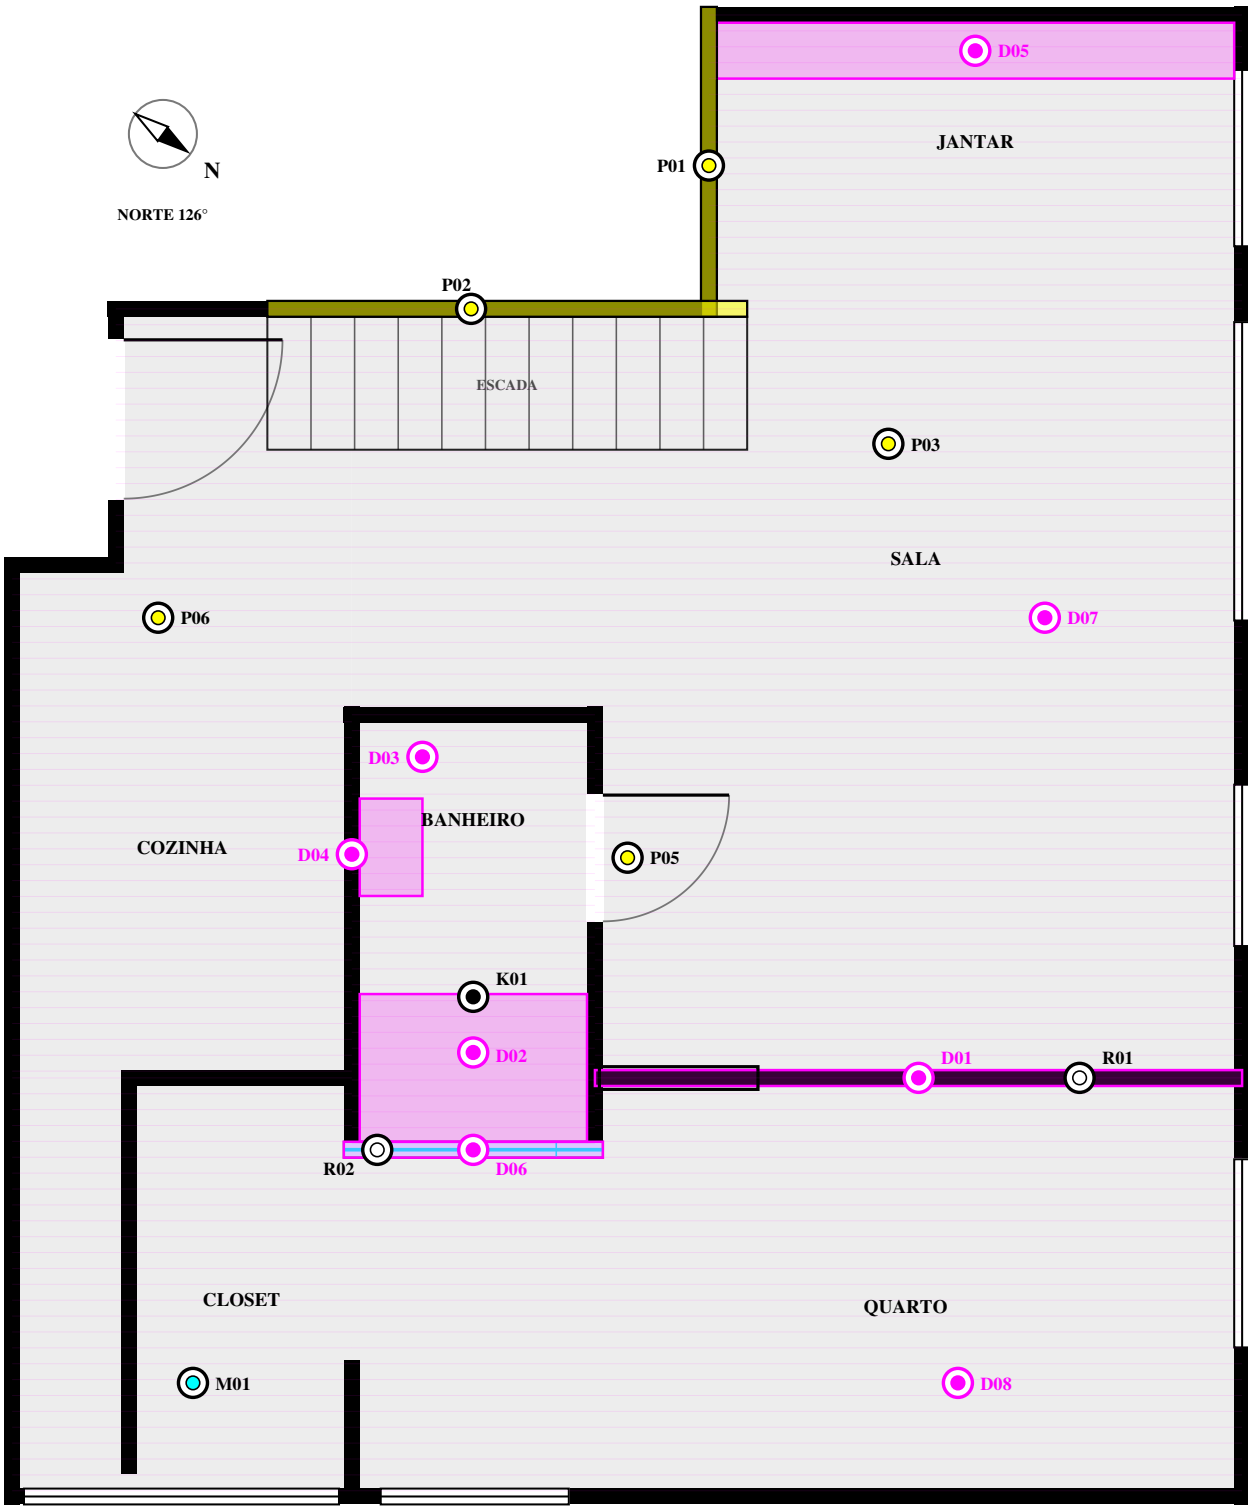

ESCOPO DE DEMOLIÇÃO E DESMONTAGEM

ID	Serviço	Quantidade preliminar
D01	Drywall entre sala e quarto	1 trecho — 4,08 m
D02	Box do banheiro: fechamento e base	1 conjunto
D03	Piso do banheiro: revestimento, base e rebaixo	3,80 m² — descer até a laje
D04	Parede atrás do espelho e da bancada	1 trecho — 2,64 m a conferir
D05	Canto alemão do jantar	1 conjunto — inventário por módulo
D06	Pano de vidro chão-teto do fundo do box	1,63 m, ponta a ponta
D07	Forro: retirar 100%	60,30 m² — teto passa a laje aparente
D08	Retirar pisos do MainFloor	60,30 m² úteis, sem dupla contagem
P01	Parede do jantar: retirar espelho e revestimento	1 trecho — 1,95 m, preparo p/ pintura
P02	Parede sob a escada: retirar revestimento	trecho a confirmar — preparo p/ pintura
P03	Laje: restaurar, descascar, limpar e preparar	60,30 m² — acabamento a definir
P04	Demais paredes com revestimento retirado	preparo p/ pintura — mapear em obra
P05	Nivelar o banheiro com o piso da casa	cota única — soleira sem degrau
P06	Regularizar e lixar todo o contrapiso	60,30 m² — plano e nivelado
R01	Nova drywall sala/quarto, com porta de correr 1,00 × 2,30 m	4,08 m + 1 porta
R02	Nova parede de fechamento do box	1,63 m, no lugar do vidro
M01	Desmontar e remontar closet	1 conjunto — inventário por módulo
K01	Vidro do box — MANTER	1 peça

Esta planta mostra o estado existente.

Box com o pano de vidro de hoje (D06) e drywall ainda sem porta. O proposto — box fechado, porta de correr e porta do banheiro girando para a escada — está nas Pranchas 03, 04 e 05.

Demolir para refazer, não só demolir.

A drywall entre sala e quarto cai e volta (R01), agora com porta de correr de 1,00 × 2,29 m. A folha estaciona no 1,00 m de parede a leste do vão: nada de tomada, quadro ou marcenaria ali. O vidro do fundo do box cai e vira parede (R02): orçar demolição e obra nova à parte.

Banheiro: reforma integral, e agora no nível da casa.

Saem piso, revestimentos, box e a parede atrás do espelho. A base desce até a laje (D03) para o banheiro nascer na cota do piso seco (P05) — soleira sem degrau, o que joga a contenção de água para dentro do box: ralo linear, caimento e fecho de vidro fazem o serviço que o degrau fazia.

Todo o contrapiso lixado, plano e nivelado (P06).

Depois de tirar os pisos (D08), a base inteira precisa ficar reta: é condição do monolítico, que copia o que está embaixo. Uma cota única de piso acabado nos 60,30 m², amarrada ao hall.

Regra de escopo: toda parede que perder revestimento é preparada para pintura.

Mapeado hoje em P01 e P02; P04 cobre o que aparecer em obra. Definir o nível de acabamento antes de orçar — massa e lixa não são a mesma linha que regularizar parede castigada.

A laje inteira é serviço, não sobra da demolição (P03).

Com o forro fora, a laje aparece como está: fixação, marca de fôrma, desnível, fissura. Prever restauro, descascamento e limpeza dos 60,30 m², com o acabamento definido com a empreiteira.

Closet: etiquetar módulos e ferragens, fotografar, acondicionar e proteger.


A área de 5,30 m² é do ambiente, não é área de marcenaria.

Piso monolítico

Sistema único em todo o MainFloor, com o banheiro à parte. Cores ilustrativas; nenhum produto, espessura ou acabamento especificado.

proposta de cumaru encerrada

piso contínuo — sem junta de material entre ambientes secos

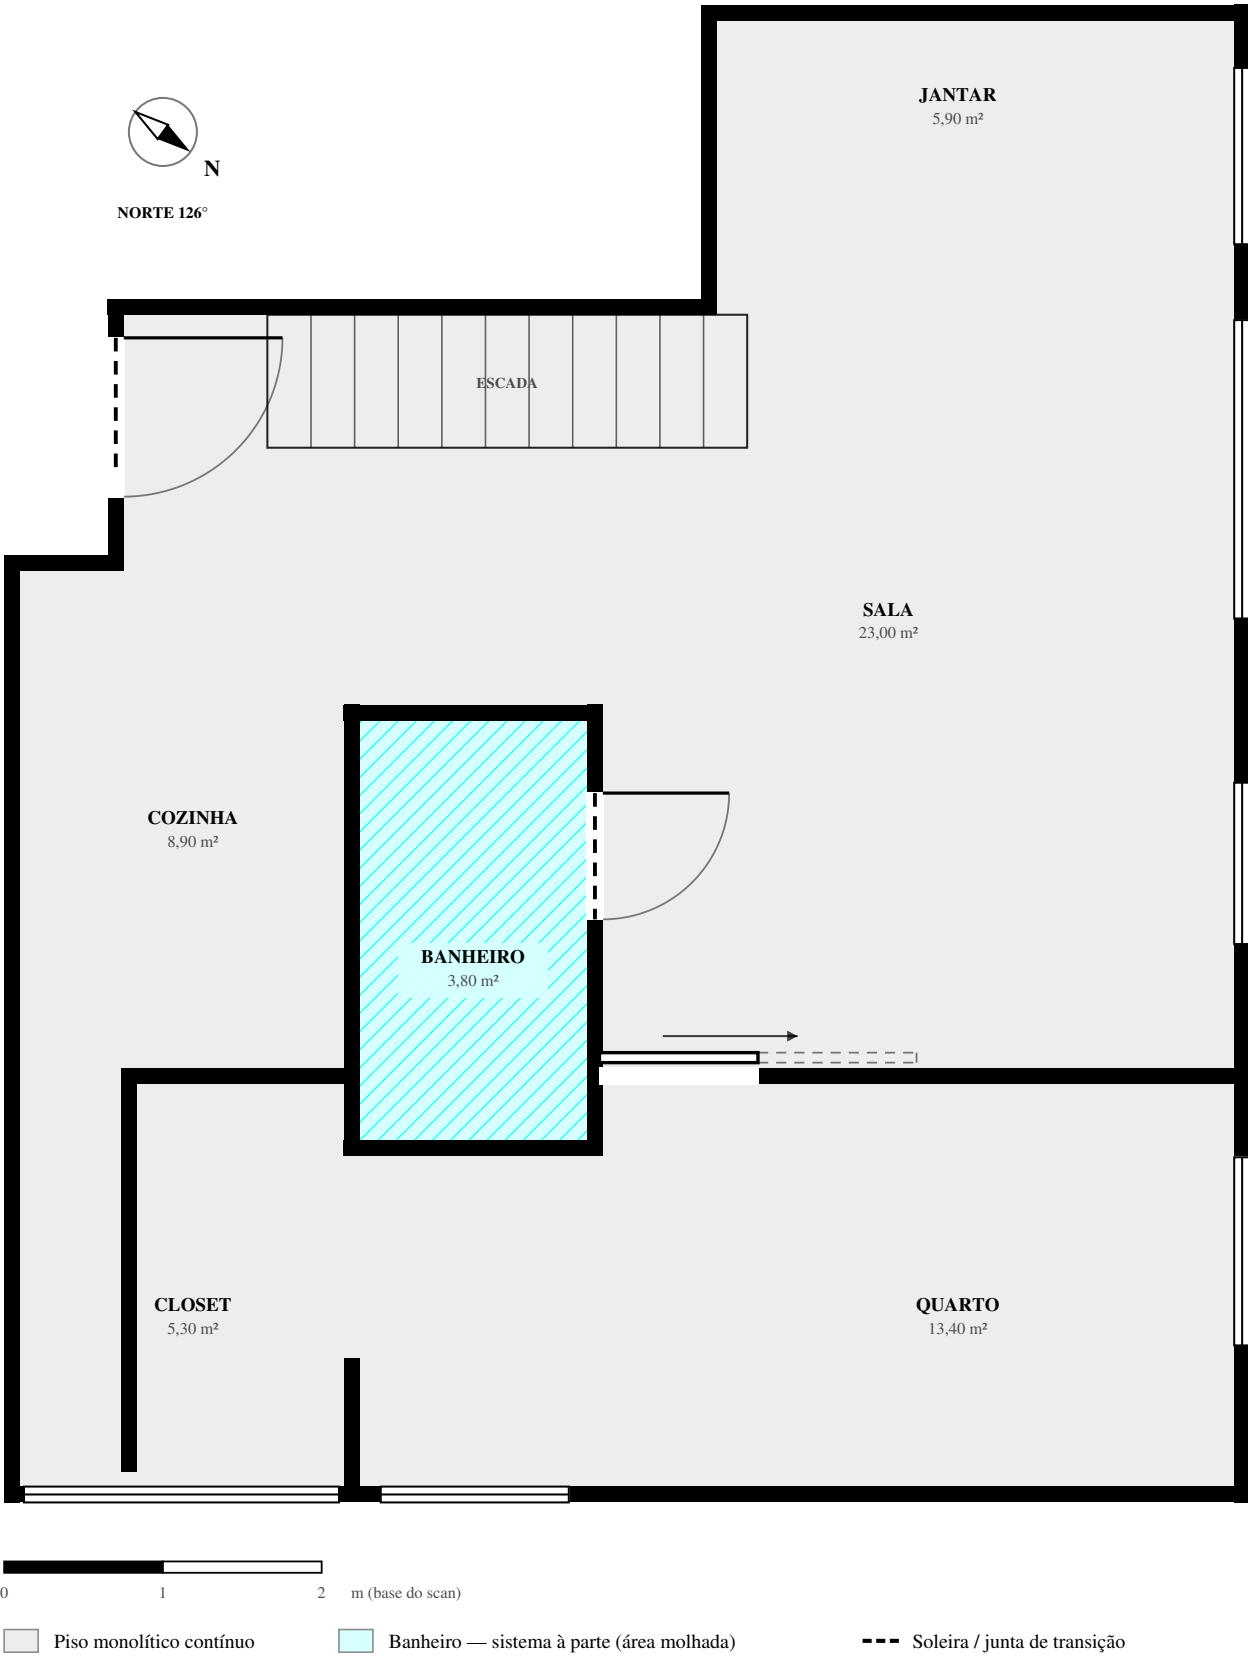

QUADRO DE ÁREAS

Ambiente	Sistema	Área
Sala	monolítico contínuo	23,00 m²
Quarto	monolítico contínuo	13,40 m²
Cozinha	monolítico contínuo	8,90 m²
Jantar	monolítico contínuo	5,90 m²
Closet	monolítico contínuo	5,30 m²
Monolítico — total	cinco ambientes, sem junta de material	56,50 m²
Banheiro	sistema à parte, área molhada	3,80 m²
MainFloor	total do pavimento	60,30 m²

Um sistema só, sem junta de material entre os ambientes secos.

Com o cumaru fora, a ponta em curva da cozinha perde a função: ela existia apenas para resolver o encontro entre a madeira e o monolítico. O piso corre contínuo da entrada ao quarto; as únicas transições são a soleira do banheiro — agora sem degrau — e a da entrada.

Juntas de movimentação são projeto, não improviso de obra.

Monolítico contínuo em 56,50 m² trabalha: prever juntas conforme o sistema escolhido, nos vãos de porta e nos encontros com a estrutura. Posição e desenho entram no executivo, junto com o fornecedor — uma trinca num piso sem junta não tem remendo invisível.

A base manda no resultado — o monolítico copia o que está embaixo.

Depois de retirar os pisos (D08), todo o contrapiso é lixado, regularizado e nivelado (P06), com conferência de aderência, umidade e fissuras. Espessura, sistema e acabamento ainda não estão especificados: cor e textura do desenho são ilustrativas.

O banheiro fica fora do monolítico, mas na mesma cota.

Sistema próprio, com impermeabilização, caimento e acabamento antiderrapante — só que nivelado com o piso seco (P05): a soleira passa a ser junta de material, não degrau. Sem degrau, a contenção de água é resolvida dentro do box, com ralo linear e fecho de vidro. A impermeabilização sobe também na parede nova do fundo do box (R02).

Encontro com a parede.

Rodapé embutido, negativo ou pintura direta mudam o preparo das paredes e o corte do piso: definir antes de a empreiteira fechar o preparo para pintura.

Sequência importa mais que no piso em régua.

O monolítico entra depois das paredes prontas e antes da marcenaria: o closet (M01) só volta depois do piso curado. Prever tempo de cura e proteção da superfície até o fim da obra.

Sem reserva de corte.


Aplicação moldada in loco não tem perda de régua, mas isso não é margem zero: prever retrabalho de textura e acerto de bordas. Os degraus da escada estão fora da conta; o piso sob a escada permanece.

Teto: laje aparente, iluminação e ar-condicionado

Distribuição conceitual sobre a laje de concreto. Reservas de posição, não quantidade final de luminárias nem de equipamentos.

sem forro — tudo aplicado na laje

piscina do pavimento superior sobre a sala

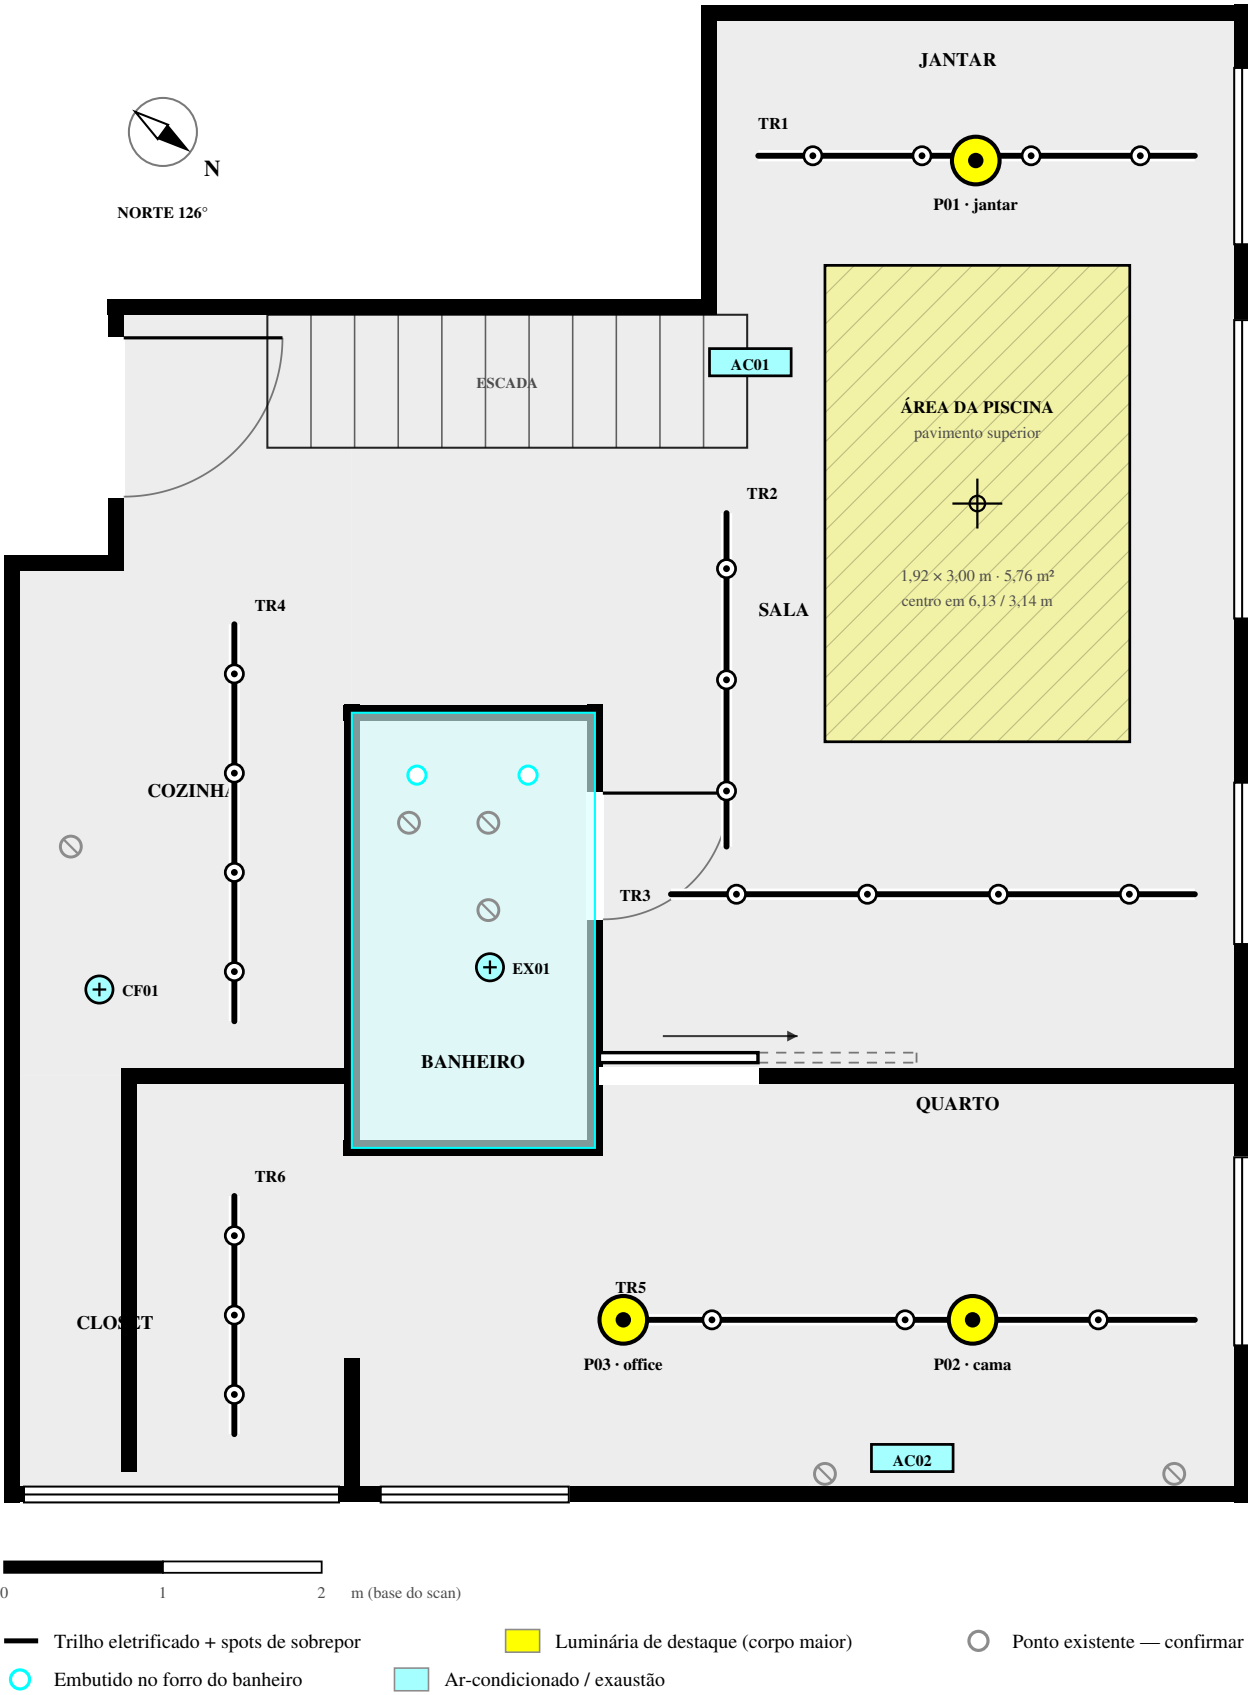

ILUMINAÇÃO POR AMBIENTE

Ambiente	Alvo geral	Fluxo inicial	Temperatura de cor
Sala	150 lux	7.188 lm	2.700 K
Quarto	150 lux	4.188 lm	2.700 K
Cozinha	300 lux	5.563 lm	3.000 K
Jantar	150 lux	1.844 lm	2.700 K
Closet	200 lux	2.208 lm	3.000 K
Banheiro	200 lux	1.583 lm	3.000 K

AR-CONDICIONADO — REGRA SIMPLIFICADA 600/800 BTU/h POR m²

Zona	Área	Base sombra	Base sol
Social + cozinha	37,80 m²	22.680 BTU/h	30.240 BTU/h
Quarto + closet	18,70 m²	11.220 BTU/h	14.960 BTU/h
Total sem banheiro	56,50 m²	33.900 BTU/h	45.200 BTU/h

Não há forro: a laje de concreto é o teto acabado, a 2,62 m do piso.

Com o forro atual são 2,42 m; a retirada (D07) devolve os 0,20 m de plenum. É nessa faixa que entram trilho, perfilado e evaporadora — e é ela que dá os 0,33 m acima da porta de correr de 2,29 m. Fora do banheiro, único ambiente que mantém forro, nada de embutido.

Fiação e infraestrutura ficam à vista.

Perfilados ou eletrocaldas pintadas, alinhados às vigas e aos trilhos: o caminho da fiação vira desenho, não sobra de obra.

P01, P02 e P03 são as três luminárias de destaque pedidas pelo cliente

— jantar, cama e office. Corpo e diâmetro maiores que os spots dos trilhos, em pendente ou plafon de sobrepor. No quarto o TR5 passa a correr no eixo de P02 e P03, a 8,28 m: as duas podem ser alimentadas pelo próprio trilho, com adaptador, dispensando saídas novas na laje.

Traçado dos trilhos revisado conforme a sua marcação:

TR3 desceu para 5,60 m, ganhando recuo da drywall; TR5 desceu para 8,28 m, no eixo das duas luminárias do quarto; TR6 saiu de junto da parede oeste e foi para 1,45 m, no mesmo eixo do TR4 — os dois lêem como uma linha só. O TR2 foi encurtado para 5,30 m: no traçado anterior ele cruzava o TR3 no meio da sala, e dois trilhos não se cruzam — se tiverem de se encontrar, é com conector T.

Sem forro para dutar, e fachada envidraçada a noroeste.

Evaporadoras hi-wall ou cassette aparente, com frigorígena, dreno e interligação elétrica aparentes, em calha e com caimento contínuo. Sala e jantar tomam o sol da tarde: dimensionar pela coluna base sol, não pela sombra. Somente Electrolux — marca igual não garante compatibilidade.

A piscina do pavimento superior fica sobre a sala — 1,92 × 3,00 m, centrada em

6,13 / 3,14 m do canto noroeste. Essa laje não recebe furação: nem luminária, nem trilho, nem evaporadora ou tubulação podem invadi-la, e a região exige impermeabilização e sobrecarga verificadas em estrutura. Nenhum trilho a invade: TR2 corre a oeste e TR3 passa 0,96 m ao sul.

A reserva AC01 caía dentro da projeção da piscina.

Foi deslocada para oeste, mantendo a insuflação para sala e jantar. A posição definitiva depende de confirmar apoio acima do limite sala/jantar e o modelo da condensadora existente: não assumir que ela admite duas evaporadoras.

Vazões de referência, a validar com perda de carga do duto:

banheiro 3,8 × 2,42 × 10 = 92,0 m³/h (mantém forro); coifa 8,9 × 2,62 × 12 = 279,8 m³/h — o segundo só valeria com cozinha isolada; integrada, seleciona-se por captura. Rotas próprias.


Fluxo = área × lux ÷ (0,60 × 0,80). Fatores de utilização e manutenção são hipóteses; a laje aparente escura reduz o fator de utilização e deve ser reavaliada.
Carga térmica não é carga final: a fachada envidraçada a noroeste, a piscina sobre a sala, a escada aberta e a ocupação mudam o resultado. Estudar 2 ou 3 evaporadoras; não há número fechado.

Tomadas, comandos e quadro

Reservas de localização, sem circuitos executivos. Posições existentes conforme marcação do cliente sobre o estudo anterior.

quadro junto à porta de entrada

trajetos aparentes: não há forro

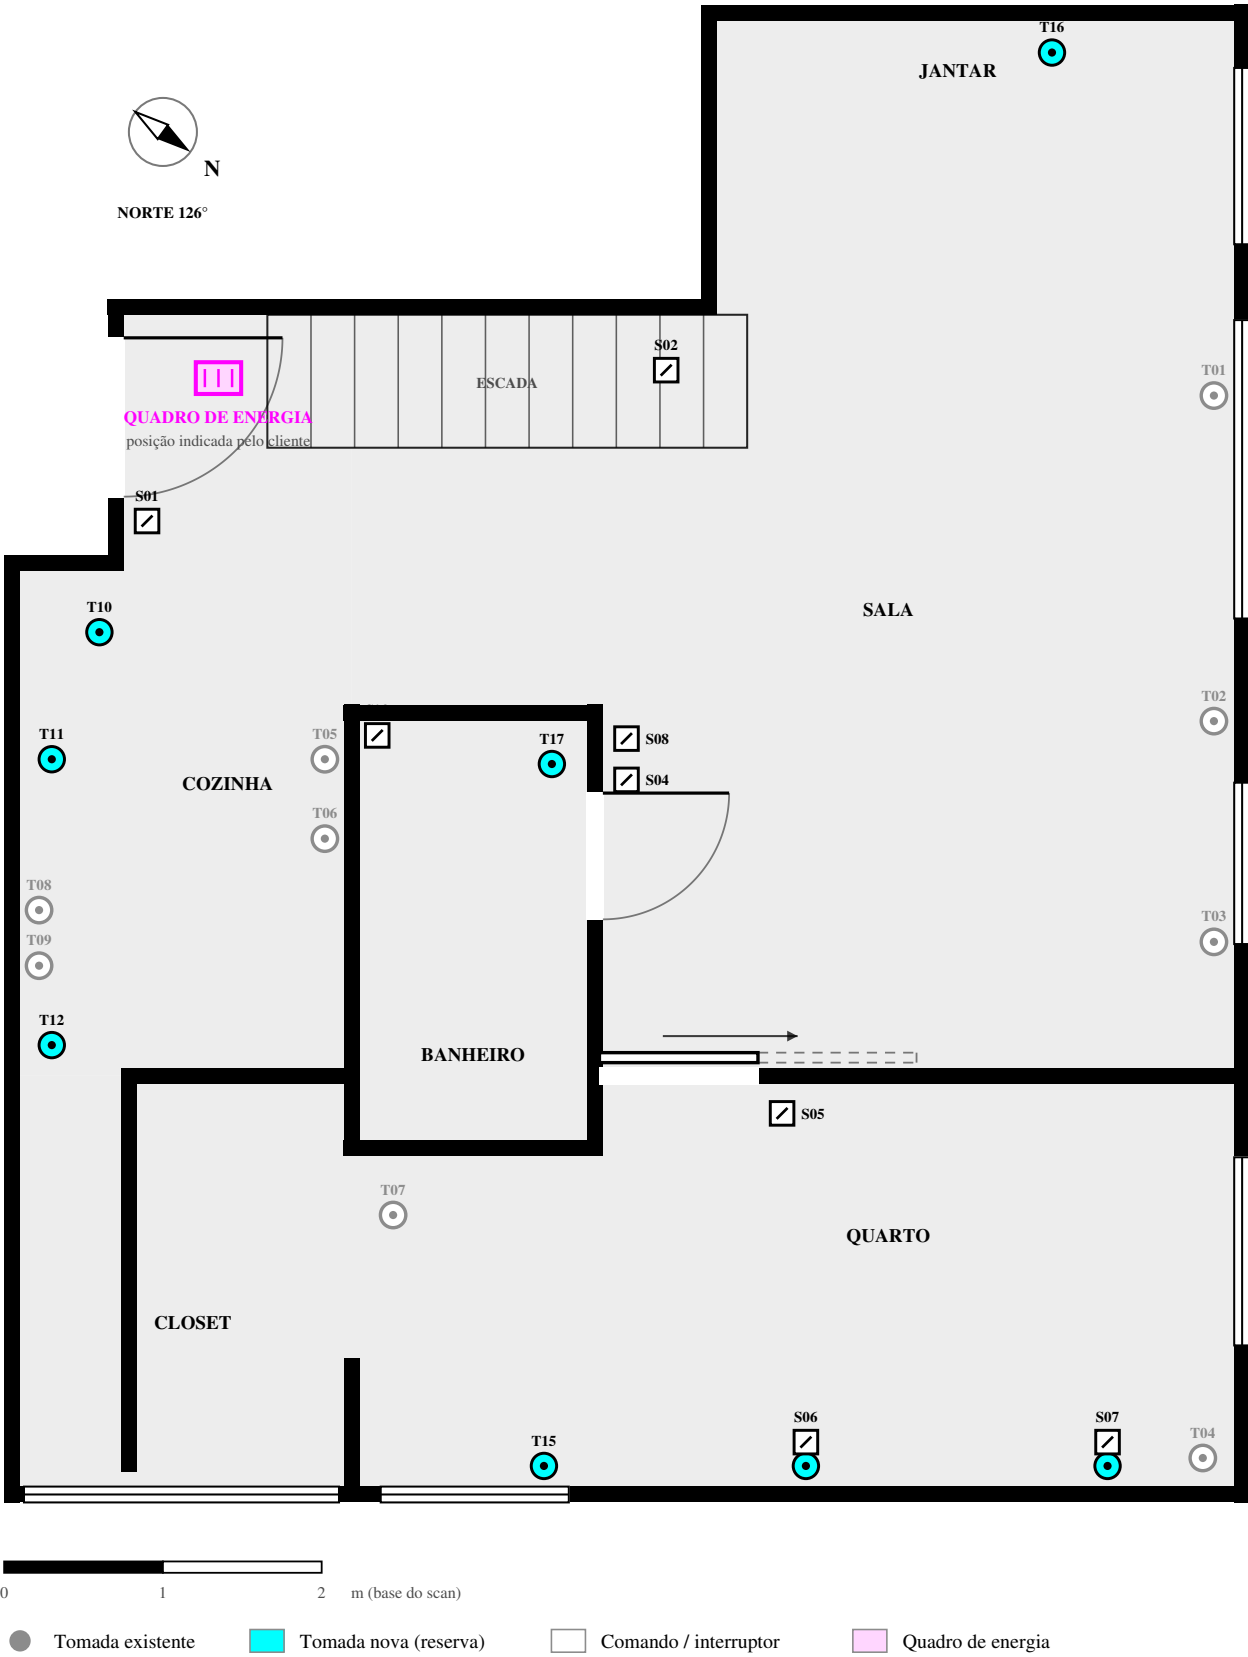

RESERVAS DE INFRAESTRUTURA ELÉTRICA

Grupo	Reservas	Revisão necessária
Quadro elétrico	junto à porta de entrada, na extensão da cozinha	tensão, fases, demanda, proteção e espaços
Tomadas existentes	9 posições levantadas pelo cliente	confirmar altura, caixa e circuito
Tomadas novas	8 reservas — T10 a T17	não é número normativo nem total final
Comandos	8 posições — S01 a S08, duas na cabeceira	lado da porta, marcenaria e cenas
Cozinha	geladeira, forno, lava-louças, coifa e bancada	pontos dedicados, circuito exclusivo
Ar-condicionado	alimentação conforme manual da unidade	quem alimenta varia com o sistema
Banheiro	ponto junto ao lavatório a validar	volumes de proteção, DR e cargas

O quadro de energia foi localizado pelo cliente: fica junto à porta de entrada, no início da extensão da cozinha. Com a porta de entrada medindo 1,00 m de vão, a folha tem 1,00 m de raio e passa sobre o quadro: ou ele desloca, ou a porta perde abertura. O S01 já saiu do vão e foi para 3,25 m. Confirmar espaço livre e altura antes de fixar — todo o traçado sai dali.

Sem forro, os trajetos ficam aparentes. A distribuição no teto passa a ser perfilado ou eletrocalha pintada, acompanhando os trilhos de luz da Prancha 04; as descidas para tomadas e comandos correm embutidas na parede. Isso vira desenho: definir caminhos e separações antes de medir eletrodutos e cabos.

Alturas de intenção, sempre conferidas com mobiliário e acabamento: tomadas gerais 0,30 m; comandos 1,10 m; pontos de bancada em torno de 1,15 m. As marcações não autorizam instalação em parede sem localizar estrutura e tubulações.

Os pontos T01 a T09 são os existentes que você marcou em planta. Estão desenhados na posição aproximada do levantamento: servem para decidir o que se aproveita e o que se remaneja, não para medir. T10 a T17 são reservas novas do estudo.

A porta de correr reserva um trecho de parede — e isso é questão elétrica. A folha estaciona no 1,00 m de drywall a leste do vão, pela face da sala: nesse trecho não cabe tomada, interruptor nem quadro. Por isso o S05 foi para a face do quarto, encostado no batente leste, fora do caminho da folha. S06 e S07 seguem na cabeceira, um de cada lado da cama, em paralelo com as luminárias P02 e P03 da Prancha 04.

O que cada comando aciona — leitura de folha, não diagrama de circuito: S01 entrada e cozinha (TR4 e coifa, junto ao quadro) · S02 jantar (TR1 e P01) · S03 arandelas do espelho, junto à bancada · S04 banheiro, na quina do box · S05 quarto, ao lado da porta de correr (TR5, P02 e P03) · S06 e S07 cabeceira, em paralelo com o S05 · S08 sala (TR2 e TR3).

S08 é o novo comando da luz da sala. Fica na quina do box voltada para a escada, encostado no S04 do banheiro: é o primeiro anteparo de quem entra na sala vindo da escada ou da cozinha. Os dois ocupam a faixa de parede de 0,45 m entre a quina e o batente — cabe, mas é a folga exata de duas placas 4×2: confirmar em obra antes de fechar a caixa. Se a sala for acender também pelo outro extremo, S08 precisa de paralelo junto à porta nova da drywall, em conjunto com o S05.

Circuitos, seções, disjuntores, aterramento, DR, demanda e proteção contra surtos ficam a cargo do projeto elétrico após o levantamento. Não usar estas reservas como projeto para o eletricista executar.

Quadro de esquadrias e dados do levantamento

Todas as esquadrias na mesma escala. Alturas conforme medição do cliente; larguras do scan. Vão livre, não marco: conferir antes de fabricar.

seis janelas · três portas

peitoril, sentido de abertura e material a levantar

J01

1,10 × 1,63 m
Janela · Jantar
manter

J02

1,90 × 1,63 m
Janela · Sala
manter

J03

1,00 × 1,63 m
Janela · Sala
manter

J04

1,20 × 1,63 m
Janela · Quarto
manter

J05

1,20 × 1,63 m
Janela · Quarto
manter

J06

2,00 × 1,50 m
Janela · Closet
manter — única com 1,50

P01

1,00 × 2,29 m
Porta · Entrada
manter

P02

0,80 × 2,00 m
Porta · Banheiro
giro invertido — abre p/ escada

P03

1,00 × 2,29 m
Porta de correr · Quarto
nova, na drywall R01

0

1

2

m (elevação das esquadrias)

Janela

Porta

Nível do piso acabado

DADOS DO LEVANTAMENTO

Dado	Valor	Observação
Área útil (soma dos ambientes)	60,30 m²	relatório arredonda para 60,20
Área externa do pavimento	64,70 m²	inclui espessura de paredes
Área de parede	130,40 m²	sem vãos
Área de esquadria	13,44 m²	seis janelas, vão — scan dava 12,70
Volume	144,51 m³	com forro; ~158 m³ na laje aparente
Perímetro somado dos ambientes	78,10 m	não é perímetro do pavimento
Pé-direito — laje	2,62 m	depois de retirar o forro (D07)
Pé-direito — forro atual	2,42 m	plenum de 0,20 m
Captura / exportação	02.09 / 07.09.2026	scan 3D Polycam
Coordenadas	23°36'46,8"S 46°44'15,8"O	altitude 822 m — do scan superior
Norte	126°	do topo da folha, sentido horário

INVENTÁRIO DO SCAN — NÃO É ESPECIFICAÇÃO

Ambiente	Itens reconhecidos pelo scan (m)
Sala	sofá 2,60 × 1,60 · mesa de centro 1,60 × 1,00 · 3 cadeiras · armário 2,50 × 0,40 · escada 0,80 × 3,00
Quarto	cama 1,50 × 2,00 · bancada 3,00 × 0,50 · mesa 0,50 × 0,50 · cadeira
Cozinha	armário 1,60 × 0,60 · cuba 0,70 × 0,60 · geladeira 0,90 × 0,80 (h 1,80) · forno · cooktop · lava-louças
Jantar	armário de canto 2,50 × 0,40 — o canto alemão, item D05 da demolição
Closet	marcenaria não discriminada pelo scan — inventariar módulo a módulo antes de desmontar (M01)
Banheiro	bancada 1,70 × 0,40 · box 0,90 × 1,40 (h 2,10) · cuba 0,60 × 0,50 · bacia 0,40 × 0,70

Todas na mesma escala. Largura × altura de vão livre, não de marco.

Peitoril, sentido de abertura e material não estão medidos: as três informações precisam de visita. Nenhuma esquadria deste caderno está liberada para fabricação.

As alturas das janelas vieram do cliente, não do scan: 1,63 m em cinco das seis.

O relatório dava 1,50 e 1,60 m; a medida em campo é 1,63 m, e só a janela do closet (J06) mantém 1,50 m. Com isso as duas do quarto ficam idênticas — 1,20 × 1,63 — e cai a dúvida de qual era a da fachada noroeste e qual a da nordeste. A área de esquadria sobe para 13,44 m².

P03 é a única esquadria nova.

Porta de correr de 1,00 × 2,29 m na drywall reconstruída, com a folha estacionando no 1,00 m de parede a leste do vão, pela face da sala. P02 mantém a folha existente de 0,80 × 2,00 m e só inverte o giro. P01, a porta de entrada, mede 1,00 × 2,29 m e não é alterada.

O inventário do scan serve para escopo, não para especificação.

É o que o algoritmo reconheceu no dia da captura. Há erro evidente — uma "mesa lateral" de 6,60 × 2,00 m que é a projeção da escada — e há ausência: o closet inteiro não foi discriminado. Use a lista para conferir o que sai, o que se desmonta e o que volta.

O que este caderno ainda não tem, e que um executivo exige:

projeto estrutural para a furação da laje e a área da piscina; hidráulica e esgoto do banheiro e da cozinha; elétrico executivo com diagrama unifilar e cálculo de demanda; projeto de juntas do piso monolítico; detalhamento de marcenaria; e aprovação do condomínio.

Larguras do relatório do scan (captura 02.09.2026); alturas de janela e porta conforme medição do cliente em 12.09.2026. Vão livre; marco, contramarco e acabamento não estão medidos. Quadro de referência de estudo preliminar — não é lista de compra nem pedido de fabricação.

ESTUDO PRELIMINAR — NÃO LIBERADO PARA EXECUÇÃO | 12/09/2026

Prancha 06 / 06 · REV. J