


Piso monolítico

Sistema único em todo o MainFloor, com o banheiro à parte. Cores ilustrativas; nenhum produto, espessura ou acabamento especificado.

proposta de cumaru encerrada

piso contínuo — sem junta de material entre ambientes secos

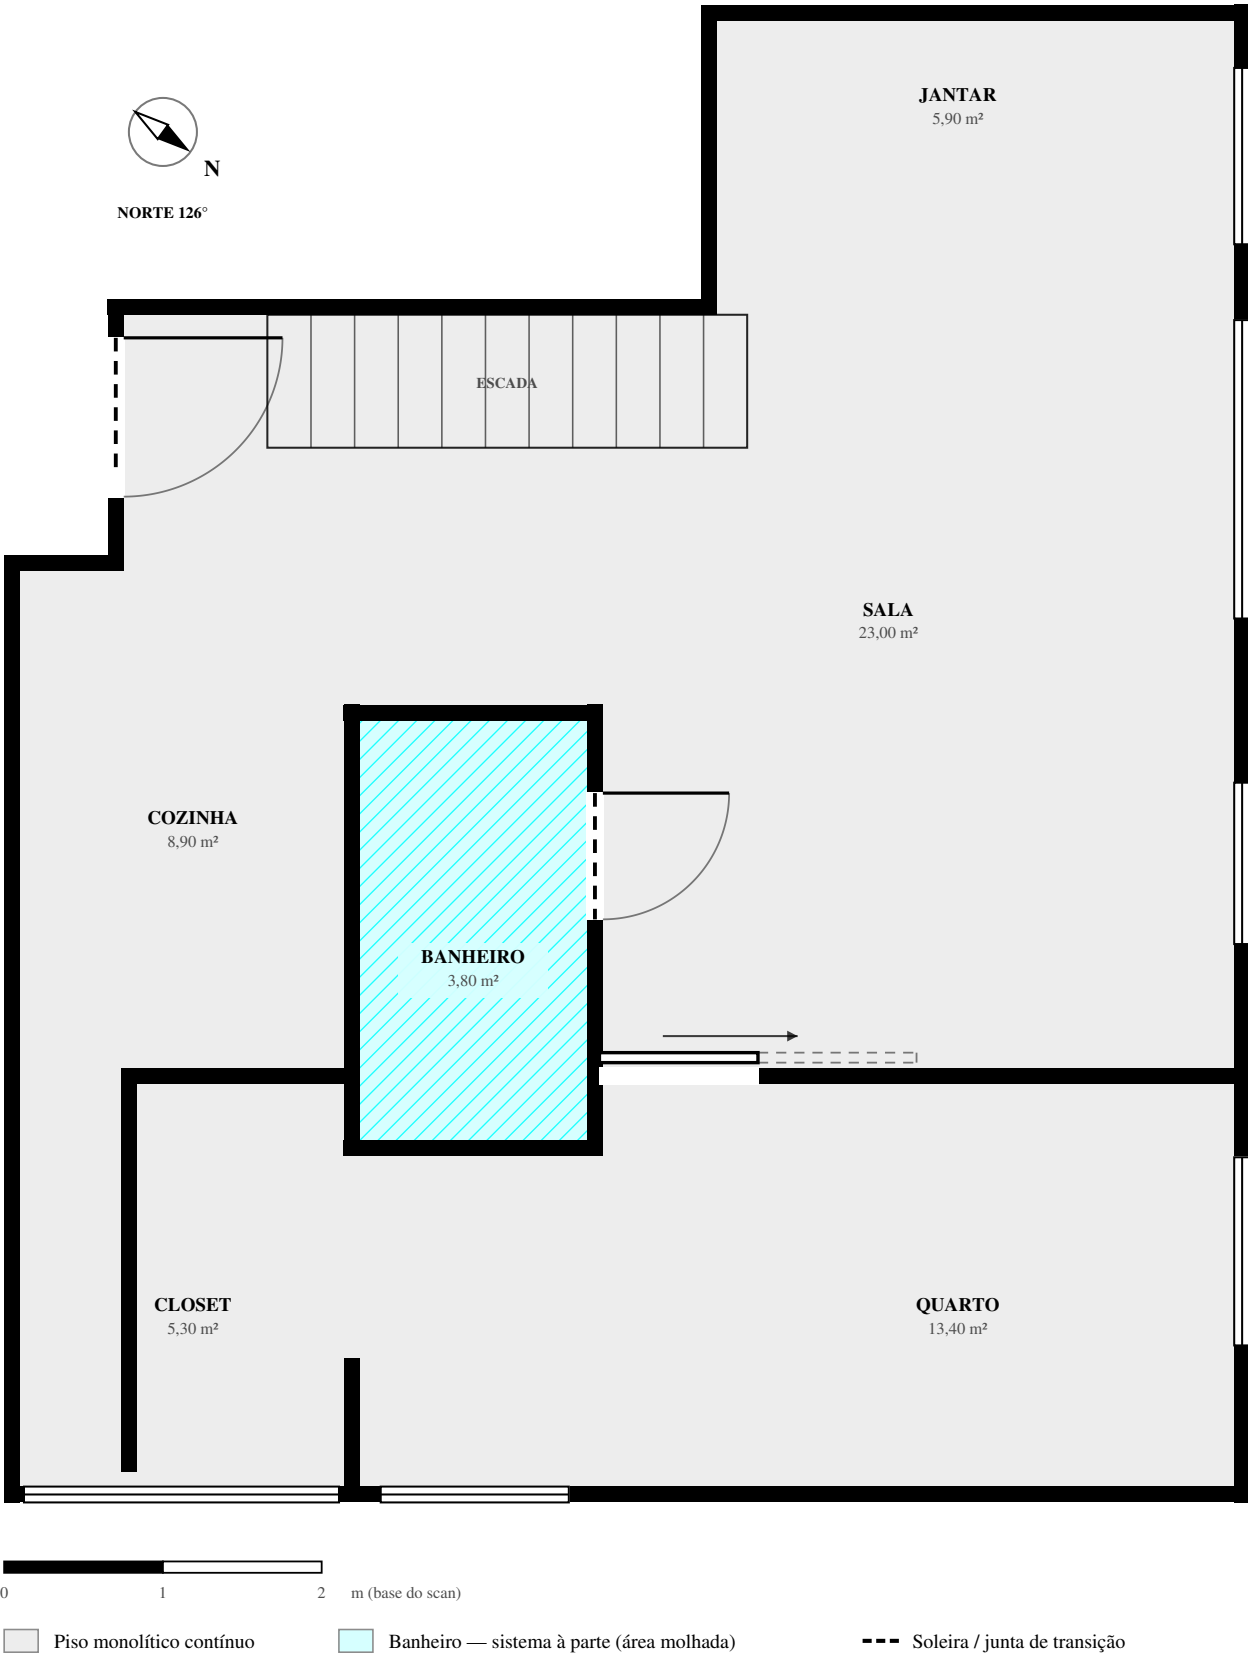

QUADRO DE ÁREAS

Ambiente	Sistema	Área
Sala	monolítico contínuo	23,00 m²
Quarto	monolítico contínuo	13,40 m²
Cozinha	monolítico contínuo	8,90 m²
Jantar	monolítico contínuo	5,90 m²
Closet	monolítico contínuo	5,30 m²
Monolítico — total	cinco ambientes, sem junta de material	56,50 m²
Banheiro	sistema à parte, área molhada	3,80 m²
MainFloor	total do pavimento	60,30 m²

Um sistema só, sem junta de material entre os ambientes secos.

Com o cumaru fora, a ponta em curva da cozinha perde a função: ela existia apenas para resolver o encontro entre a madeira e o monolítico. O piso corre contínuo da entrada ao quarto; as únicas transições são a soleira do banheiro — agora sem degrau — e a da entrada.

Juntas de movimentação são projeto, não improviso de obra.

Monolítico contínuo em 56,50 m² trabalha: prever juntas conforme o sistema escolhido, nos vãos de porta e nos encontros com a estrutura. Posição e desenho entram no executivo, junto com o fornecedor — uma trinca num piso sem junta não tem remendo invisível.

A base manda no resultado — o monolítico copia o que está embaixo.

Depois de retirar os pisos (D08), todo o contrapiso é lixado, regularizado e nivelado (P06), com conferência de aderência, umidade e fissuras. Espessura, sistema e acabamento ainda não estão especificados: cor e textura do desenho são ilustrativas.

O banheiro fica fora do monolítico, mas na mesma cota.

Sistema próprio, com impermeabilização, caimento e acabamento antiderrapante — só que nivelado com o piso seco (P05): a soleira passa a ser junta de material, não degrau. Sem degrau, a contenção de água é resolvida dentro do box, com ralo linear e fecho de vidro. A impermeabilização sobe também na parede nova do fundo do box (R02).

Encontro com a parede.

Rodapé embutido, negativo ou pintura direta mudam o preparo das paredes e o corte do piso: definir antes de a empreiteira fechar o preparo para pintura.

Sequência importa mais que no piso em régua.

O monolítico entra depois das paredes prontas e antes da marcenaria: o closet (M01) só volta depois do piso curado. Prever tempo de cura e proteção da superfície até o fim da obra.

Sem reserva de corte.

Aplicação moldada in loco não tem perda de régua, mas isso não é margem zero: prever retrabalho de textura e acerto de bordas. Os degraus da escada estão fora da conta; o piso sob a escada permanece.