


Quarto adaptável e fechamento da claraboia

A cortina fecha o jantar como quarto de hóspede; a claraboia ganha fechamento elétrico em 2027/28, com a infraestrutura feita agora.

cama de casal com 0,60 m de circulação nos três lados

8,54 m² dentro da cortina · claraboia não furável

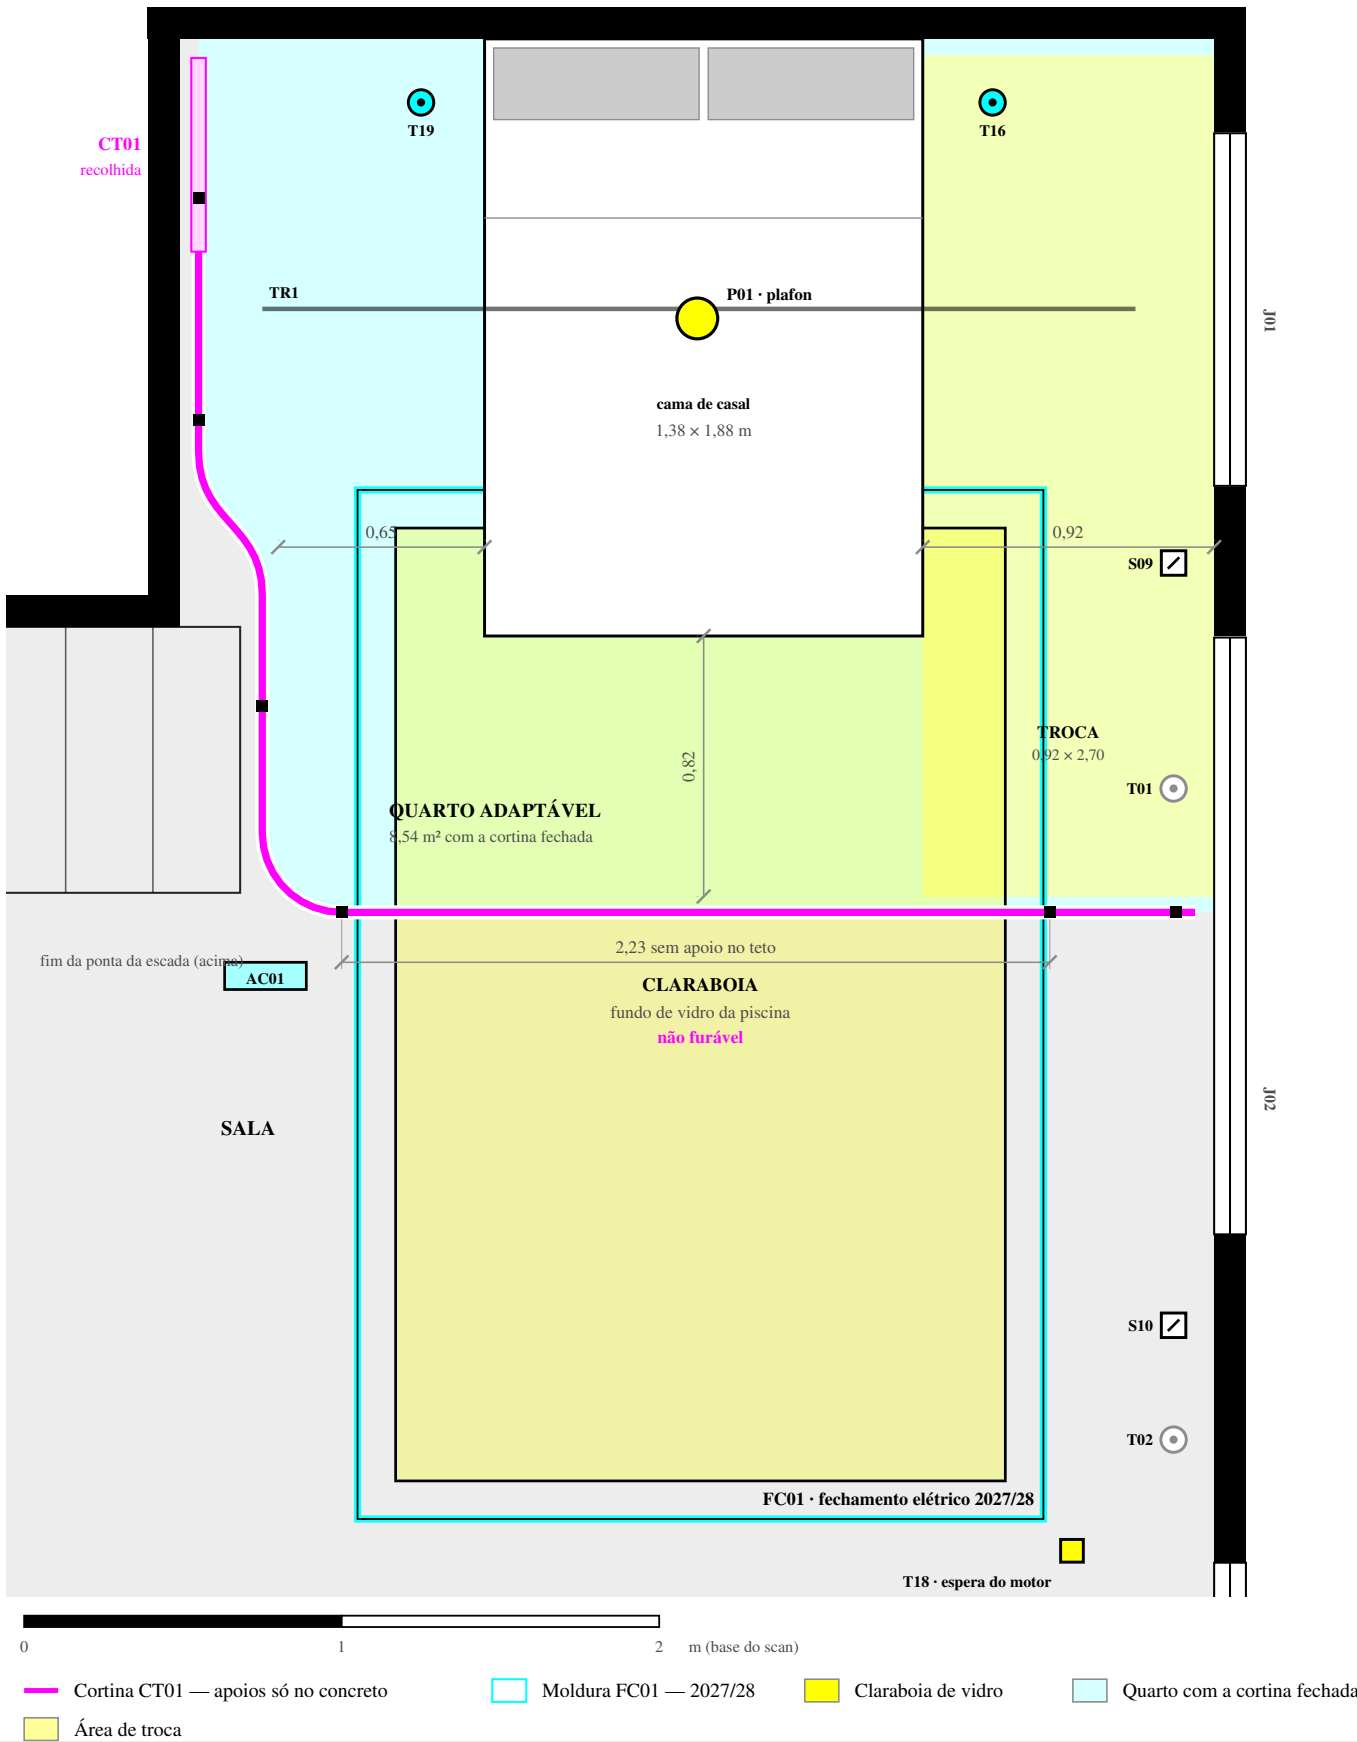

Circulação mínima adotada de 0,60 m em volta da cama; cortina com ~5 cm de tecido de cada lado do eixo do trilho. Medidas sobre o scan de 02.09.2026

O vidro da claraboia não recebe fixação. Apoios do trilho e da moldura só no concreto em volta, com posição confirmada em estrutura antes de furar.

ESTUDO PRELIMINAR — NÃO LIBERADO PARA EXECUÇÃO | 30/09/2026

QUARTO ADAPTÁVEL — NÚMEROS

Grandeza	Valor	Leitura
Área dentro da cortina	8,54 m²	jantar 5,90 m² + faixa da sala até a ponta da escada
Largura × profundidade	3,00 × 2,75 m	da cortina à fachada · da parede norte à cortina
Linha da cortina	2,85 m	da parede norte — 0,06 m além da ponta da escada
Trilho CT01	5,58 m	eixo, do canto do jantar à fachada leste
Cortina recolhida	~0,61 m de trilho	pacote no canto noroeste, junto à parede
Vão sem apoio no teto	2,23 m	sob a claraboia: perfil autoportante

CAMA x CIRCULAÇÃO — CABECEIRA NA PAREDE NORTE

Cama	Medida m	Lado cortina	Lado J01	Pé	Atende 0,60
Casal padrão	1,38 × 1,88	0,65	0,92	0,82	sim
Viúva	1,28 × 1,88	0,65	1,02	0,82	sim
Queen — referência	1,58 × 1,98	0,65	0,72	0,72	sim

ESCOPO — O QUE ENTRA AGORA E O QUE FICA PARA 2027/28

ID	Item	Fase
CT01	Trilho da cortina + perfil autoportante no trecho da claraboia	agora
CT02	Cortina de tecido, pé-direito inteiro — blackout a definir	agora
IN4	Eletroduto aparente e caixa de espera T18 junto à moldura	agora
IN5	Comando S10 com cabo guia até a espera	agora
MR1	Faixa de 0,12 m em volta do vidro reservada à moldura	agora
FC01	Fechamento elétrico da claraboia: moldura, motor e painel	2027/28
FC02	Ligação na espera T18 e programação do comando S10	2027/28

A cortina vira exatamente no fim da ponta da escada.

Recollida, fica no canto oroeste do xantar. Estendida, desce pola parede, desvía 0,20 m para contornar a lateral da escada, fai a curva no fim da punta e corre recta a 2,85 m da parede norte até a fachada. Ali a fachada é vidro (J02): a cortina encosta no caixilho — se a J02 tiver montante central, o trilho termina nele. Conferir en obra.

Com a linha na ponta da escada cabe cama de casal, com folga.

Cabeceira na parede norte, que é cega (divisa). Sobram 0,65 m do lado da cortina, 0,92 m do lado da J01 e 0,82 m no pé: os 0,60 m mínimos estão atendidos nos três lados. A faixa de 0,92 m junto à J01 é a área de troca de roupa. Viúva sobra mais; queen passa no limite.

Sob a claraboia o trilho não tem apoio no teto.

Entre 5,00 e 7,23 m são 2,23 m sem fixação — trilho comum pede apoio a cada ~1,0 m. Entra perfil autoportante (tubo metálico) fixado no concreto antes e depois da moldura, com o trilho preso nele; alternativa, cabo de aço tensionado. Confirmar com o fornecedor.

Fechamento elétrico: o equipamento é de 2027/28, a espera é de agora.

Com o teto aberto, eletroduto, caixa T18 e comando S10 com cabo guia custam pouco; depois da pintura custam abrir laje aparente e repintar. A moldura fixa na faixa de 0,12 m em volta do vidro — confirmar em estrutura se há viga de borda da piscina ali.

O que a cortina muda no resto do teto.

P01 passa a plafon, sobre a cama. AC01 sai da linha da cortina para 4,76 / 3,05 m: com a cortina fechada o quarto fica sem evaporadora própria. T16 e T19 são as tomadas das duas cabeceiras; S09 é paralelo da luz do jantar, no pilar entre J01 e J02.