


Opção A — cumaru-ferro, cozinha e closet em monolítico

Piso pronto em réguas nas áreas de estar e dormir; cozinha e closet numa zona monolítica contínua. Cores e desenho de régua ilustrativos.

norte 126° · Prancha 03 de 07

ponta arredondada: canto reto com filete de 0,70 m

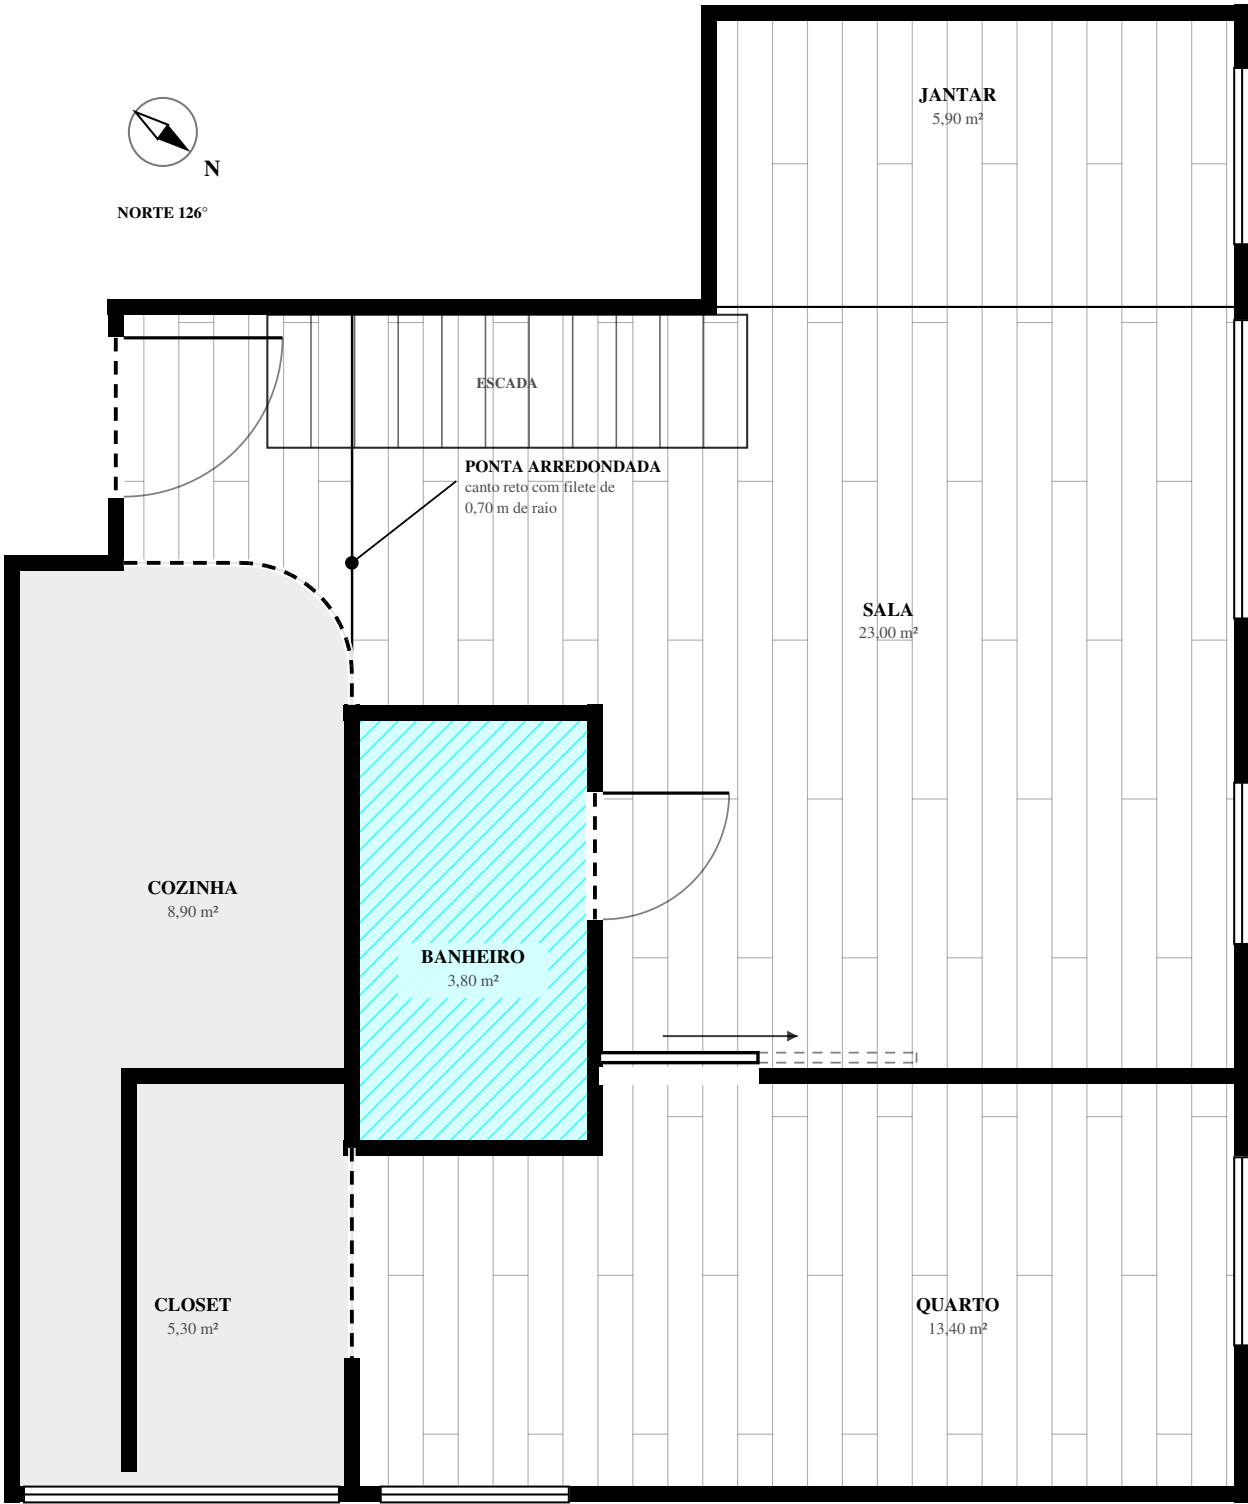

QUADRO DE ÁREAS

Sistema	Onde	Área
Cumaru-ferro	sala 23,00 + quarto 13,40 + jantar 5,90 + corredor 2,39	44,69 m²
+ reserva de 10%	cortes, perdas e reposição futura	49,16 m²
Monolítico	cozinha 6,51 (de 8,90) + closet 5,30 — zona contínua	11,81 m²
Banheiro	sistema à parte, área molhada, na mesma cota	3,80 m²
MainFloor	total do pavimento	60,30 m²

Cozinha e closet formam uma zona monolítica só.

A zona é um retângulo contínuo, da parede oeste até a linha da sala e do degrau até a fachada sul, passando pela abertura entre cozinha e closet. O corredor da entrada e a escada ficam em cumaru; o monolítico cobre a cozinha de trabalho e o closet.

A ponta é canto reto com filete de 0,70 m de raio.

Não é mais um arco achatado atravessando a cozinha: o limite corre reto pela linha do degrau, vira reto na linha da sala, e só a quina que aparece no corredor é arredondada. Um quarto de círculo tangente aos dois lados — geometria que o marceneiro e o aplicador sabem replicar com um compasso, e que o perfil de transição consegue acompanhar.

A junta é o detalhe mais caro desta opção.

Perfil de transição com junta de movimentação, reto nos trechos retos e curvo só no filete. E as duas espessuras têm de ser niveladas no contrapiso para se encontrarem rentes: régua pronta com manta e monolítico somam alturas diferentes, e é no contrapiso que se acerta a diferença, não na soleira.

Cumaru-ferro é madeira densa — o que é virtude e é risco.

Dureza e resistência altas, e por isso mesmo muito sensível a umidade e a base torta. Exige contrapiso seco, plano e nivelado (P06), aclimação das régua no ambiente antes de assentar e folga de dilatação em todo o perímetro, escondida no rodapé. Piso pronto reduz obra, mas não dispensa nenhuma dessas três condições.

O desenho das régua é hipótese, não especificação.

Régua de 0,22 m correndo norte-sul, paralelas ao lado maior do pavimento, com topos a cada 3,00 m defasados de um terço. Largura, comprimento e sentido de assentamento são decisão de projeto: o sentido muda a leitura do espaço e a percepção do desnível do contrapiso.

O banheiro fica fora dos dois sistemas, mas na mesma cota.

Sistema próprio, com impermeabilização, caimento e acabamento antiderrapante, nivelado com o piso seco (P05): a soleira é junta de material, não degrau. Sem degrau, ralo linear e fecho de vidro assumem a contenção de água.