


Quadro de esquadrias e dados do levantamento

Todas as esquadrias na mesma escala. Alturas conforme medição do cliente; larguras do scan. Vão livre, não marco: conferir antes de fabricar.

seis janelas · três portas
peitoril, sentido de abertura e material a levantar

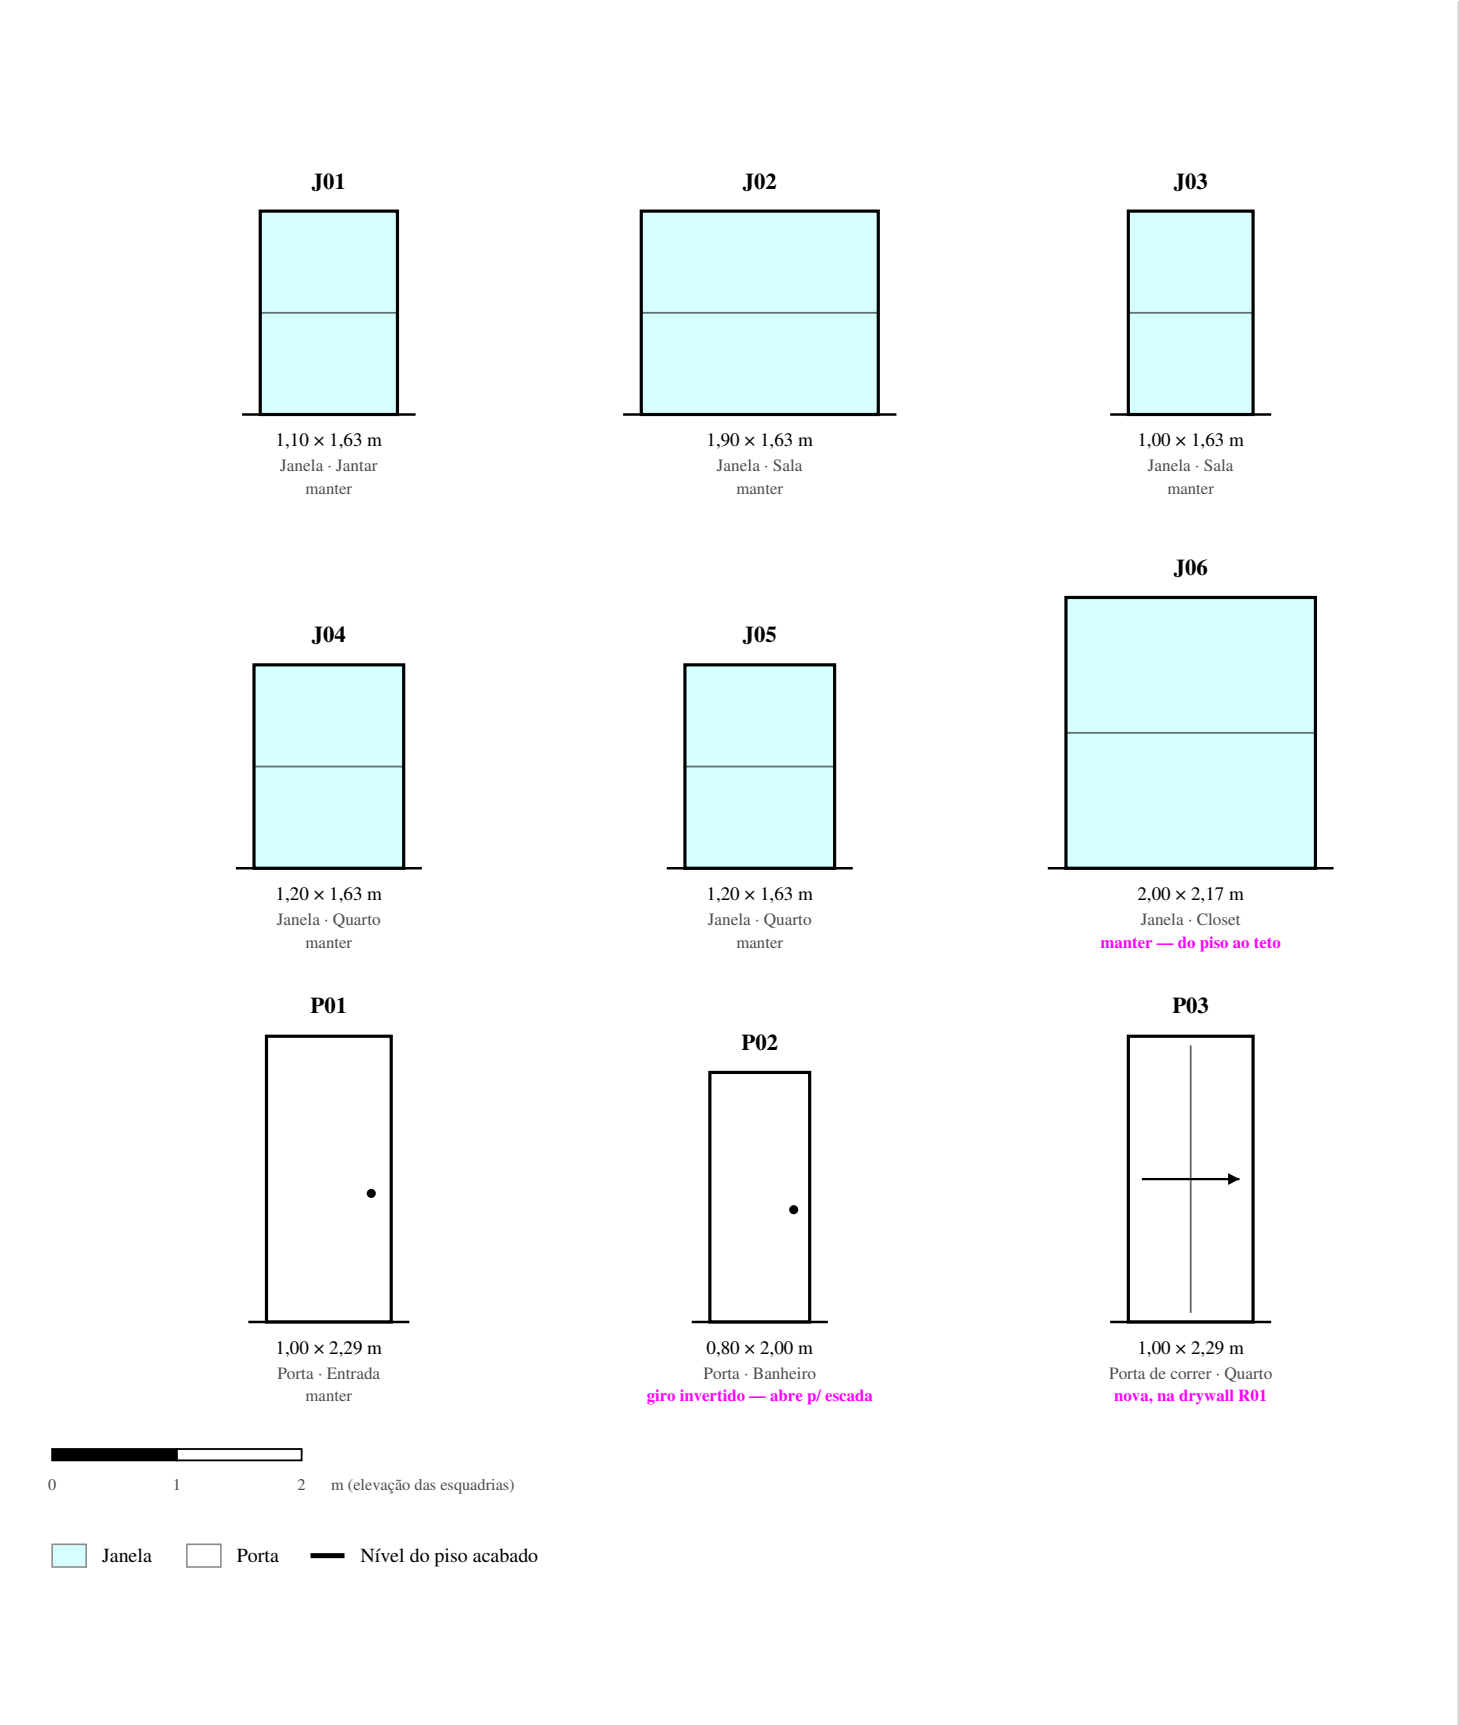

DADOS DO LEVANTAMENTO		
Dado	Valor	Observação
Área útil (soma dos ambientes)	60,30 m²	relatório arredonda para 60,20
Área externa do pavimento	64,70 m²	inclui espessura de paredes
Área de parede	130,40 m²	sem vãos
Área de esquadria	14,77 m²	seis janelas, vão — scan dava 12,70
Volume	144,51 m³	com forro; ~158 m³ na laje aparente
Perímetro somado dos ambientes	78,10 m	não é perímetro do pavimento
Pé-direito — laje	2,62 m	depois de retirar o forro (D07)
Pé-direito — forro atual	2,42 m	plenum de 0,20 m
Captura / exportação	02.09 / 07.09.2026	scan 3D Polycam
Coordenadas	23°36'46,8"S 46°44'15,8"O	altitude 822 m — do scan superior
Norte	126°	do topo da folha, sentido horário

INVENTÁRIO DO SCAN — NÃO É ESPECIFICAÇÃO

Ambiente	Itens reconhecidos pelo scan (m)
Sala	sofá 2,60 × 1,60 · mesa de centro 1,60 × 1,00 · 3 cadeiras · armário 2,50 × 0,40 · escada 0,80 × 3,00
Quarto	cama 1,50 × 2,00 · bancada 3,00 × 0,50 · mesa 0,50 × 0,50 · cadeira
Cozinha	armário 1,60 × 0,60 · cuba 0,70 × 0,60 · geladeira 0,90 × 0,80 (h 1,80) · forno · cooktop · lava-louças
Jantar	armário de canto 2,50 × 0,40 — o canto alemão, item D05 da demolição
Closet	marcenaria não discriminada pelo scan — inventariar módulo a módulo antes de desmontar (M01)
Banheiro	bancada 1,70 × 0,40 · box 0,90 × 1,40 (h 2,10) · cuba 0,60 × 0,50 · bacia 0,40 × 0,70

Todas na mesma escala. Largura × altura de vão livre, não de marco.

Peitoril, sentido de abertura e material não estão medidos: as três informações precisam de visita. Nenhuma esquadria deste caderno está liberada para fabricação.

As alturas das janelas vieram do cliente, não do scan.

Cinco têm 1,63 m. A do closet (J06) vai do piso ao teto; 2,42 m de altura livre menos 0,15 m de apoio no topo e 0,10 m de peitoril, dando 2,00 × 2,17 m — e é o único peitoril medido até agora. As duas do quarto ficam idênticas, e a área de esquadria sobe de 12,70 para 14,77 m².

P03 é a única esquadria nova.

Porta de correr de 1,00 × 2,29 m na drywall reconstruída, com a folha estacionando no 1,00 m de parede a leste do vão, pela face da sala. P02 mantém a folha existente de 0,80 × 2,00 m e só inverte o giro. P01, a porta de entrada, mede 1,00 × 2,29 m e não é alterada.

O inventário do scan serve para escopo, não para especificação.

É o que o algoritmo reconheceu no dia da captura. Há erro evidente — uma "mesa lateral" de 6,60 × 2,00 m que é a projeção da escada — e há ausência: o closet inteiro não foi discriminado. Use a lista para conferir o que sai, o que se desmonta e o que volta.

O que este caderno ainda não tem, e que um executivo exige:

projeto estrutural para a furação da laje e a área da piscina; hidráulica e esgoto do banheiro e da cozinha; elétrico executivo com diagrama unifilar e cálculo de demanda; projeto de juntas do piso monolítico; detalhamento de marcenaria; e aprovação do condomínio.