
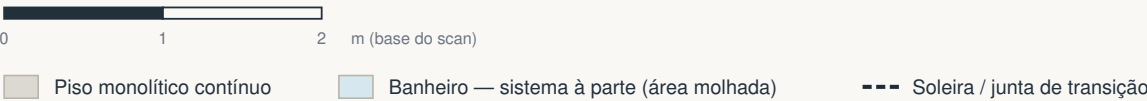


Piso monolítico

Sistema único em todo o MainFloor, com o banheiro à parte. Cores ilustrativas; nenhum produto, espessura ou acabamento especificado.

proposta de cumaru encerrada

piso contínuo — sem junta de material entre ambientes secos

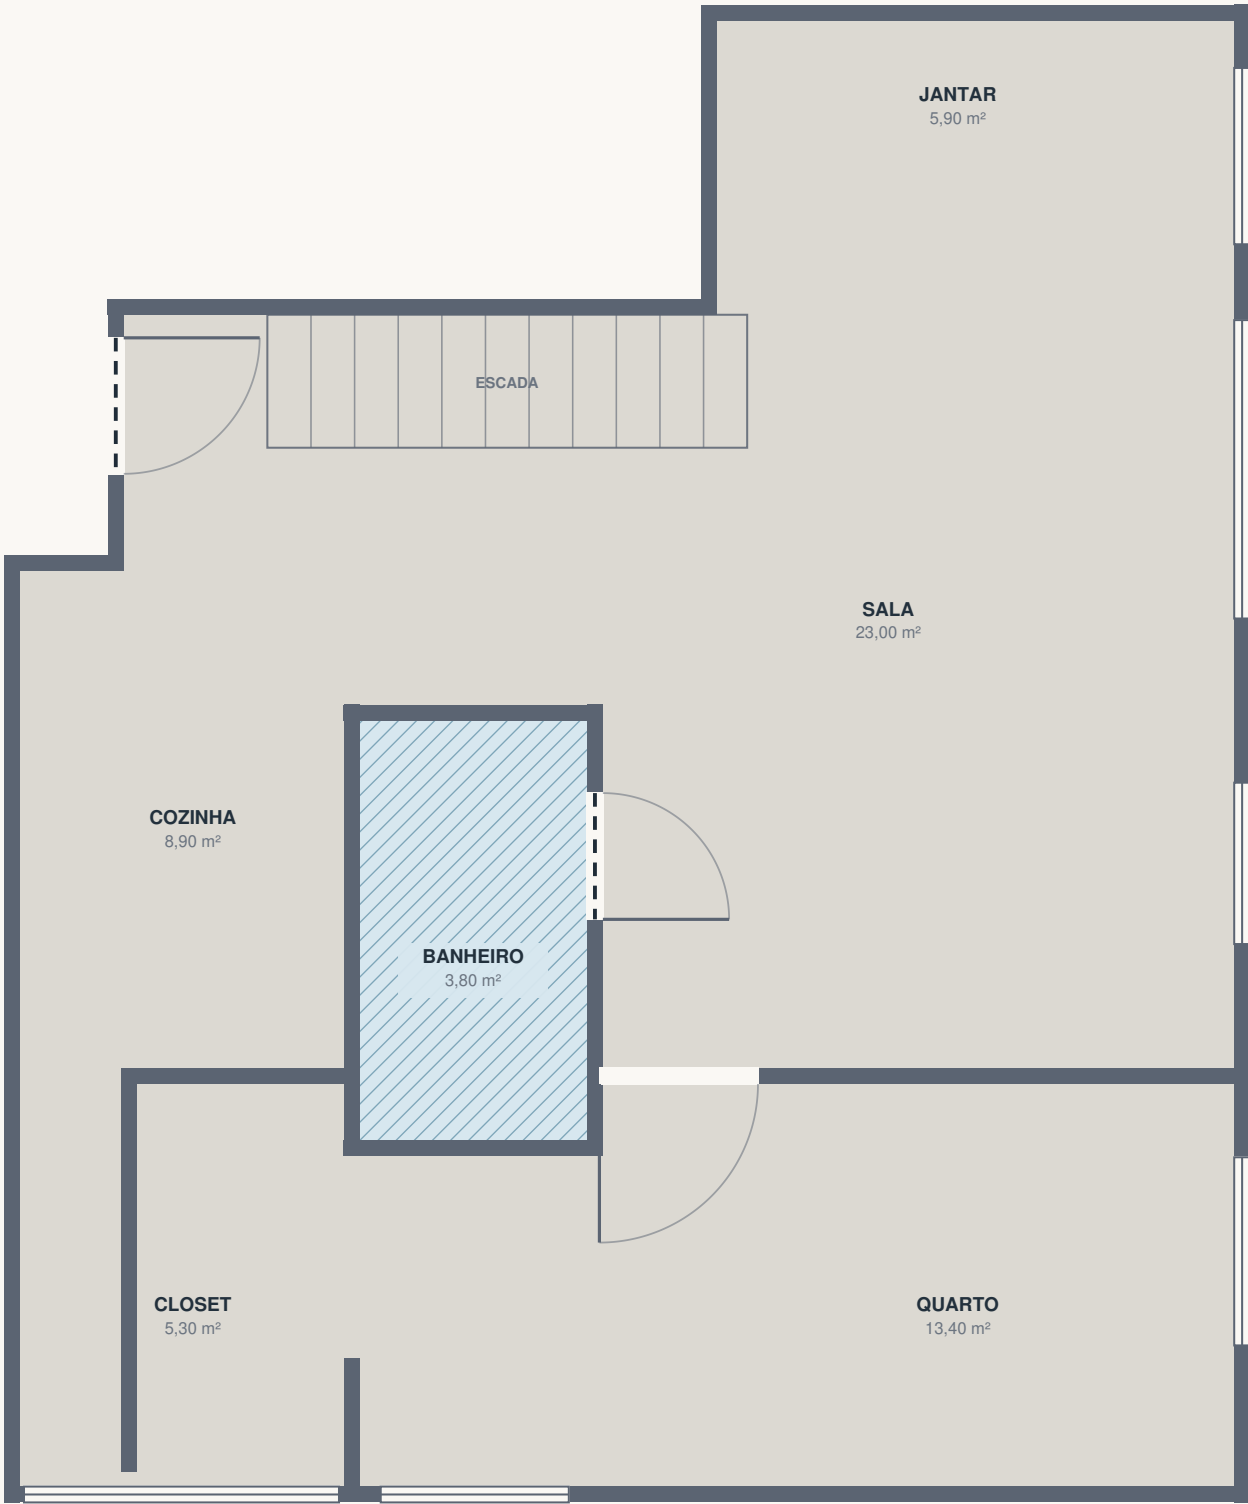

QUADRO DE ÁREAS

Ambiente	Sistema	Área
Sala	monolítico contínuo	23,00 m²
Quarto	monolítico contínuo	13,40 m²
Cozinha	monolítico contínuo	8,90 m²
Jantar	monolítico contínuo	5,90 m²
Closet	monolítico contínuo	5,30 m²
Monolítico — total	cinco ambientes, sem junta de material	56,50 m²
Banheiro	sistema à parte, área molhada	3,80 m²
MainFloor	total do pavimento	60,30 m²

Um sistema só, sem junta de material entre os ambientes secos.
Com o cumaru fora, a ponta em curva da cozinha perde a função: ela existia apenas para resolver o encontro entre a madeira e o monolítico. O piso corre contínuo da entrada ao quarto, e as únicas transições que sobram são a soleira do banheiro e a da porta de entrada.

Juntas de movimentação são projeto, não improvisado de obra.
Monolítico contínuo em 56,50 m² trabalha: prever juntas conforme o sistema escolhido, nos vãos de porta e nos encontros com a estrutura. Posição e desenho entram no executivo, junto com o fornecedor — uma trinca num piso sem junta não tem remendo invisível.

A base manda no resultado.
Depois de retirar os pisos existentes (D08), conferir nível, aderência, umidade e fissuras do contrapiso em toda a extensão. Espessura, sistema e acabamento ainda não estão especificados: cor e textura do desenho são ilustrativas.

O banheiro fica fora do monolítico.
Sistema próprio, com impermeabilização, caimento para o ralo e acabamento antiderrapante. Com o piso demolido, conferir o rebaixo da laje; a impermeabilização precisa subir também na parede nova do fundo do box (R02).

Encontro com a parede.
Rodapé embutido, negativo ou pintura direta mudam o preparo das paredes e o corte do piso: definir antes de a empreiteira fechar o preparo para pintura.

Sequência importa mais que no piso em régua.
O monolítico entra depois das paredes prontas e antes da marcenaria: o closet (M01) só volta depois do piso curado. Prever tempo de cura e proteção da superfície até o fim da obra.

Sem reserva de corte.
Aplicação moldada in loco não tem perda de régua, mas isso não é margem zero: prever retrabalho de textura e acerto de bordas. Os degraus da escada estão fora da conta; o piso sob a escada permanece.