

Planta baixa cotada — estado proposto

Folha de referência dimensional. Cotas em metros, sobre o levantamento por scan de 02.09.2026; conferir em campo antes de qualquer medição.

norte 126° — medido pela rosa do pavimento superior

pé-direito 2,62 m na laje · 2,40 m com o forro atual

QUADRO DE AMBIENTES — LEVANTAMENTO (m, m²)

Ambiente	Área	Perímetro	Bounding box	Inscrita
Sala de TV	23,00 m²	20,7 m	5,6 × 4,8	4,8 × 4,0
Quarto	13,40 m²	16,2 m	5,6 × 2,5	5,6 × 2,1
Cozinha	8,90 m²	13,7 m	4,7 × 2,1	4,7 × 1,4
Sala de estar	5,90 m²	10,1 m	3,3 × 1,8	—
Closet	5,30 m²	9,3 m	2,5 × 2,1	—
Banheiro	3,80 m²	8,1 m	2,6 × 1,4	—
MainFloor	60,30 m²	78,1 m	7,85 × 9,43	—

Como esta planta foi levantada.

Scan 3D Polycam, captura de 02.09.2026, relatório exportado em 07.09.2026. Paredes, vãos e polígonos de ambiente foram lidos do vetor do arquivo em pontos PDF e convertidos pela escala 45,66 pt/m, conferida duas vezes contra as cotas gerais: 358,33 pt / 7,85 m e 430,56 pt / 9,43 m. O próprio relatório avisa que são estimativas — nenhuma cota aqui substitui medição em campo.

Pé-direito: 2,40 m com o forro atual, 2,62 m na laje.

Alturas informadas pelo cliente; o relatório do scan mede 2,40 m com forro, o que confere. Com a retirada total do forro (D07) ganham-se os 0,22 m de plenum. É essa folga que acomoda a porta de correr de 2,29 m: sob o forro de hoje sobriariam 0,13 m, e sobre a laje sobram 0,33 m — espaço para o trilho aparente. Volume passa de 144,51 m³ para cerca de 158 m³ com a laje aparente.

Espessuras e níveis: uma cota única para o pavimento.

Todas as paredes lidas no scan têm 0,10 m. A nova drywall (R01) repete a espessura, salvo se o trilho da porta de correr for embutido em cassete — aí a parede engrossa. O banheiro passa a nascer na mesma cota do piso seco (P05), sem degrau de soleira, e todo o contrapiso é lixado e nivelado (P06): ±0,00 é o piso acabado atual, e o nível final precisa ser amarrado ao hall.

Diferença entre as áreas do relatório.

Área externa 64,70 m² (inclui paredes), área útil 60,20 m² pelo relatório e 60,30 m² pela soma dos seis ambientes — a diferença é arredondamento. O caderno usa 60,30 m². Área de parede 130,40 m², área de janela 12,70 m², perímetro somado dos ambientes 78,10 m.

Bounding box não é o ambiente.


As dimensões do relatório vêm em duas leituras: o menor retângulo que contém o ambiente (B) e o maior retângulo inscrito (I). Em planta irregular — sala de TV e cozinha — as duas divergem bastante: usar a inscrita para conferir mobiliário e a cotada em planta para obra.

O norte foi medido, não arbitrado: 126° do topo da folha.

O relatório do pavimento superior — mesma captura — traz rosa dos ventos e GPS; o do MainFloor não traz nenhum dos dois. As duas plantas estão desenhadas com 180° de diferença, confirmado por dois elementos que os pavimentos compartilham: a caixa da escada e a área da piscina, que só cai no terraço de cima com essa rotação. A pétala N do Upfloor marca −53,97°; somados 180°, dá 126°.

As duas fachadas envidraçadas dão para NOROESTE e NORDESTE.

Noroeste: sala de estar (J01), sala de TV (J02 e J03) e uma janela do quarto (J04) — é a face que toma o sol de tarde, o mais quente. Nordeste: a outra janela do quarto (J05) e o closet (J06), sol de manhã. As outras duas faces são divisa, a sudeste e a sudoeste. Coordenadas do levantamento: 23°36'46,8"S 46°44'15,8"O, altitude 822 m.

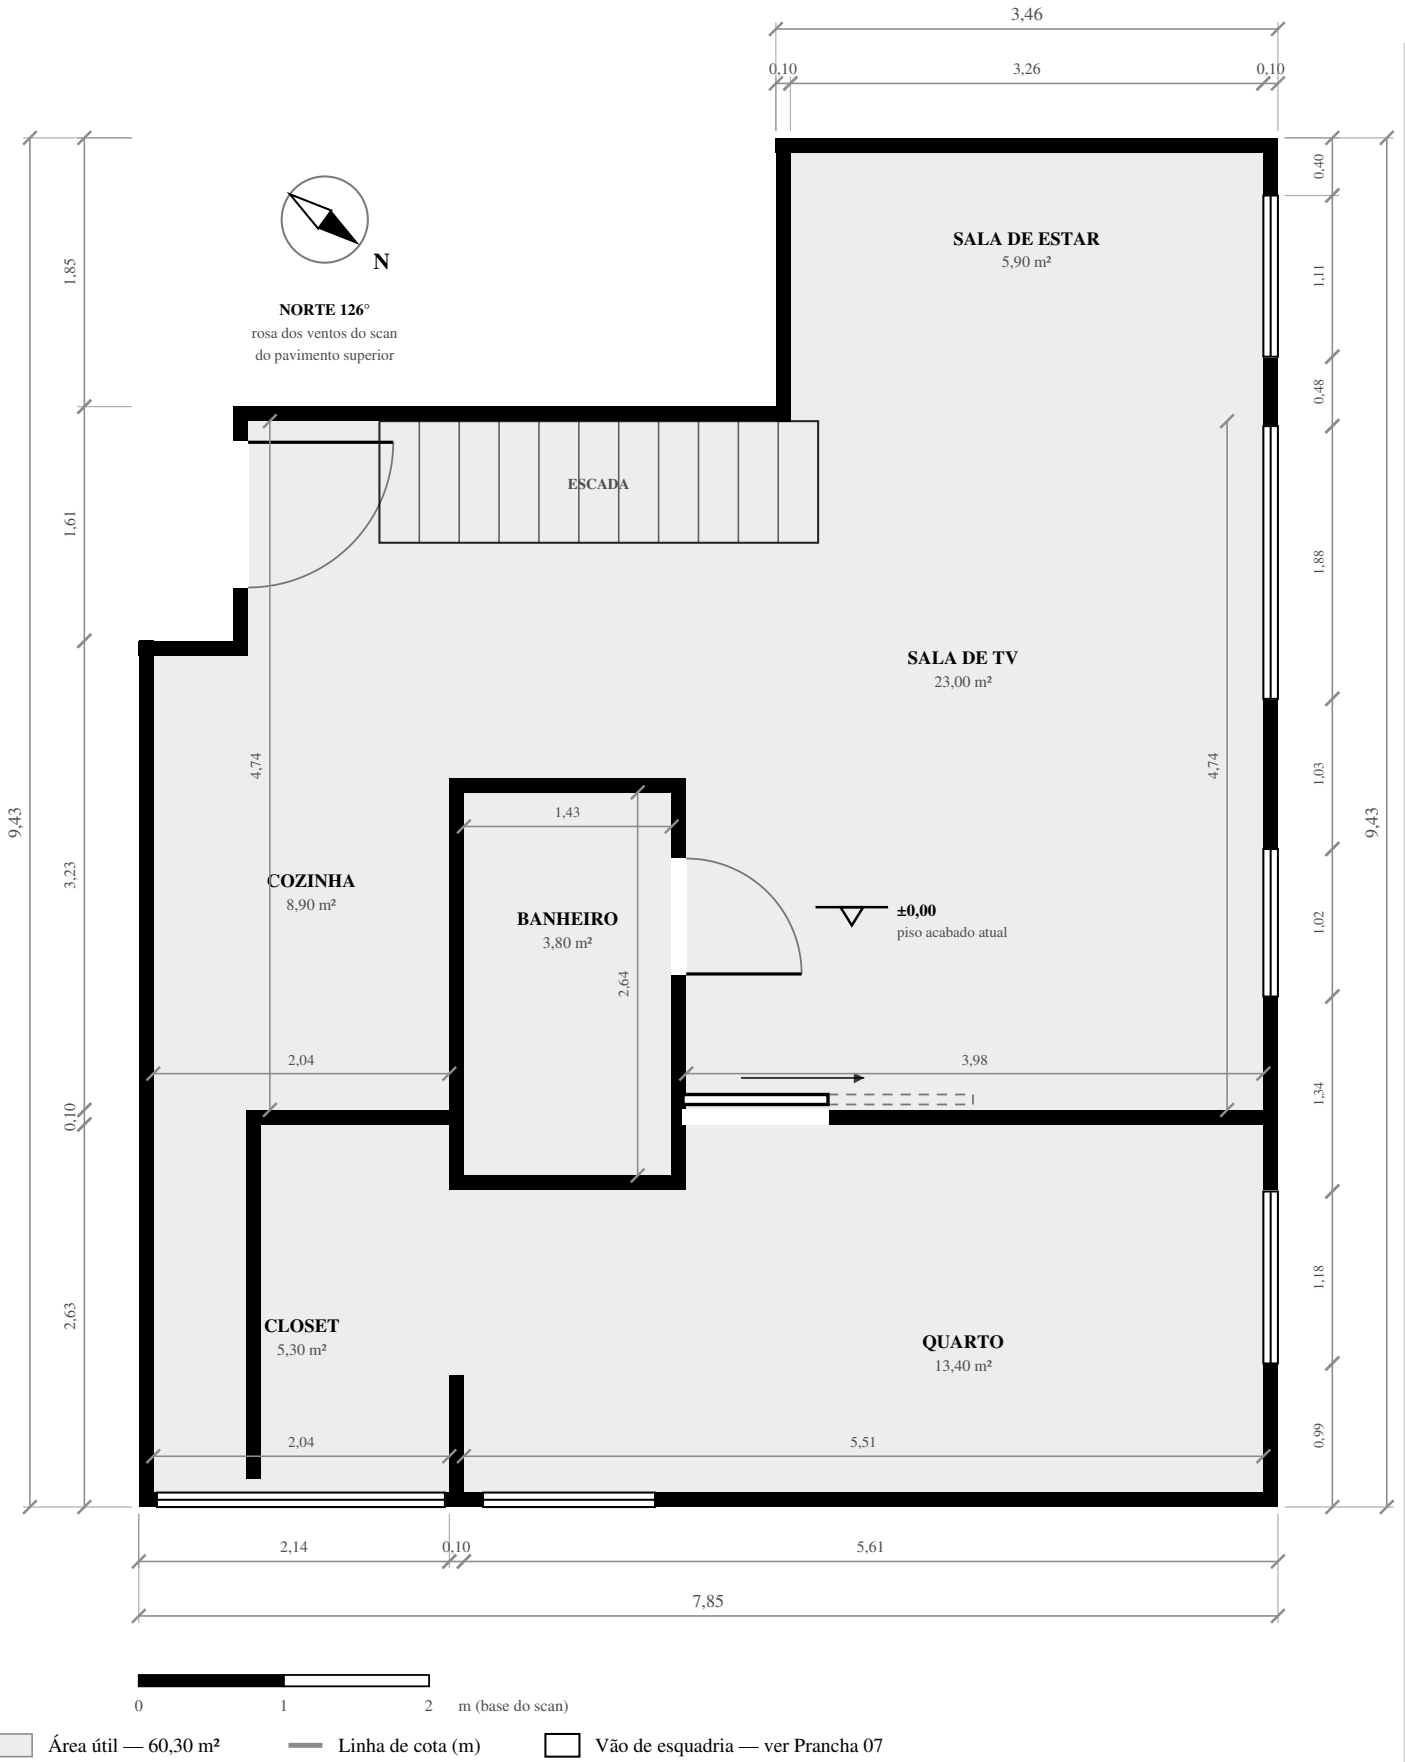

Cotas extraídas do modelo do scan e arredondadas ao centímetro. O relatório do levantamento declara que os valores são estimativas: conferir em campo antes de fabricar esquadria, marcenaria ou bancada. Planta de estudo preliminar. Não é planta executiva liberada: faltam projeto estrutural, hidráulica, elétrico executivo e aprovação do condomínio.