


Opção B — monolítico em todo o MainFloor

Sistema único nos cinco ambientes secos, com o banheiro à parte. Cores ilustrativas; nenhum produto, espessura ou acabamento especificado.

norte 126° · Prancha 04 de 13

piso contínuo — sem junta de material entre ambientes secos

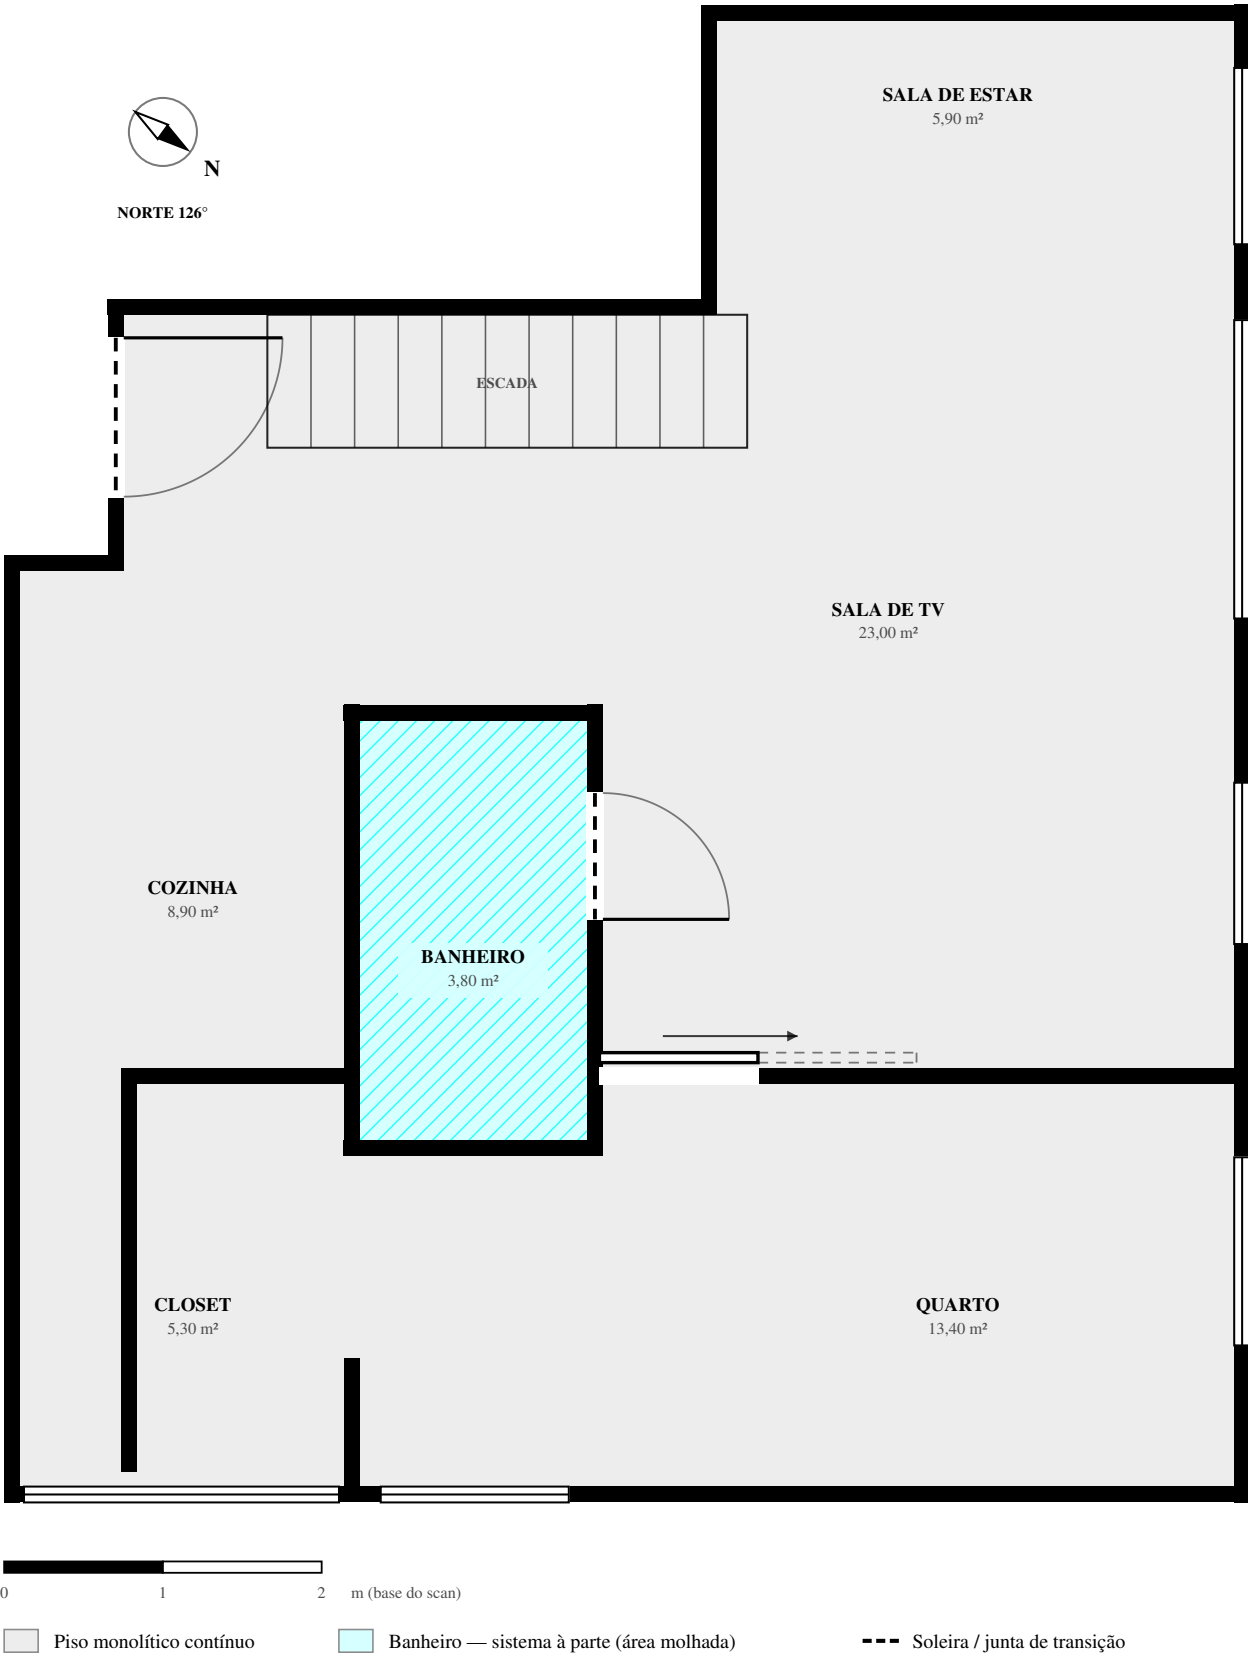

QUADRO DE ÁREAS

Sistema	Onde	Área
Monolítico	sala de TV, quarto, cozinha, sala de estar e closet — sem junta de material	56,50 m²
Sem reserva	aplicação moldada in loco, sem perda de corte	—
Banheiro	sistema à parte, área molhada, na mesma cota	3,80 m²
MainFloor	total do pavimento	60,30 m²

Um sistema só, sem junta de material entre os ambientes secos.

O piso corre contínuo da entrada ao quarto. Não há curva porque não há encontro de materiais: a ponta em curva da cozinha só existe na opção A. As únicas transições são a soleira do banheiro — sem degrau — e a da porta de entrada.

Contínuo não quer dizer sem junta — e quantas juntas depende do sistema.

Cimentício (cimento queimado, concreto polido, autonivelante aparente) retrai ao curar e acompanha o movimento da laje: trabalha em painéis de 3 a 6 m de lado, próximos do quadrado, o que dá de 4 a 8 juntas nos 56,50 m². Microcimento de 2 a 3 mm, com tela e primer, reduz as juntas às do substrato e à dessolidarização de perímetro. Resina epóxi ou poliuretano fecha contínuo de verdade, mas tem cara de resina e não de concreto.

Três juntas são obrigatórias em qualquer sistema.

Sobre junta estrutural ou linha de viga, porque ali a laje se move e o acabamento trinca se for contínuo. No perímetro, para o pano poder trabalhar sem romper no canto — fica escondida no rodapé. E na parada de concretagem, onde a aplicação do dia terminou. A boa notícia: a casa já tem lugares naturais para elas — a soleira da entrada, a do banheiro e a linha da porta de correr entre sala de TV e quarto.

Peça a paginação de juntas junto com a proposta, antes de assinar.

Quem desenha as juntas escolhe onde a trinca vai aparecer; quem não desenha deixa o material escolher. Fornecedor que promete 56,50 m² sem nenhuma junta ou está propondo resina, ou não vai entregar o que prometeu — trinca em piso monolítico não tem remendo invisível.

A base manda no resultado — o monolítico copia o que está embaixo.

Depois de retirar os pisos (D08), todo o contrapiso é lixado, regularizado e nivelado (P06), com conferência de aderência, umidade e fissuras. Espessura, sistema e acabamento ainda não estão especificados: cor e textura do desenho são ilustrativas.

O banheiro fica fora do monolítico, mas na mesma cota.

Sistema próprio, com impermeabilização, caimento e acabamento antiderrapante, nivelado com o piso seco (P05). Sem degrau, ralo linear e fecho de vidro assumem a contenção de água, e a impermeabilização sobe também na parede nova do fundo do box (R02).

Sequência importa mais que no piso em régua.

O monolítico entra depois das paredes prontas e antes da marcenaria: o closet (M01) só volta depois do piso curado. Prever tempo de cura e proteção da superfície até o fim da obra.