Quarto adaptável e fechamento da claraboia

A cortina fecha a sala de estar como quarto de hóspede; a claraboia ganha fechamento elétrico em 2027/28, com a infraestrutura feita agora.

cama de casal com 0,60 m de circulação nos três lados

8,78 m² dentro da cortina · claraboia não furável

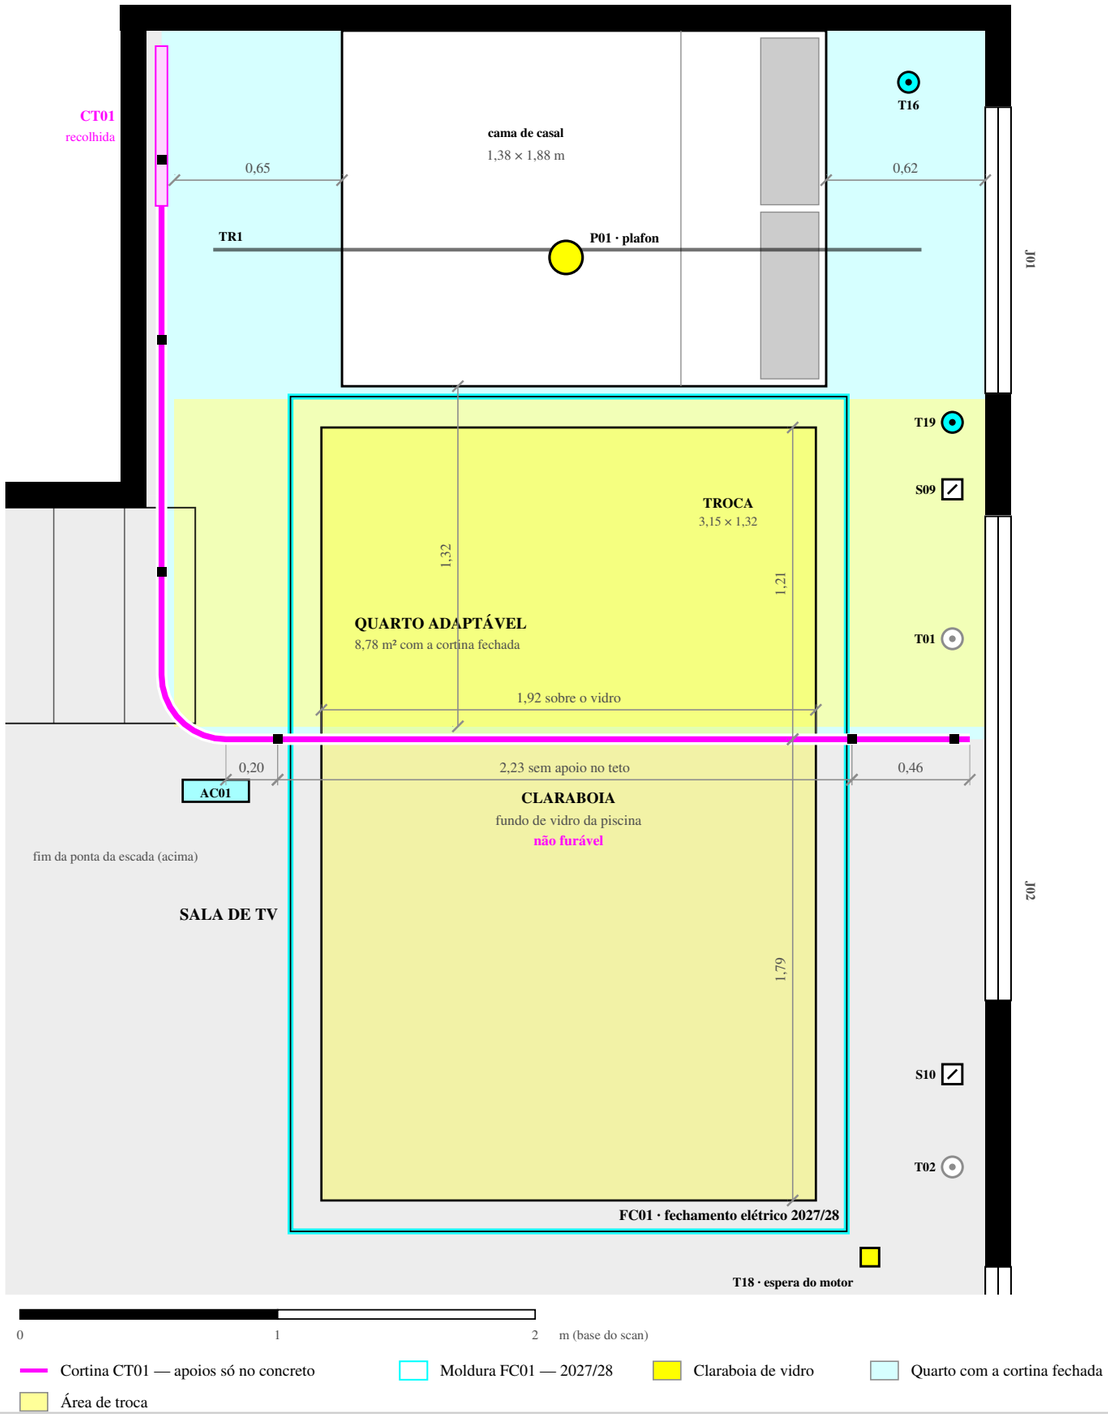

QUARTO ADAPTÁVEL — NÚMEROS

Grandeza	Valor	Leitura
Área dentro da cortina	8,78 m²	sala de estar 5,90 m² + faixa da sala de TV até a ponta da escada
Largura × profundidade	3,20 × 2,75 m	da cortina à fachada · da parede norte à cortina
Linha da cortina	2,85 m	da parede norte — 0,06 m além da ponta da escada
Cortina recolhida	~0,62 m de trilho	pacote no canto noroeste, junto à parede

CAMA × CIRCULAÇÃO — LESTE–OESTE, JUNTO À PAREDE NORTE

Cama	Medida m	Pé oeste	Cabeceira	Lado sul	Atende 0,60
Casal padrão	1,38 × 1,88	0,65	0,62	1,32	sim
Viúva	1,28 × 1,88	0,65	0,62	1,42	sim
Queen — referência	1,58 × 1,98	0,60	0,57	1,12	no limite

ESCOPO — O QUE ENTRA AGORA E O QUE FICA PARA 2027/28

ID	Item	Fase
CT01	Trilho da cortina + perfil autoportante no trecho da claraboia	agora
CT02	Cortina de tecido, pé-direito inteiro — blackout a definir	agora
IN4	Eletroduto aparente e caixa de espera T18 junto à moldura	agora
IN5	Comando S10 com cabo guia até a espera	agora
MR1	Faixa de 0,12 m em volta do vidro reservada à moldura	agora
FC01	Fechamento elétrico da claraboia: moldura, motor e painel	2027/28
FC02	Ligação na espera T18 e programação do comando S10	2027/28

TRILHO CT01 — MEDIDAS NO EIXO, A PARTIR DO CANTO NOROESTE

Trilho CT01 — trecho	De – até (m)	Medida
Descida rente à parede oeste (x 4,55)	y 0,16 a 2,60	2,44 m
Curva no fim da ponta da escada, R 0,25	y 2,60 a x 4,80	0,39 m
Reta até o último apoio antes da claraboia	x 4,80 a 5,00	0,20 m
Vão sob a claraboia, sem apoio — perfil PF1	x 5,00 a 7,23	2,23 m
· dentro do vão: faixa da moldura FC01	x 5,05 a 7,21	2,16 m
· dentro do vão: sobre o vidro	x 5,17 a 7,09	1,92 m
Do apoio leste até a fachada (J02)	x 7,23 a 7,69	0,46 m
Total do eixo CT01	do canto noroeste à fachada	5,72 m
Linha sob o vidro, a y 2,85	borda norte 1,64 · sul 4,64	1,21 / 1,79 m
Apoios AP, só no concreto	y 0,60 · 1,30 · 2,20 · x 5,00 · 7,23 · 7,63	6 pontos

Trilho reto, com uma curva só, no fim da ponta da escada.
Desce rente à parede, passa sobre o degrau, vira e corre a 2,85 m da parede norte até a J02. Se a J02 tiver montante central, o trilho termina nele. Cama e folgas: ver a tabela acima.

Sob a claraboia: 2,23 m sem fixação, do apoio x 5,00 ao x 7,23.
Trilho comum pede apoio a cada ~1,0 m: perfil autoportante PF1 (tubo metálico) no concreto antes e depois da moldura, com o trilho preso nele — ou cabo de aço tensionado. Medidas sobre o scan: conferir vidro e moldura em obra antes de cortar o perfil.

Fechamento elétrico: o equipamento é de 2027/28, a espera é de agora.
Eletroduto, caixa T18 e comando S10 com cabo guia entram com o teto aberto. A moldura fixa na faixa de 0,12 m em volta do vidro — confirmar se há viga de borda da piscina ali.

Circulação mínima adotada de 0,60 m em volta da cama; cortina com ~5 cm de tecido de cada lado do eixo do trilho. Medidas sobre o scan de 02.09.2026.
O vidro da claraboia não recebe fixação. Apoios do trilho e da moldura só no concreto em volta, com posição confirmada em estrutura antes de furar.