


# Planta proposta cotada

MainFloor completo, com a parede cozinha/closet na posição nova. Demais ambientes sem alteração.

cozinha 9,82 m² · closet 4,38 m²

mesma base do scan — REV. M

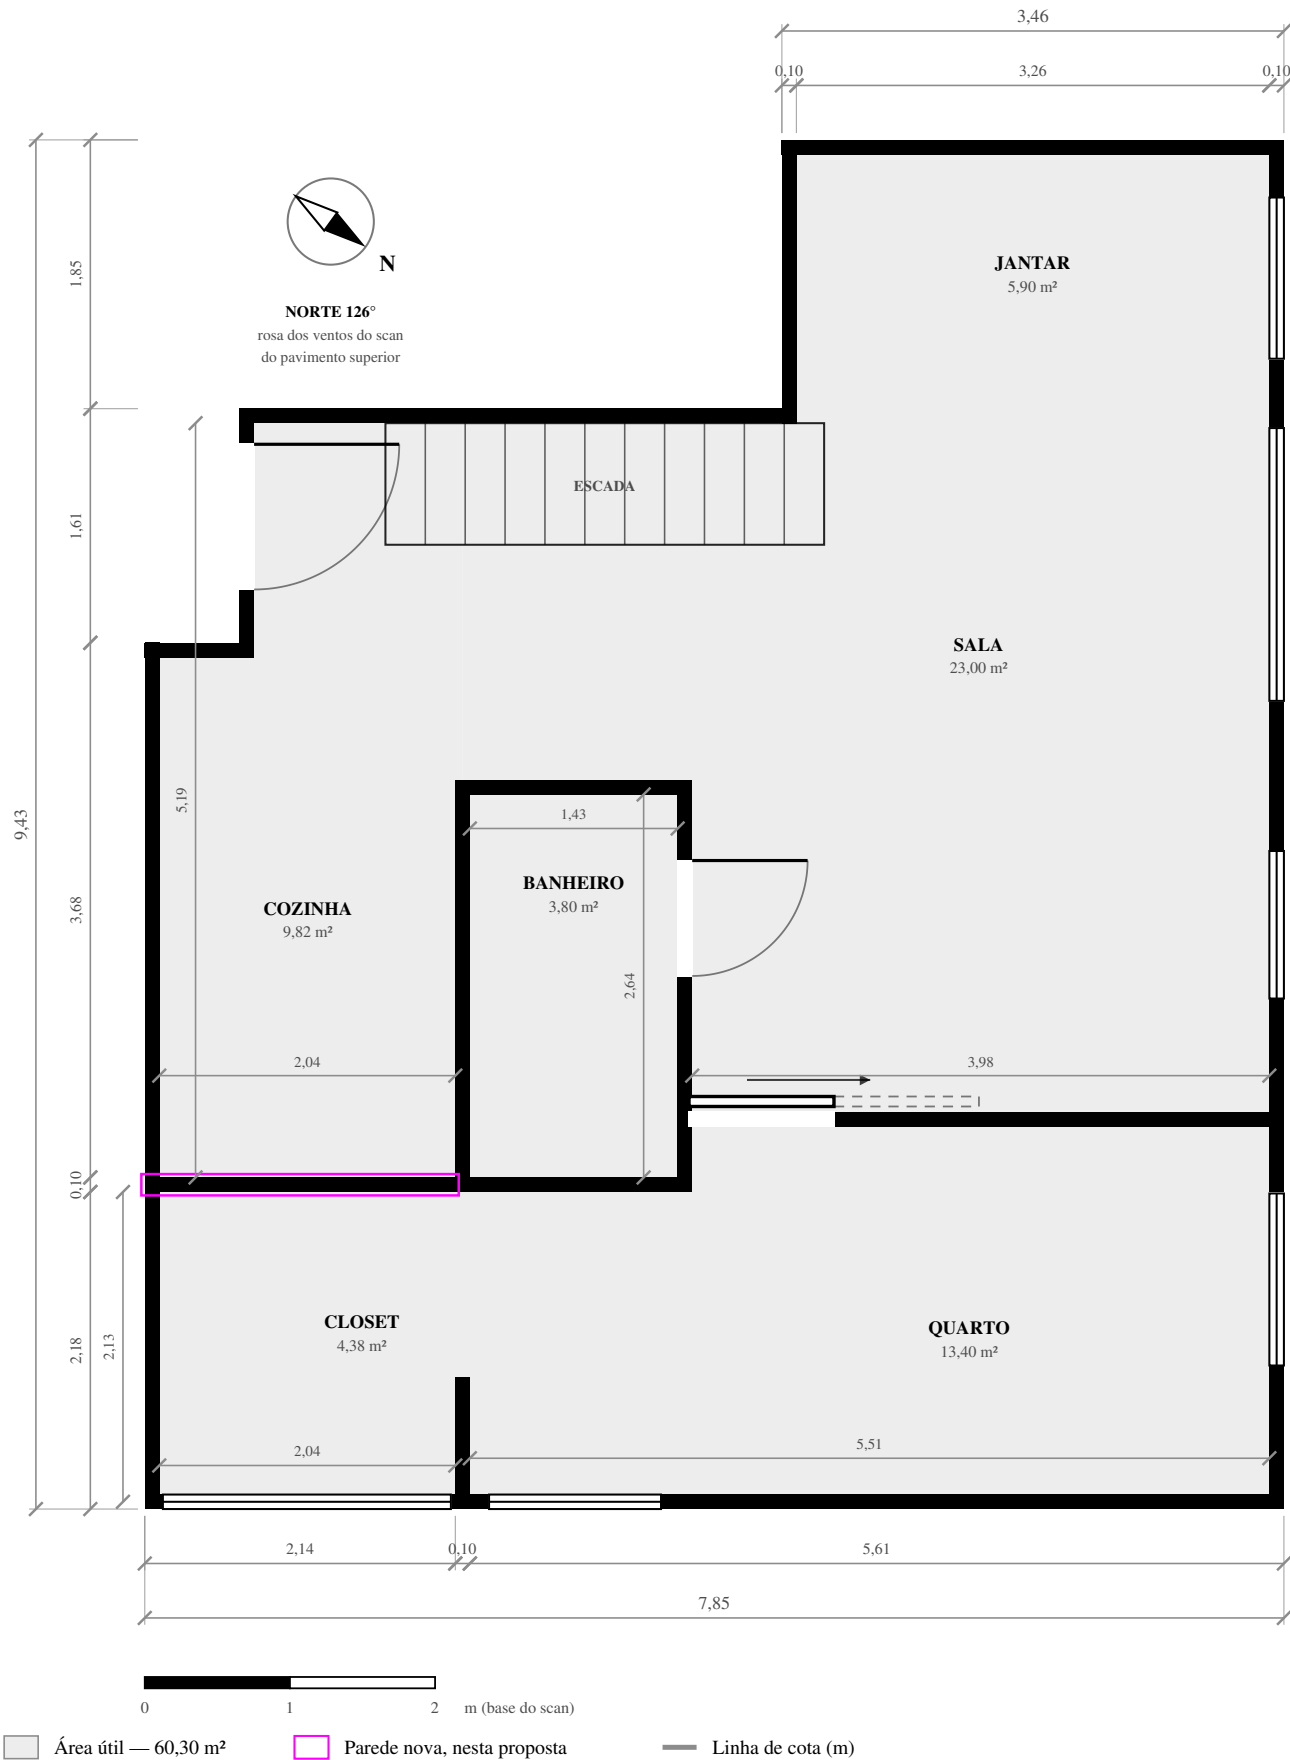

## COMPARATIVO DE ÁREAS

| Ambiente          | Área atual | Área nesta proposta | Diferença    |
|-------------------|------------|---------------------|--------------|
| Cozinha           | 8,90 m²    | 9,82 m²             | +0,92 m²     |
| Closet            | 5,30 m²    | 4,38 m²             | −0,92 m²     |
| Soma das duas     | 14,20 m²   | 14,20 m²            | sem variação |
| MainFloor — total | 60,30 m²   | 60,30 m²            | sem variação |

### Só duas salas mudam de área.

Sala, quarto, jantar e banheiro seguem exatamente como na REV. M — mesmas cotas, mesmas esquadrias, mesma numeração de portas e janelas.

### A largura interna comum não muda.

Cozinha e closet continuam com 2,04 m de largura livre — a mesma parede externa oeste e a mesma parede do banheiro/quarto os limitam dos dois lados. Só a parede que os separa entre si é que se move.

### J06, a janela do closet, não é afetada.

Fica na parede sul (fachada), que esta alteração não toca. A profundidade do closet diminui pelo lado norte — o vão da janela permanece o mesmo.

Cotas extraídas do modelo do scan e arredondadas ao centímetro, com a parede cozinha/closet na posição desta proposta. Planta de estudo. Substitui a Prancha 01 apenas nesta proposta alternativa — a REV. M segue como está.