


Piso — opção A, cumaru-ferro + monolítico

Piso pronto em réguas nas áreas de estar e dormir; cozinha e closet numa zona monolítica contínua — sem mudança nesta zona.

norte 126° · Alt A · 05

ponta arredondada: canto reto com filete de 0,70 m

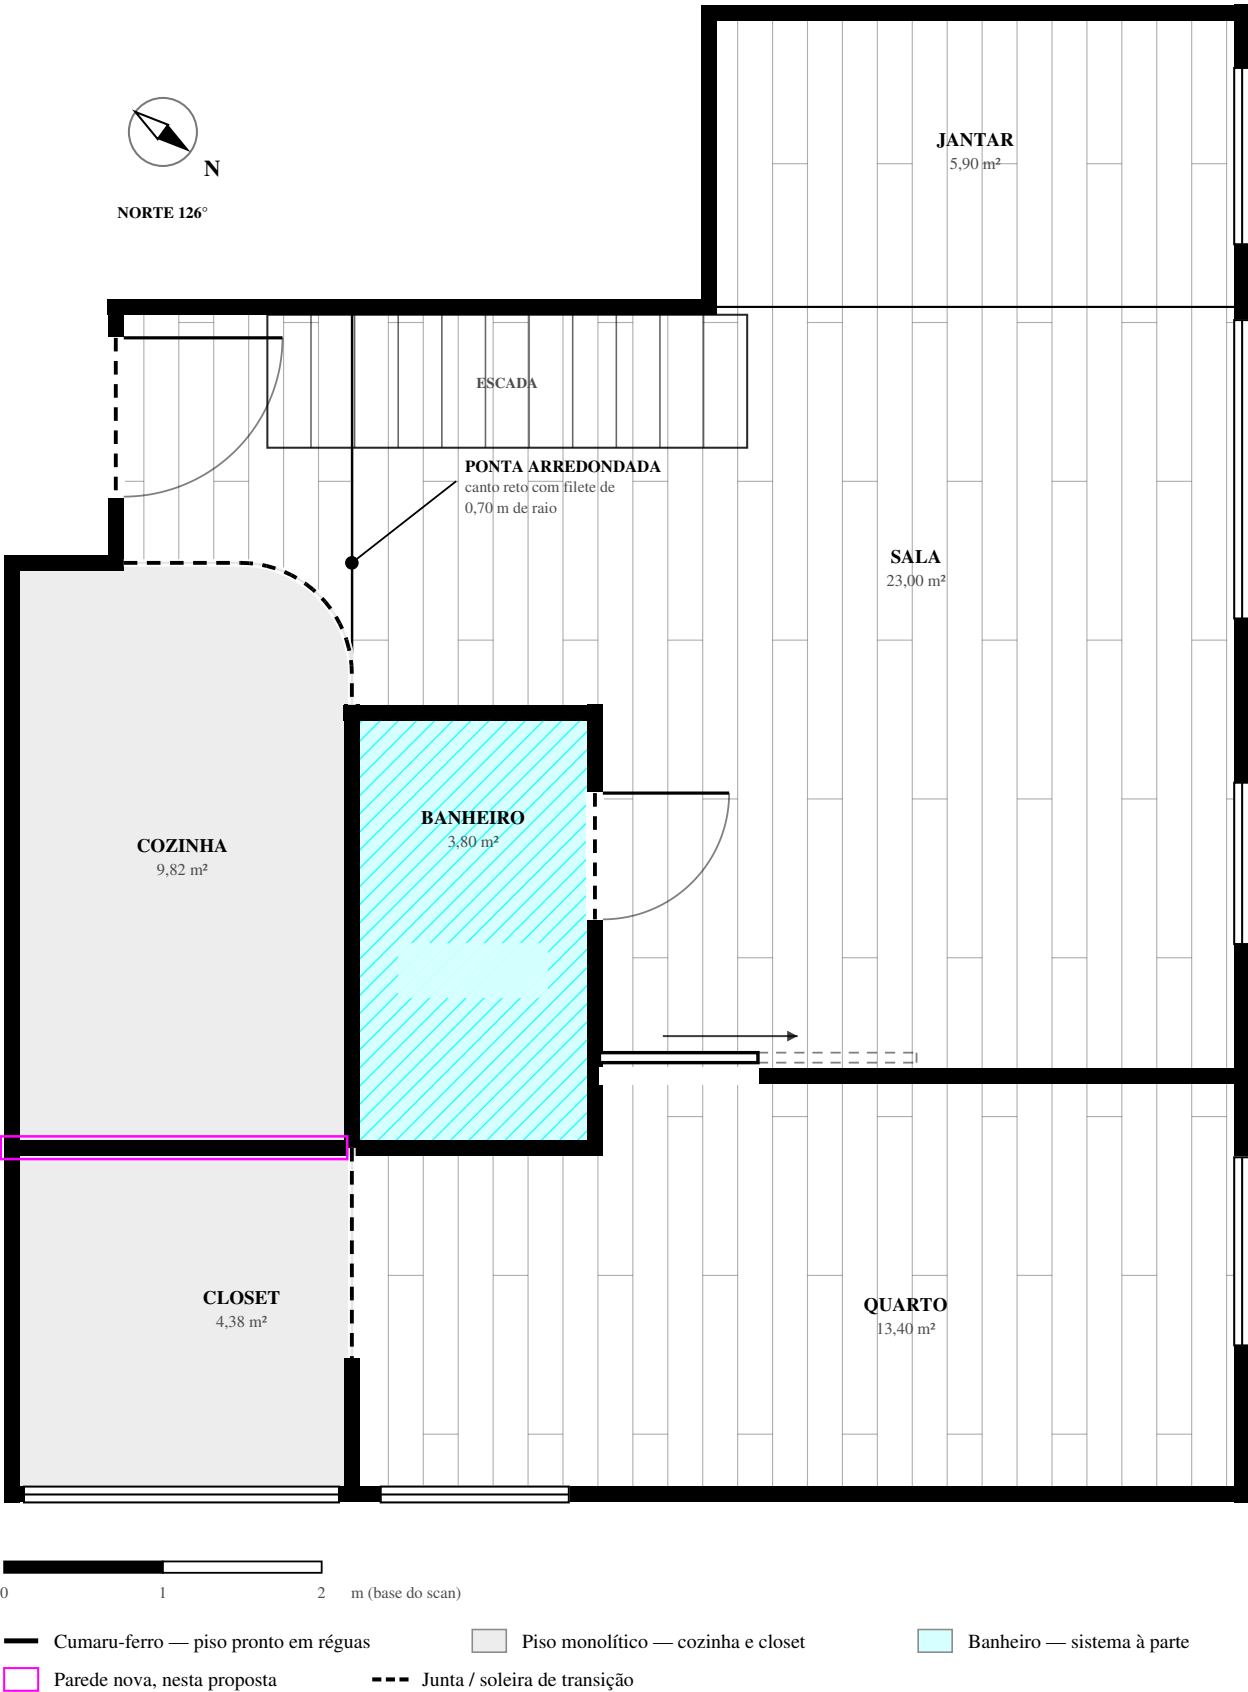

QUADRO DE ÁREAS

Sistema	Onde	Área
Cumaru-ferro	sala 23,00 + quarto 13,40 + jantar 5,90 + corredor 2,39	44,69 m²
+ reserva de 10%	cortes, perdas e reposição futura	49,16 m²
Monolítico	cozinha 7,43 (de 9,82) + closet 4,38 — zona contínua	11,81 m²
Banheiro	sistema à parte, área molhada, na mesma cota	3,80 m²
MainFloor	total do pavimento	60,30 m²

Nesta proposta, só a divisão interna cozinha/closet se move.

A zona monolítica inteira (cozinha + closet) já era desenhada como um único pano contínuo, de parede a parede — 11,81 m², sem mudança. O que muda é apenas quanto desse pano cada ambiente soma: cozinha passa de 6,51 para 7,43 m² dentro da zona; closet cai de 5,30 para 4,38 m². Nenhum corte de piso novo é criado por esta alteração.

A zona monolítica da opção A quase não tem problema de junta.

São 11,81 m² num pano estreito: cabe em um ou dois painéis, e a junta de material com o cumaru já resolve a maior parte do movimento. O desenho de juntas vira questão de verdade só na opção B, com 56,50 m² contínuos — ver a Prancha 04.

Cozinha e closet formam uma zona monolítica só.

A zona é um retângulo contínuo, da parede oeste até a linha da sala e do degrau até a fachada sul, passando pela abertura entre cozinha e closet. O corredor da entrada e a escada ficam em cumaru; o monolítico cobre a cozinha de trabalho e o closet.

A ponta é canto reto com filete de 0,70 m de raio.

Não é mais um arco achatado atravessando a cozinha: o limite corre reto pela linha do degrau, vira reto na linha da sala, e só a quina que aparece no corredor é arredondada. Um quarto de círculo tangente aos dois lados — geometria que o marceneiro e o aplicador sabem replicar com um compasso, e que o perfil de transição consegue acompanhar.

A junta é o detalhe mais caro desta opção.

Perfil de transição com junta de movimentação, reto nos trechos retos e curvo só no filete. E as duas espessuras têm de ser niveladas no contrapiso para se encontrarem rentes: régua pronta com manta e monolítico somam alturas diferentes, e é no contrapiso que se acerta a diferença, não na soleira.

Cumaru-ferro é madeira densa — o que é virtude e é risco.

Dureza e resistência altas, e por isso mesmo muito sensível a umidade e a base torta. Exige contrapiso seco, plano e nivelado (P06), aclimação das réguas no ambiente antes de assentar e folga de dilatação em todo o perímetro, escondida no rodapé. Piso pronto reduz obra, mas não dispensa nenhuma dessas três condições.

O desenho das réguas é hipótese, não especificação.

Réguas de 0,22 m correndo norte-sul, paralelas ao lado maior do pavimento, com topos a cada 3,00 m defasados de um terço. Largura, comprimento e sentido de assentamento são decisão de projeto: o sentido muda a leitura do espaço e a percepção do desnível do contrapiso.

O banheiro fica fora dos dois sistemas, mas na mesma cota.

Sistema próprio, com impermeabilização, caimento e acabamento antiderrapante, nivelado com o piso seco (P05): a soleira é junta de material, não degrau. Sem degrau, ralo linear e fecho de vidro assumem a contenção de água.