


Quadro de esquadrias e dados do levantamento

Idêntico à REV. M — nenhuma esquadria muda de vão nesta proposta. J06, a janela do closet, é a que fica mais perto da alteração.

seis janelas · três portas

nenhuma esquadria afetada por esta proposta

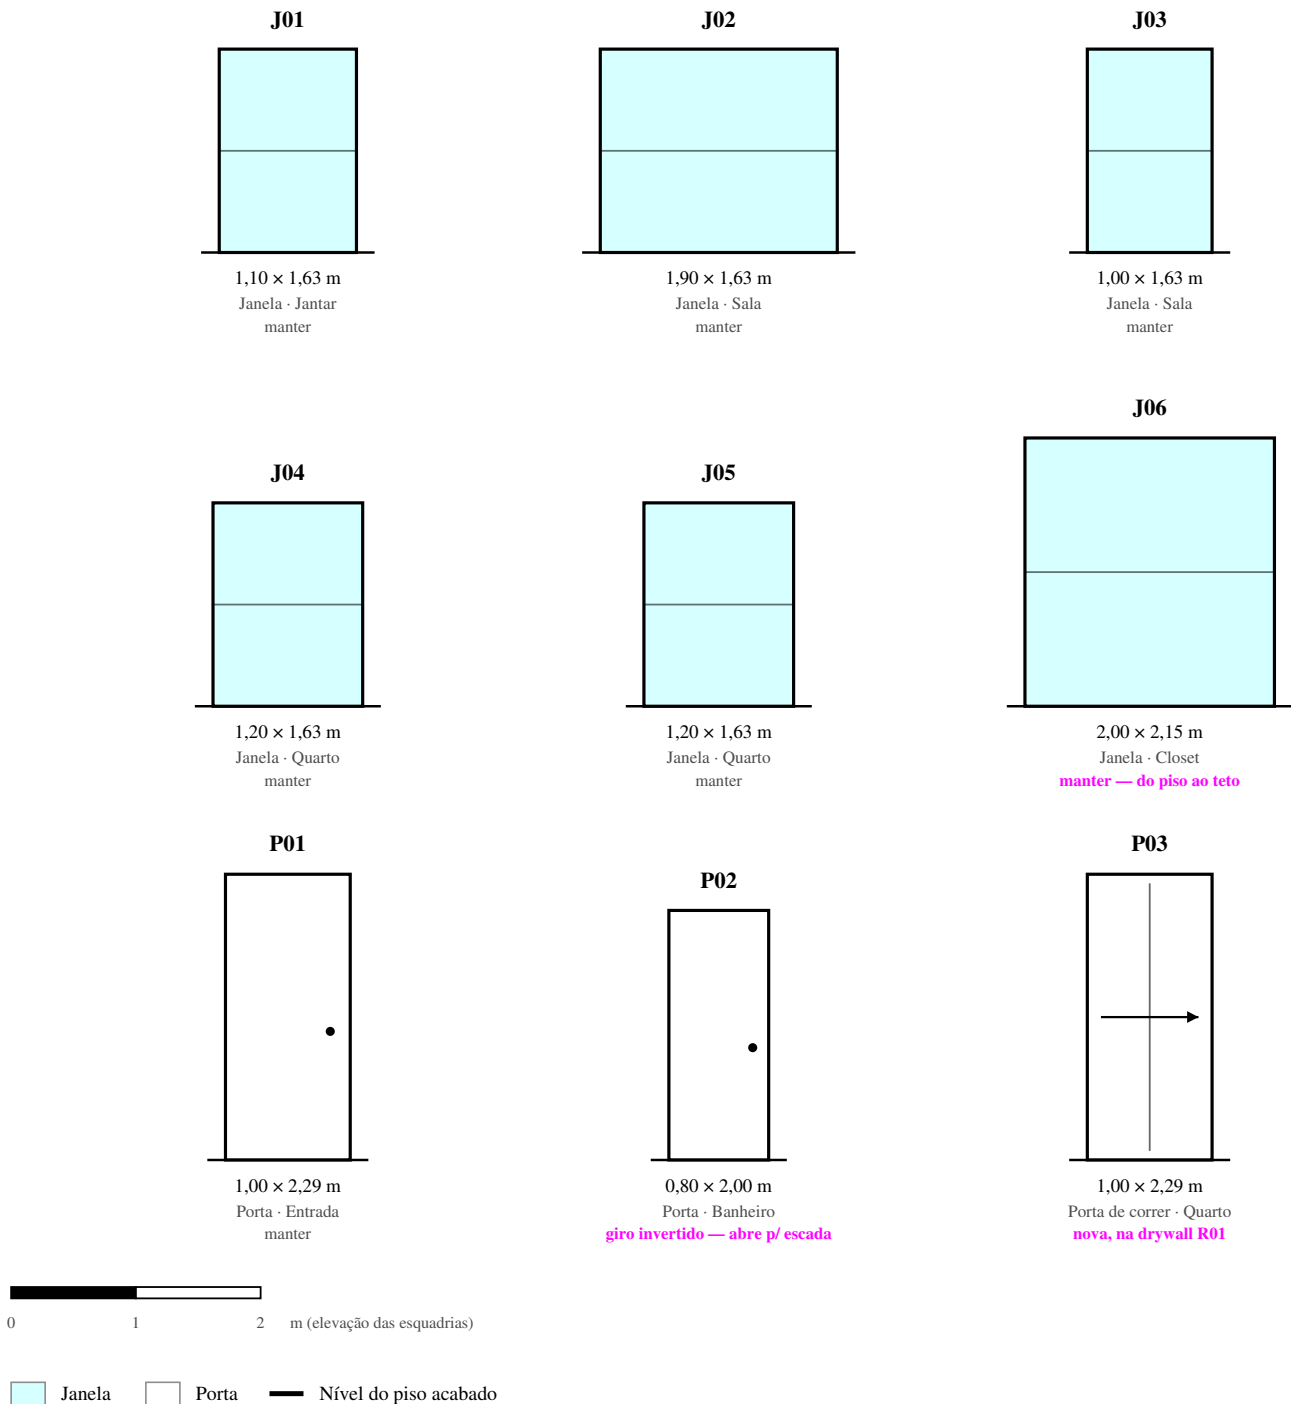

DADOS DO LEVANTAMENTO

Dado	Valor	Observação
Área útil (soma dos ambientes)	60,30 m²	relatório arredonda para 60,20
Área externa do pavimento	64,70 m²	inclui espessura de paredes
Área de parede	130,40 m²	sem vãos
Área de esquadria	14,73 m²	seis janelas, vão — scan dava 12,70
Volume	144,51 m³	com forro; ~158 m³ na laje aparente
Perímetro somado dos ambientes	78,10 m	não é perímetro do pavimento
Pé-direito — laje	2,62 m	depois de retirar o forro (D07)
Pé-direito — forro atual	2,40 m	plenum de 0,22 m
Captura / exportação	02.09 / 07.09.2026	scan 3D Polycam
Coordenadas	23°36'46,8"S 46°44'15,8"O	altitude 822 m — do scan superior
Norte	126°	do topo da folha, sentido horário

INVENTÁRIO DO SCAN — NÃO É ESPECIFICAÇÃO

Ambiente	Itens reconhecidos pelo scan (m)
Sala	sofá 2,60 × 1,60 · mesa de centro 1,60 × 1,00 · 3 cadeiras · armário 2,50 × 0,40 · escada 0,80 × 3,00
Quarto	cama 1,50 × 2,00 · bancada 3,00 × 0,50 · mesa 0,50 × 0,50 · cadeira
Cozinha	armário 1,60 × 0,60 · cuba 0,70 × 0,60 · geladeira 0,90 × 0,80 (h 1,80) · forno · cooktop · lava-louças
Jantar	armário de canto 2,50 × 0,40 — o canto alemão, item D05 da demolição
Closet	marcenaria não discriminada pelo scan — inventariar módulo a módulo antes de desmontar (M01)
Banheiro	bancada 1,70 × 0,40 · box 0,90 × 1,40 (h 2,10) · cuba 0,60 × 0,50 · bacia 0,40 × 0,70

Por que esta folha é igual à da REV. M.

A alteração desliza uma parede interna 0,45 m — nenhuma esquadria muda

de largura, altura ou posição. J06 (a janela do closet) é a mais próxima:

fica na parede sul, que esta proposta não toca, então seu vão de $2,00 \times$

2,15 m permanece igual. O que muda é a profundidade do ambiente através

delas, não o vão em si.

Todas na mesma escala. Largura $\times$ altura de vão livre, não de marco.

Peitoril, sentido de abertura e material não estão medidos: as três informações precisam de

visita. Nenhuma esquadria deste caderno está liberada para fabricação.

As alturas das janelas vieram do cliente, não do scan.

Cinco têm 1,63 m. A do closet (J06) vai do piso ao teto: 2,40 m de altura livre menos 0,15 m de

apoio no topo e 0,10 m de peitoril, dando $2,00 \times 2,15$ m — e é o único peitoril medido até agora.

As duas do quarto ficam idênticas, e a área de esquadria sobe de 12,70 para 14,73 m².

P03 é a única esquadria nova.

Porta de correr de 1,00 x 2,29 m na drywall reconstruída, com a folha estacionando no 1,00 m

de parede a leste do vão, pela face da sala. P02 mantém a folha existente de $0,80 \times 2,00$ m e

só inverte o giro. P01, a porta de entrada, mede $1,00 \times 2,29$ m e não é alterada.

O inventário do scan serve para escopo, não para especificação.

É o que o algoritmo reconheceu no dia da captura. Há erro evidente — uma "mesa lateral" de

6,60 x 2,00 m que é a projeção da escada — e há ausência: o closet inteiro não foi

discriminado. Use a lista para conferir o que sai, o que se desmonta e o que volta.

O que este caderno ainda não tem, e que um executivo exige:

projeto estrutural para a furação da laje e a área da piscina; hidráulica e esgoto do banheiro

e da cozinha; elétrico executivo com diagrama unifilar e cálculo de demanda; projeto de

juntas do piso monolítico; detalhamento de marcenaria; e aprovação do condomínio.