


Demolição e preparo

Escopo de retirada, preparo de superfícies e reconstruções. Planta no estado existente.

FO1 — DEMOLIÇÃO

extraído do caderno de estudo REV. N

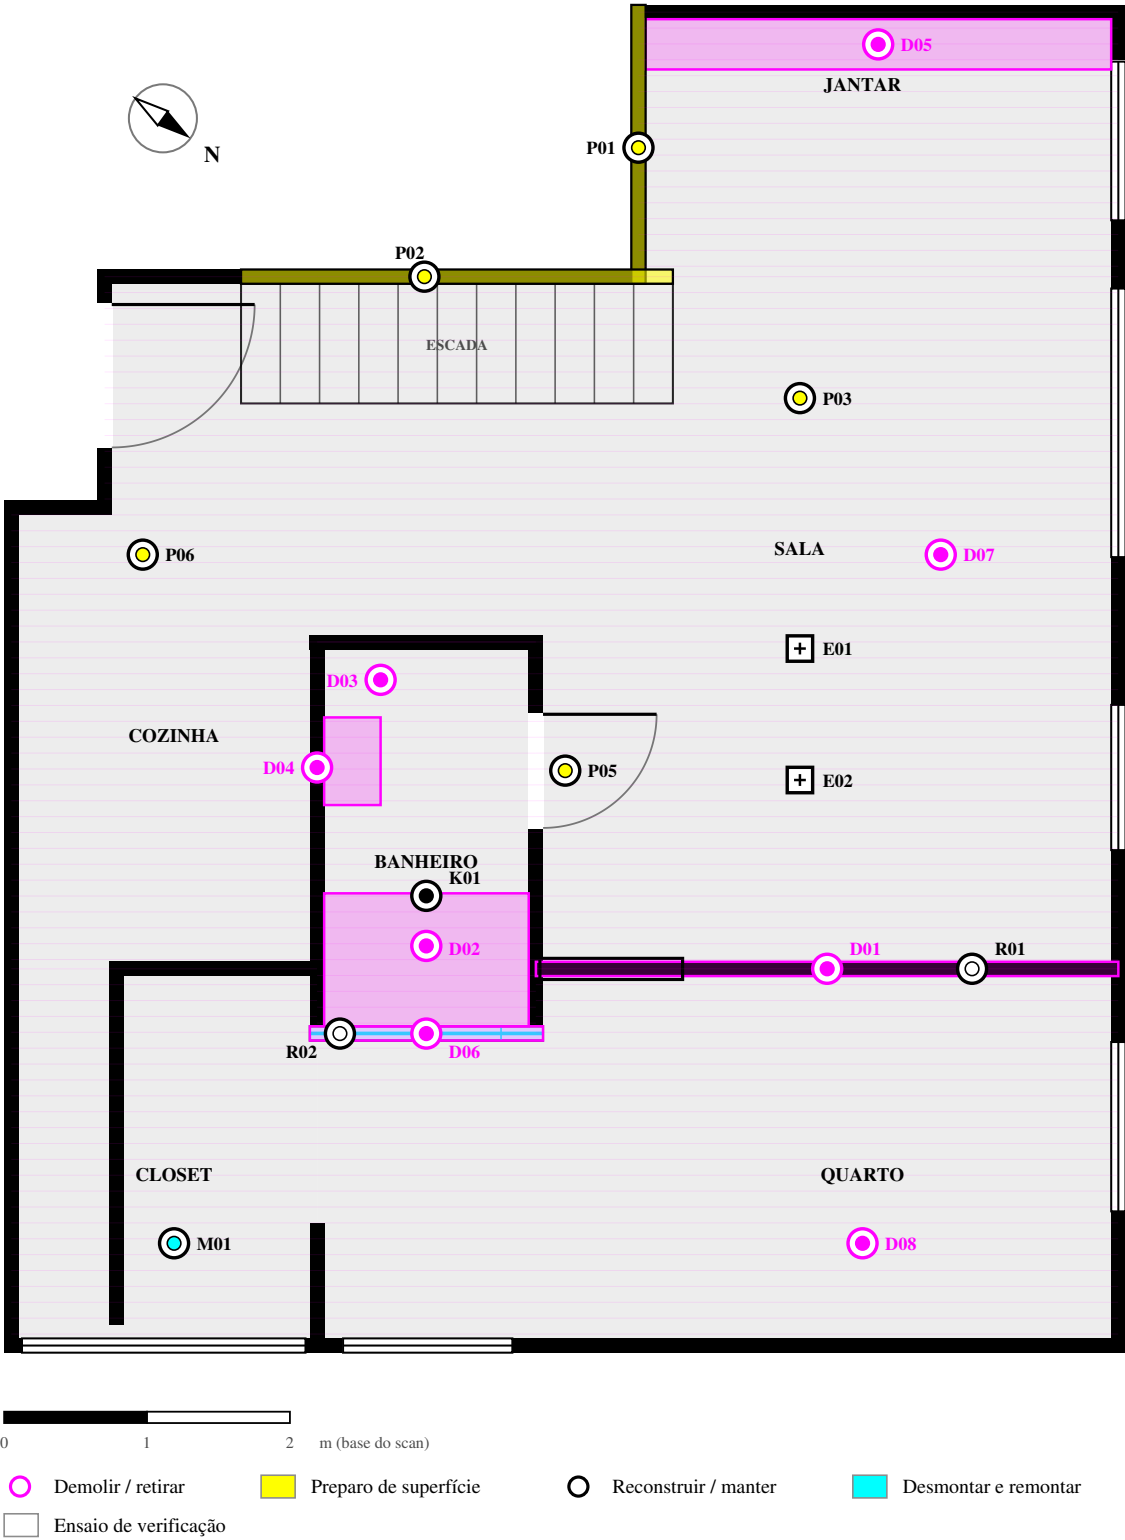

SEQUÊNCIA GERAL DA OBRA

1 Ensaio e proteção	2 Demolição	3 Preparo de superfícies	4 Infraestrutura	5 Reconstruções	6 Piso	7 Pintura	8 Marcenaria e luminárias
---------------------	-------------	--------------------------	------------------	-----------------	--------	-----------	---------------------------

ESCOPO — TAREFA E QUANTIDADE

ID	Tarefa	Quantidade
E01	Ensaio de estanqueidade (pressão) na hidráulica	1 ensaio
E02	Medição de resistência de isolamento na elétrica	1 ensaio
M01	Desmontar closet, etiquetar módulos e ferragens, acondicionar	1 conjunto
D05	Retirar canto alemão do jantar	1 conjunto
D07	Retirar forro — 100%	60,30 m²
D01	Demolir drywall entre sala e quarto	4,08 m
D02	Demolir fechamento e base do box do banheiro	1 conjunto
D06	Demolir pano de vidro chão-teto do fundo do box	1,63 m
D04	Demolir parede atrás do espelho e da bancada do banheiro	2,64 m a conferir
D08	Retirar pisos do MainFloor	60,30 m²
D03	Retirar piso, base e rebaixo do banheiro até a laje	3,80 m²
P01	Parede do jantar: retirar espelho e revestimento	1,95 m
P02	Parede sob a escada: retirar revestimento	a confirmar
P04	Demais paredes com revestimento retirado	mapear em obra
P03	Laje: restaurar, descascar, limpar e preparar	60,30 m²
P06	Regularizar e lixar todo o contrapiso — plano e nivelado	60,30 m²
P05	Nivelar o banheiro na cota do piso da casa	cota única
R01	Reconstruir drywall sala/quarto com vão de porta 1,00 × 2,29 m	4,08 m + 1 vão
R02	Construir parede de fechamento do fundo do box	1,63 m
K01	Vidro do box — MANTER e proteger	1 peça

ORDEM DE EXECUÇÃO

- Ensaio antes de qualquer demolição — E01 e E02.**
Resultado por escrito antes de abrir parede ou piso.
- Proteção e canteiro.**
Proteger K01, esquadrias, prumadas e caixilhos. Isolar acessos e prever remoção de entulho e horário de condomínio.
- Desmontagem — M01 e D05.**
Closet etiquetado e acondicionado; canto alemão do jantar.
- Forro — D07, 100%.**
Libera a laje e revela a altura livre real.
- Vedações — D01, D02, D06 e D04.**
- Pisos e base — D08 e D03.**
Banheiro desce até a laje.
- Revestimentos de parede — P01, P02 e P04.**
- Laje — P03.**
Restauo, descascamento e limpeza.
- Reconstruções — R01 e R02.**
R01 fecha somente após a infraestrutura elétrica embutida.
- Contrapiso e nível — P06 e P05.**
Última etapa desta disciplina. Entregar plano, nivelado, seco e limpo, em cota única, para liberar o piso.