Planta baixa cotada — estado proposto

Folha de referência dimensional. Cotas em metros, sobre o levantamento por scan de 02.09.2026; conferir em campo antes de qualquer medição.

norte 126° — medido pela rosa do pavimento superior

pé-direito 2,62 m na laje · 2,40 m com o forro atual

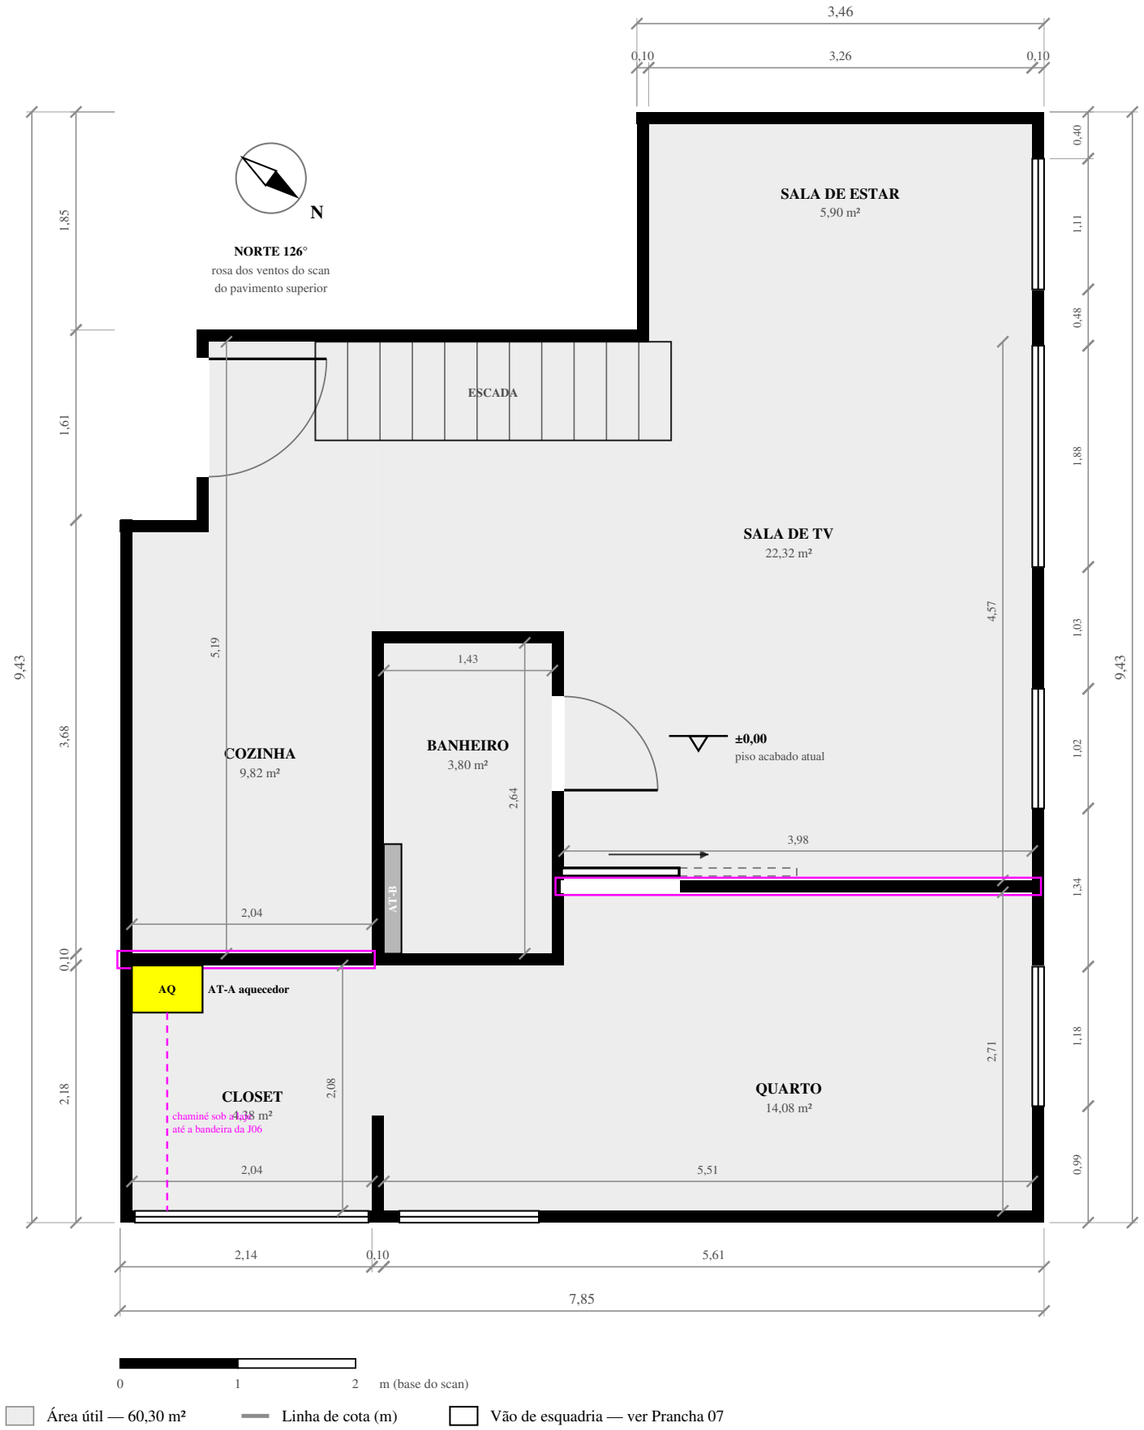

QUADRO DE AMBIENTES — LEVANTAMENTO (m, m²)

Ambiente	Área	Perímetro	Bounding box	Inscrita
Sala de TV	22,32 m²	20,4 m	5,6 × 4,6	4,8 × 3,8
Quarto	14,08 m²	16,5 m	5,6 × 2,7	5,6 × 2,3
Cozinha	9,82 m²	14,6 m	5,2 × 2,1	5,2 × 1,4
Sala de estar	5,90 m²	10,1 m	3,3 × 1,8	—
Closet	4,38 m²	8,4 m	2,1 × 2,1	—
Banheiro	3,80 m²	8,1 m	2,6 × 1,4	—
MainFloor	60,30 m²	78,1 m	7,85 × 9,43	—

Alternativo A: a parede cozinha/closet desce 0,45 m para o sul.
Fica alinhada à face sul do banheiro e segue até a parede externa oeste (R04, tracejada em magenta). A cozinha passa de 8,90 para 9,82 m² e o closet de 5,30 para 4,38 m²; a soma das duas e a área do MainFloor não mudam. A largura livre comum, 2,04 m, também não.

Alternativo A: a drywall sala de TV/quarto (R01) volta 0,17 m mais ao norte.
O quarto passa de 2,54 para 2,71 m livres (de 13,40 para 14,08 m²) e a sala de TV de 23,00 para 22,32 m². A porta de correr P03 acompanha a parede; o comprimento da drywall não muda.

Como esta planta foi levantada.
Scan 3D Polycam, captura de 02.09.2026, relatório exportado em 07.09.2026. Paredes, vãos e polígonos de ambiente foram lidos do vetor do arquivo em pontos PDF e convertidos pela escala 45,66 pt/m, conferida duas vezes contra as cotas gerais: 358,33 pt / 7,85 m e 430,56 pt / 9,43 m. O próprio relatório avisa que são estimativas — nenhuma cota aqui substitui medição em campo.

Pé-direito: 2,40 m com o forro atual, 2,62 m na laje.
Alturas informadas pelo cliente; o relatório do scan mede 2,40 m com forro, o que confere. Com a retirada total do forro (D07) ganham-se os 0,22 m de plenum. É essa folga que acomoda a porta de correr de 2,29 m: sob o forro de hoje sobrariam 0,13 m, e sobre a laje sobram 0,33 m — espaço para o trilho aparente. Volume passa de 144,51 m³ para cerca de 158 m³ com a laje aparente.

Espessuras e níveis: uma cota única para o pavimento.
Todas as paredes lidas no scan têm 0,10 m. A nova drywall (R01) repete a espessura, salvo se o trilho da porta de correr for embutido em cassete — aí a parede engrossa. O banheiro passa a nascer na mesma cota do piso seco (P05), sem degrau de soleira, e todo o contrapiso é lixado e nivelado (P06): ±0,00 é o piso acabado atual, e o nível final precisa ser amarrado ao hall.

Diferença entre as áreas do relatório.
Área externa 64,70 m² (inclui paredes), área útil 60,20 m² pelo relatório e 60,30 m² pela soma dos seis ambientes — a diferença é arredondamento. O caderno usa 60,30 m². Área de parede 130,40 m², área de janela 12,70 m², perímetro somado dos ambientes 78,10 m.

O norte foi medido, não arbitrado: 126° do topo da folha.
O relatório do pavimento superior — mesma captura — traz rosa dos ventos e GPS; o do MainFloor não traz nenhum dos dois. As duas plantas estão desenhadas com 180° de diferença, confirmado por dois elementos que os pavimentos compartilham: a caixa da escada e a área da piscina, que só cai no terraço de cima com essa rotação. A pétala N do Upfloor marca −53,97°; somados 180°, dá 126°.

As duas fachadas envidraçadas dão para NOROESTE e NORDESTE.

ÁREAS TÉCNICAS · DA REV. Q (22/10/2026)

AT-B · área técnica do banho/chuveiro: na parede oeste do banheiro (a mesma da bancada), ao longo de todo o box; 0,93 × 0,15 m. Profundidade estimada (0,15 m, planta original do proprietário) — confirmar em campo depois do D04. Prumada do condomínio: não demolir. AT-A · aquecimento: aquecedor a gás no closet, nicho ~0,60 × 0,40 m piso-laje na parede de divisa, alinhado ao D09; chaminé sob a laje até a bandeira da J06 (posição no comprimento da parede esquemática). NBR 13103: o closet (~11–14 m³) fica abaixo do volume de referência — nicho fechado em material incombustível, ventilação permanente para o exterior e chaminé própria. Liberação obrigatória por instalador credenciado / Comgás antes da infraestrutura. Áreas líquidas com as áreas técnicas: closet 4,14 m² (era 4,38), banheiro 3,66 m² (−0,14 m² do shaft).

Cotas extraídas do modelo do scan e arredondadas ao centímetro. O relatório do levantamento declara que os valores são estimativas: conferir em campo antes de fabricar esquadria, marcenaria ou bancada.
Planta de estudo preliminar. Não é planta executiva liberada: faltam projeto estrutural, hidráulica, elétrico executivo e aprovação do condomínio.