Opção A — monolítico, cozinha e closet em porcelanato

Monolítico nas áreas de estar e dormir; cozinha e closet numa zona contínua de porcelanato. Cores e paginação ilustrativas.

norte 126° · Prancha 03 de 14

ponta arredondada: canto reto com filete de 0,70 m

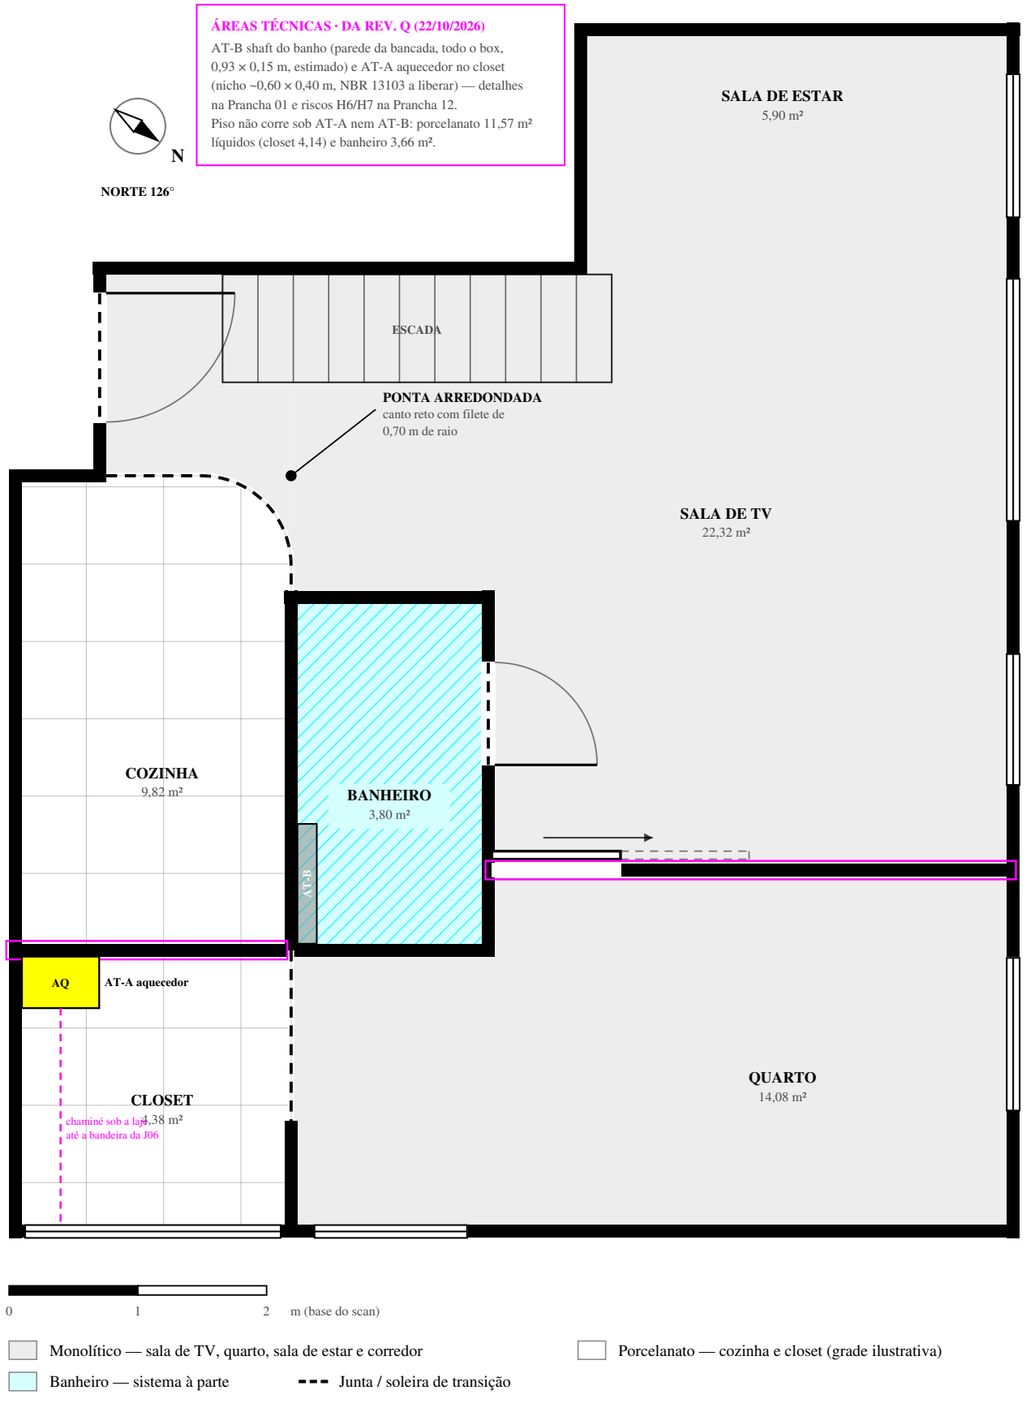

QUADRO DE ÁREAS

Sistema	Onde	Área
Monolítico	sala de TV 22,32 + quarto 14,08 + sala de estar 5,90 + corredor 2,39	44,69 m²
Sem reserva	moldado in loco, sem perda de corte	—
Porcelanato	cozinha 7,43 (de 9,82) + closet 4,14 líquidos (sem o AT-A)	11,57 m²
+ reserva de 10%	cortes, perdas e reposição futura	12,73 m²
Banheiro	sistema à parte, na mesma cota — 3,66 líquidos sem o AT-B	3,80 m²
MainFloor	total do pavimento	60,30 m²

Alternativo A: os dois materiais trocam de lugar.
Onde era cumaru-ferro — sala de TV, quarto, sala de estar e corredor — entra o monolítico; onde era monolítico — cozinha e closet — entra porcelanato. O contorno da zona e a ponta arredondada não mudam.

O monolítico agora é o pano grande: 44,69 m² pedem projeto de juntas.
Cimentício trabalha em painéis de 3 a 6 m de lado; microcimento reduz as juntas às do substrato e ao perímetro. Lugares naturais: as soleiras da entrada e do banheiro, a linha da porta de correr P03 e o encontro com o porcelanato. Pedir a paginação de juntas junto com a proposta.

Porcelanato na cozinha e no closet: formato, cor e rejunte a definir.
A grade de 0,60 m do desenho é ilustrativa. Juntas de assentamento e de movimentação conforme o fabricante e a NBR 13753; reserva de 10% para cortes e reposição.

Na ponta arredondada o monolítico acompanha e o porcelanato é cortado.
Filete de 0,70 m de raio, canto reto nos demais trechos. O monolítico, moldado in loco, segue a curva sem esforço; do lado do porcelanato as peças são cortadas em curva (jato d'água ou serra) e o perfil de transição curvo fica no encontro.

As duas espessuras se acertam no contrapiso, não na soleira.
Porcelanato com argamassa colante e monolítico somam alturas diferentes: o acerto é no contrapiso (P06), para os dois se encontrarem rentes, sem degrau.

Sequência sugerida: porcelanato e perfil, depois o monolítico.
O monolítico é aplicado contra o perfil de transição já fixado e cura antes da marcenaria: o closet (M01) só volta com o piso curado.

O banheiro fica fora dos dois sistemas, mas na mesma cota.
Sistema próprio, com impermeabilização, caimento e acabamento antiderrapante, nivelado com o piso seco (P05): a soleira é junta de material, não degrau. Sem degrau, ralo linear e fecho de vidro assumem a contenção de água.

Revestimento contínuo: toda a área de piso é revestida, inclusive sob móveis e equipamentos — nenhum recorte de mobiliário foi descontado. Áreas conforme o scan de 02.09.2026.
Estudo preliminar de superfície: não substitui especificação de sistema, projeto de juntas nem memorial de aplicação do fornecedor.